

PROJECT:
TASTE OF VILLAGE

LOCATION:
260 FARNHAM ROAD, SLOUGH SL14XL LONDON UK



36 ARCLAY CLOSE UB8 3WP
UXBRIDGE LONDON UK

+44 743 8881857

TABLE OF CONTENTS

DRG. NO	DESCRIPTION	DRG. NO	DESCRIPTION
INTERIOR DRAWINGS			
ID-01	PROPOSED PLAN	ID-22	GRILL / COUNTER SECTION AT B-B'
ID-02	3D VIEWS	ID-23	MAIN ENTRANCE PLAN
ID-03	3D VIEWS	ID-24	MAIN ENTRANCE ELEVATION
ID-04	GENERAL ARRANGEMENT PLAN	ID-25	TOILET WORKING PLAN
ID-05	WALL IDENTIFICATION PLAN	ID-26	TOILET WORKING ELEVATION-01
ID-06	PLUMBING PLAN	ID-27	TOILET WORKING ELEVATION-02
ID-07	HVAC PLAN	ID-28	TOILET WORKING ELEVATION-03
ID-08	ELECTRICAL INSTALLATION PLAN	ID-29	TOILET WORKING ELEVATION-04
ID-09	LIGHTING PLAN	ID-30	TOILET TILE LAYOUT PLAN
ID-10	CEILING PLAN	ID-31	TOILET TILE LAYOUT ELEVATION-01
ID-11	CEILING PANEL DETAIL	ID-32	TOILET TILE LAYOUT ELEVATION-02
ID-12	FLOOR FINISHING PLAN	ID-33	TOILET TILE LAYOUT ELEVATION-03
ID-13	WALL FINISHING PLAN	ID-34	TOILET TILE LAYOUT ELEVATION-04
ID-14	ARCH FEATURE WALL ELEVATION -01	ID-35	CAMERA SURVEILLANCE PLAN
ID-15	ARCH FEATURE WALL CNC CUTTING BLOWUP DETAIL	ID-36	FIRE STRATEGY PLAN
ID-16	CNC CUTTING FEATURE WALL ELEVATION -02	ID-37	PLACEMENT PLAN TECH EQUIPMENTS
ID-17	FEATURE WALL ELEVATION -03	ID-38	PLACEMENT PLAN KITCHEN EQUIPMENTS
ID-18	GRILL / COUNTER PLAN	ID-39	FURNITURE LAYOUT PLAN
ID-19	GRILL / COUNTER FRONT ELEVATION	ID-40	PLACEMENT PLAN SANITARY EQUIPMENTS
ID-20	GRILL / COUNTER SIDE ELEVATION		
ID-21	GRILL / COUNTER SECTION AT A-A'		



36 ARCLAY CLOSE UB8 3WP
UXBRIDGE LONDON UK
+44 743 8881857

PROJECT NAME:

TASTE OF VILLAGE

OWNER'S NAME:

TASTE OF VILLAGE

PRINCIPAL ARCHITECT;

M.S.

TITLE

LIST OF DRAWINGS

CHECKED BY :

M.S.

DRAWN BY:

FAIZAN ALI

Revised Dates :

Rev. _____

Rev. _____

Rev. _____

Rev. _____

SCALE:

N.T.S

DATE:

22-10-2025

JOB NO.

25.1030

DRG NO.

ID -00

NOTES:

PRESENTATION
DRAWING NOT FOR
CONSTRUCTION



36 ARCLAY CLOSE UB8 3WP
UXBRIDGE LONDON UK

+44 743 8881857

PROJECT NAME:

TASTE OF VILLAGE

OWNER'S NAME:

TASTE OF VILLAGE

PRINCIPAL ARCHITECT;

M.S.

TITLE

GROUND FLOOR
PROPOSED PLAN

CHECKED BY :

M.S.

DRAWN BY:

FAIZAN ALI

Revised Dates :

Rev. _____

Rev. _____

Rev. _____

Rev. _____

SCALE:

N.T.S

DATE:

22-10-2025

JOB NO.


25.1030


DRG NO.

ID -01

NOTES:

PRESENTATION
DRAWING NOT FOR
CONSTRUCTION

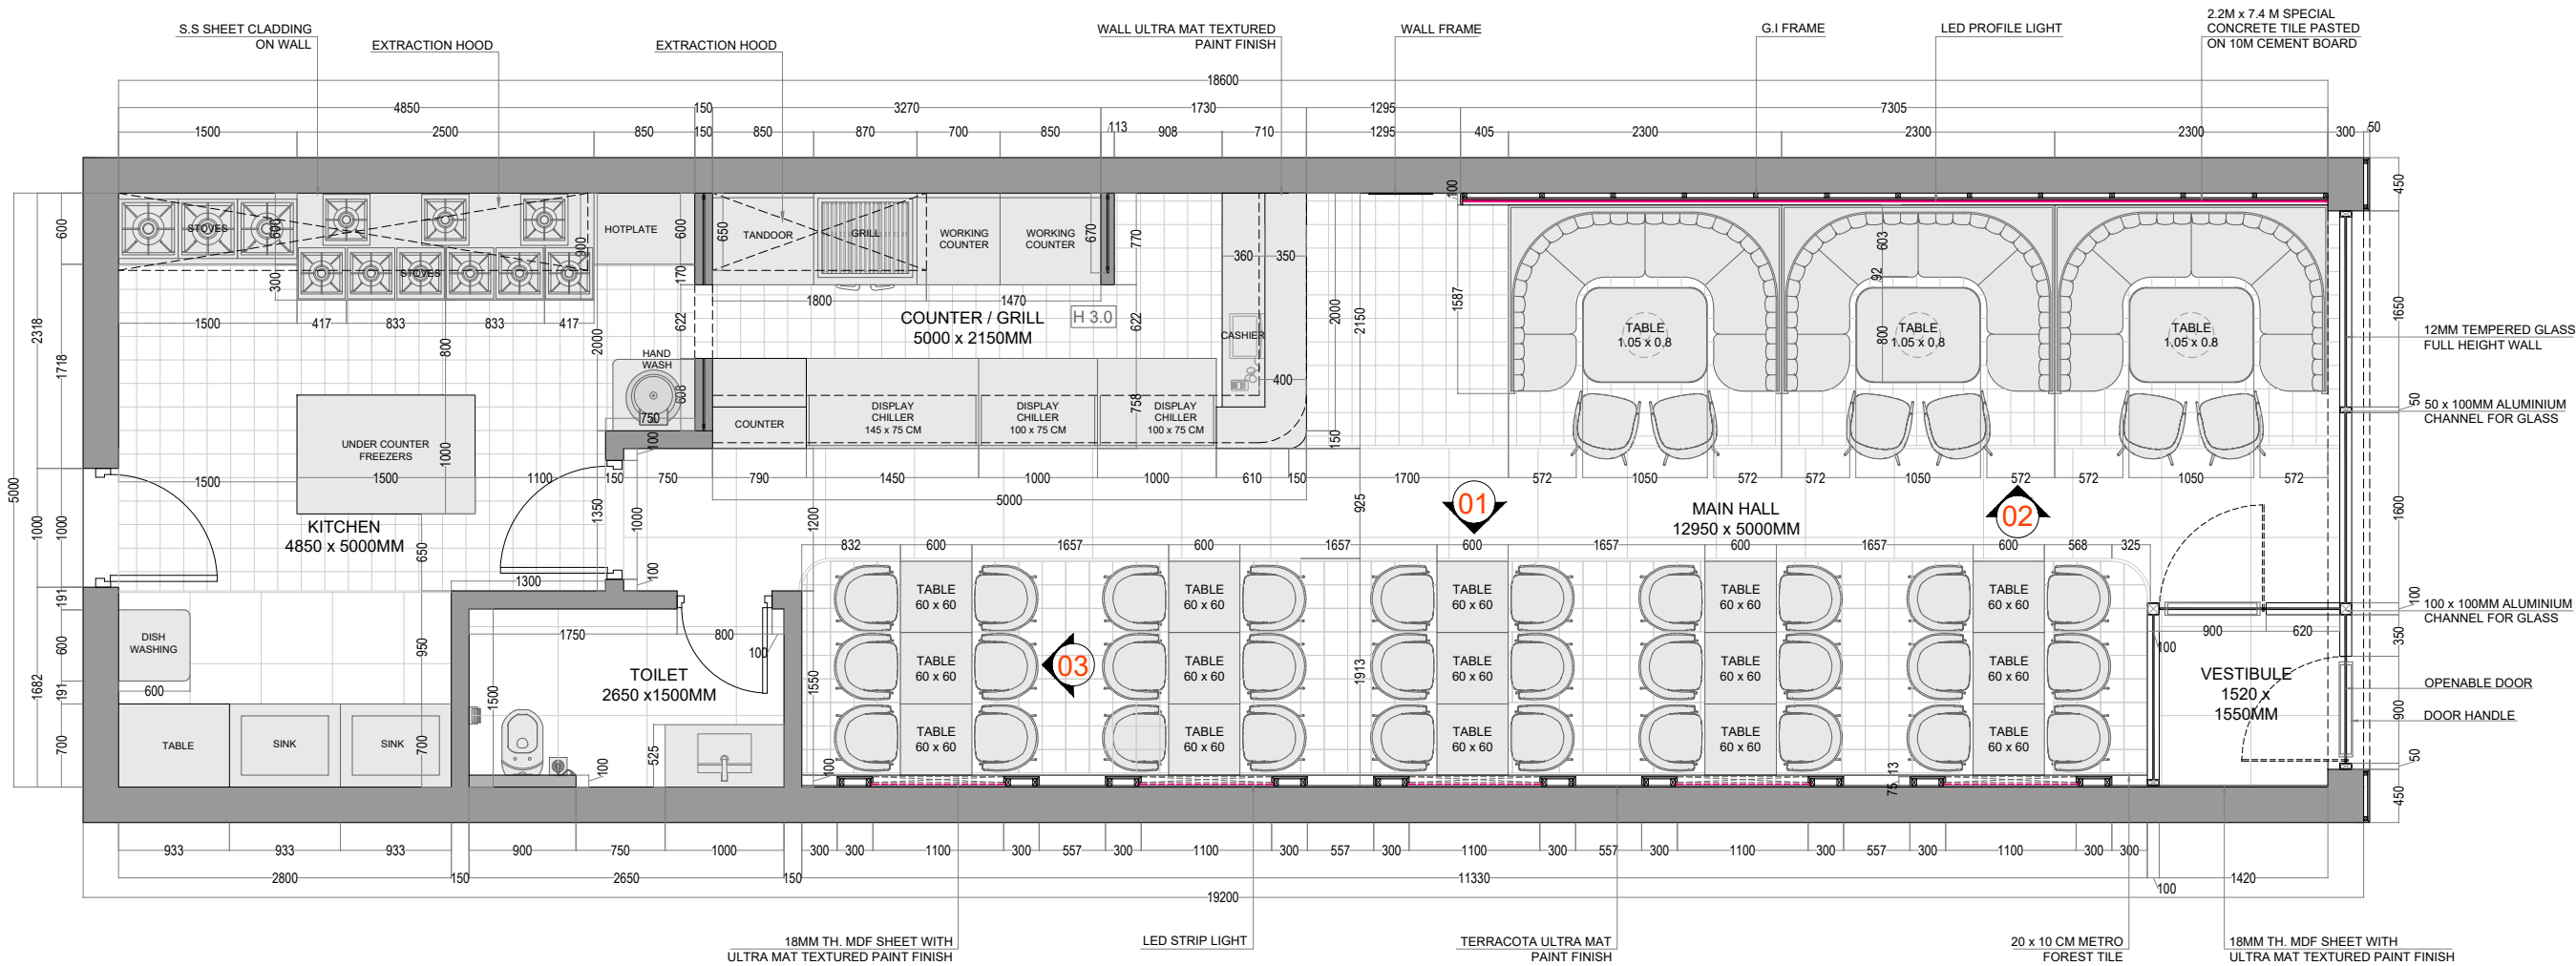

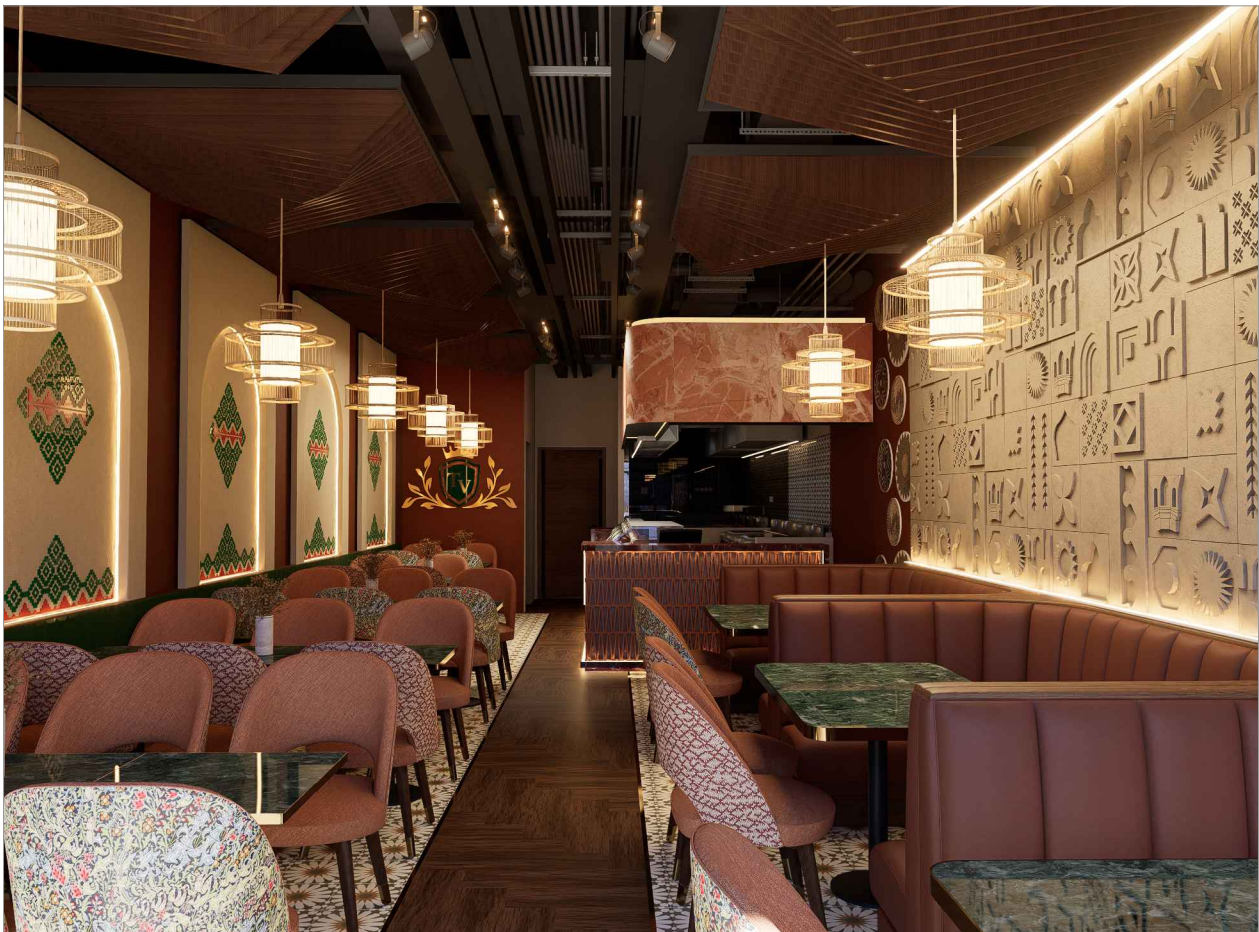

36 ARCLAY CLOSE UB8 3WP
UXBRIDGE LONDON UK
+44 743 8881857

PROJECT NAME:

TASTE OF VILLAGE

OWNER'S NAME:

TASTE OF VILLAGE

PRINCIPAL ARCHITECT;

M.S.

TITLE

3D VIEWS

CHECKED BY :

M.S.

DRAWN BY:

FAIZAN ALI

Revised Dates :

Rev. _____

Rev. _____

Rev. _____

Rev. _____

SCALE:

N.T.S

DATE:

22-10-2025

JOB NO.


25.1030

DRG NO.

ID -02

NOTES:

PRESENTATION
DRAWING NOT FOR
CONSTRUCTION

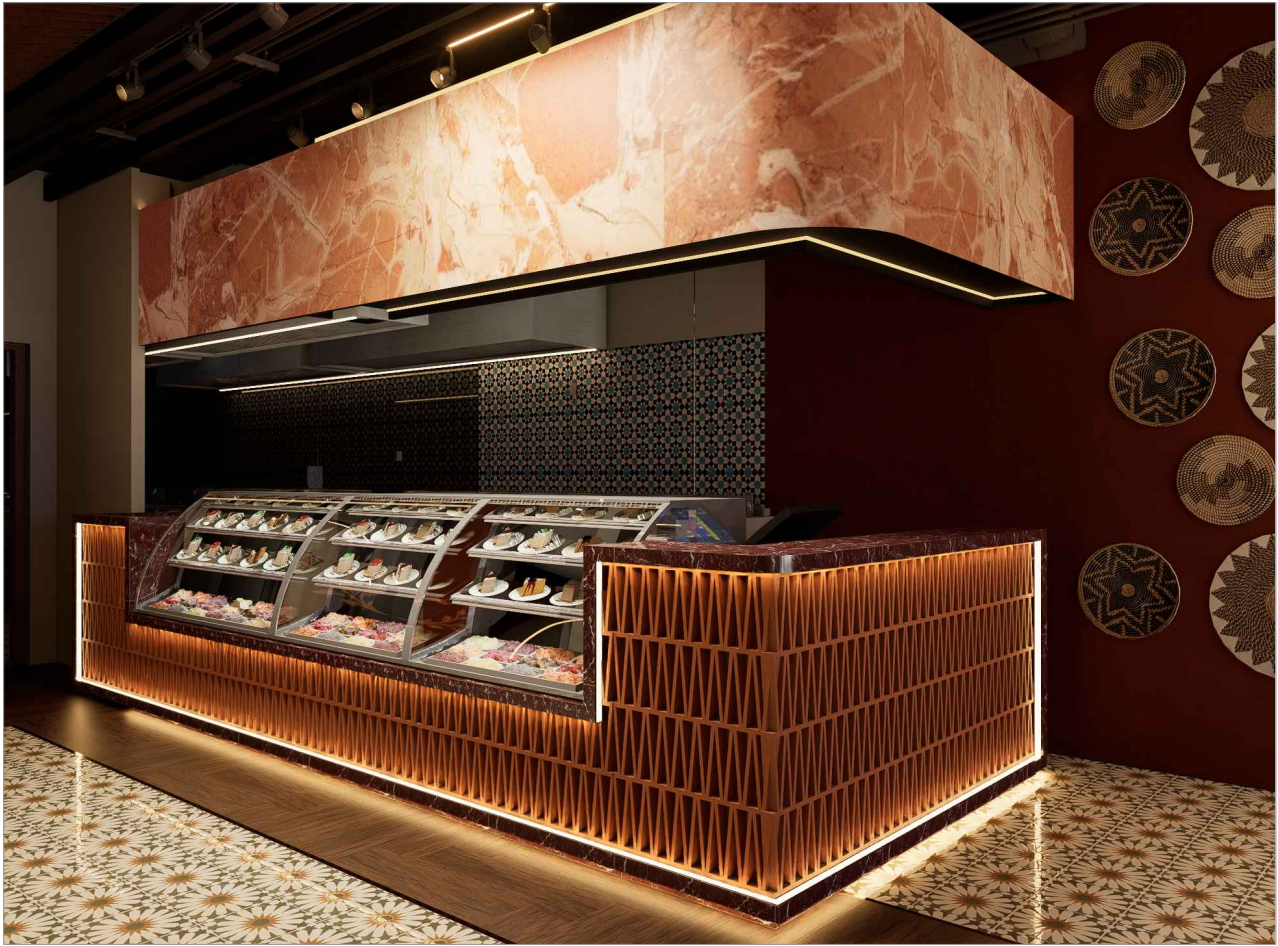

36 ARCLAY CLOSE UB8 3WP
UXBRIDGE LONDON UK
+44 743 8881857

PROJECT NAME:

TASTE OF VILLAGE

OWNER'S NAME:

TASTE OF VILLAGE

PRINCIPAL ARCHITECT:

M.S.

TITLE

3D VIEWS

CHECKED BY :

M.S.

DRAWN BY:

FAIZAN ALI

Revised Dates :

Rev. _____

Rev. _____

Rev. _____

Rev. _____

SCALE:

N.T.S

DATE:

22-10-2025

JOB NO.

25.1030


DRG NO.

ID -03

NOTES:

PRESENTATION
DRAWING NOT FOR
CONSTRUCTION

HVAC	
	CEILING CASSETTE AIR CONDITION 60 X 60 CM
	AIR CURTAIN
	EXTRACT & AIR INPUT HOOD
	EXHAUST FAN 30 x 30 CM

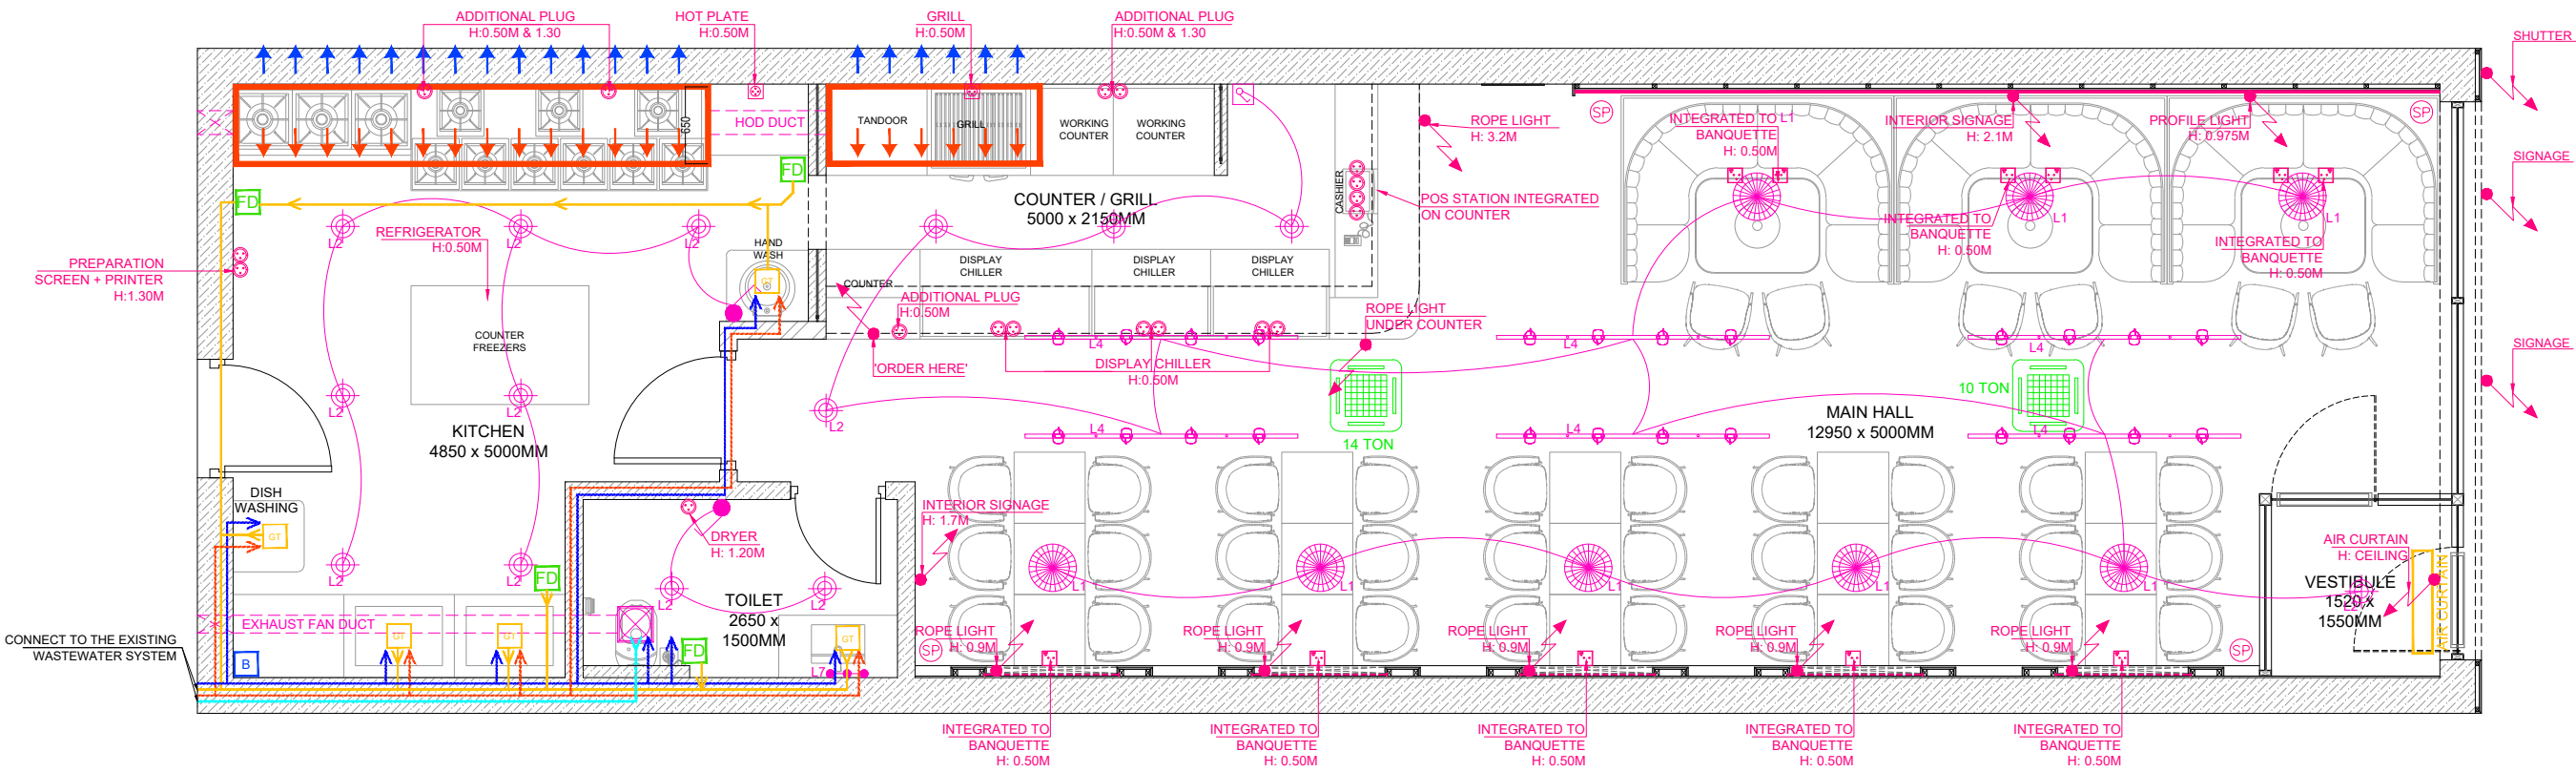

36 ARCLAY CLOSE UB8 3WP
UXBRIDGE LONDON UK
+44 743 8881857

PROJECT NAME:

TASTE OF VILLAGE

OWNER'S NAME:

TASTE OF VILLAGE

PRINCIPAL ARCHITECT;

M.S.

TITLE
GROUND FLOOR
GENERAL ARRANGEMENT PLAN

CHECKED BY:

M.S.

DRAWN BY:

FAIZAN ALI

Revised Dates:

Rev.

Rev.

Rev.

Rev.

SCALE:

N.T.S

DATE:

22-10-2025

JOB NO.


25.1030


DRG NO.

ID -04

NOTES:

PRESENTATION
DRAWING NOT FOR
CONSTRUCTION

 REPRESENTATION					
CODE	PW -1	PW -2	WL -1	WL -2	WL -3
DETAIL					
TYPE	PARTITION WALL	PARTITION WALL	WALL LINING	WALL LINING	WALL LINING
PARTITION THICKNESS (MM)	150 MM	150 & 112MM	70MM	70MM	6MM
FIRE INSULATION	1/2 H	1 H	1 H	1/2 H	-----
SOUND INSULATION	47dB	-----	-----	-----	-----
CHARACTERISTIC	one layer of gyproc sound bloc 12.5 mm each side of gyp frame 70 as 50 + 50mm isover acoustic partition roll	one layer of gyproc fire line 15mm mm each side of gyp frame 70 as 50	one layer of gyproc fire line 15mm one side of gyp frame 48 s 50mm isover acoustic partition	one layer of gyproc 15mm one side of gyp frame 48 s 50 'c' stud + 50mm isover acoustic partition roll	one layer of gyproc fireline 6mm fixed on an existing wall

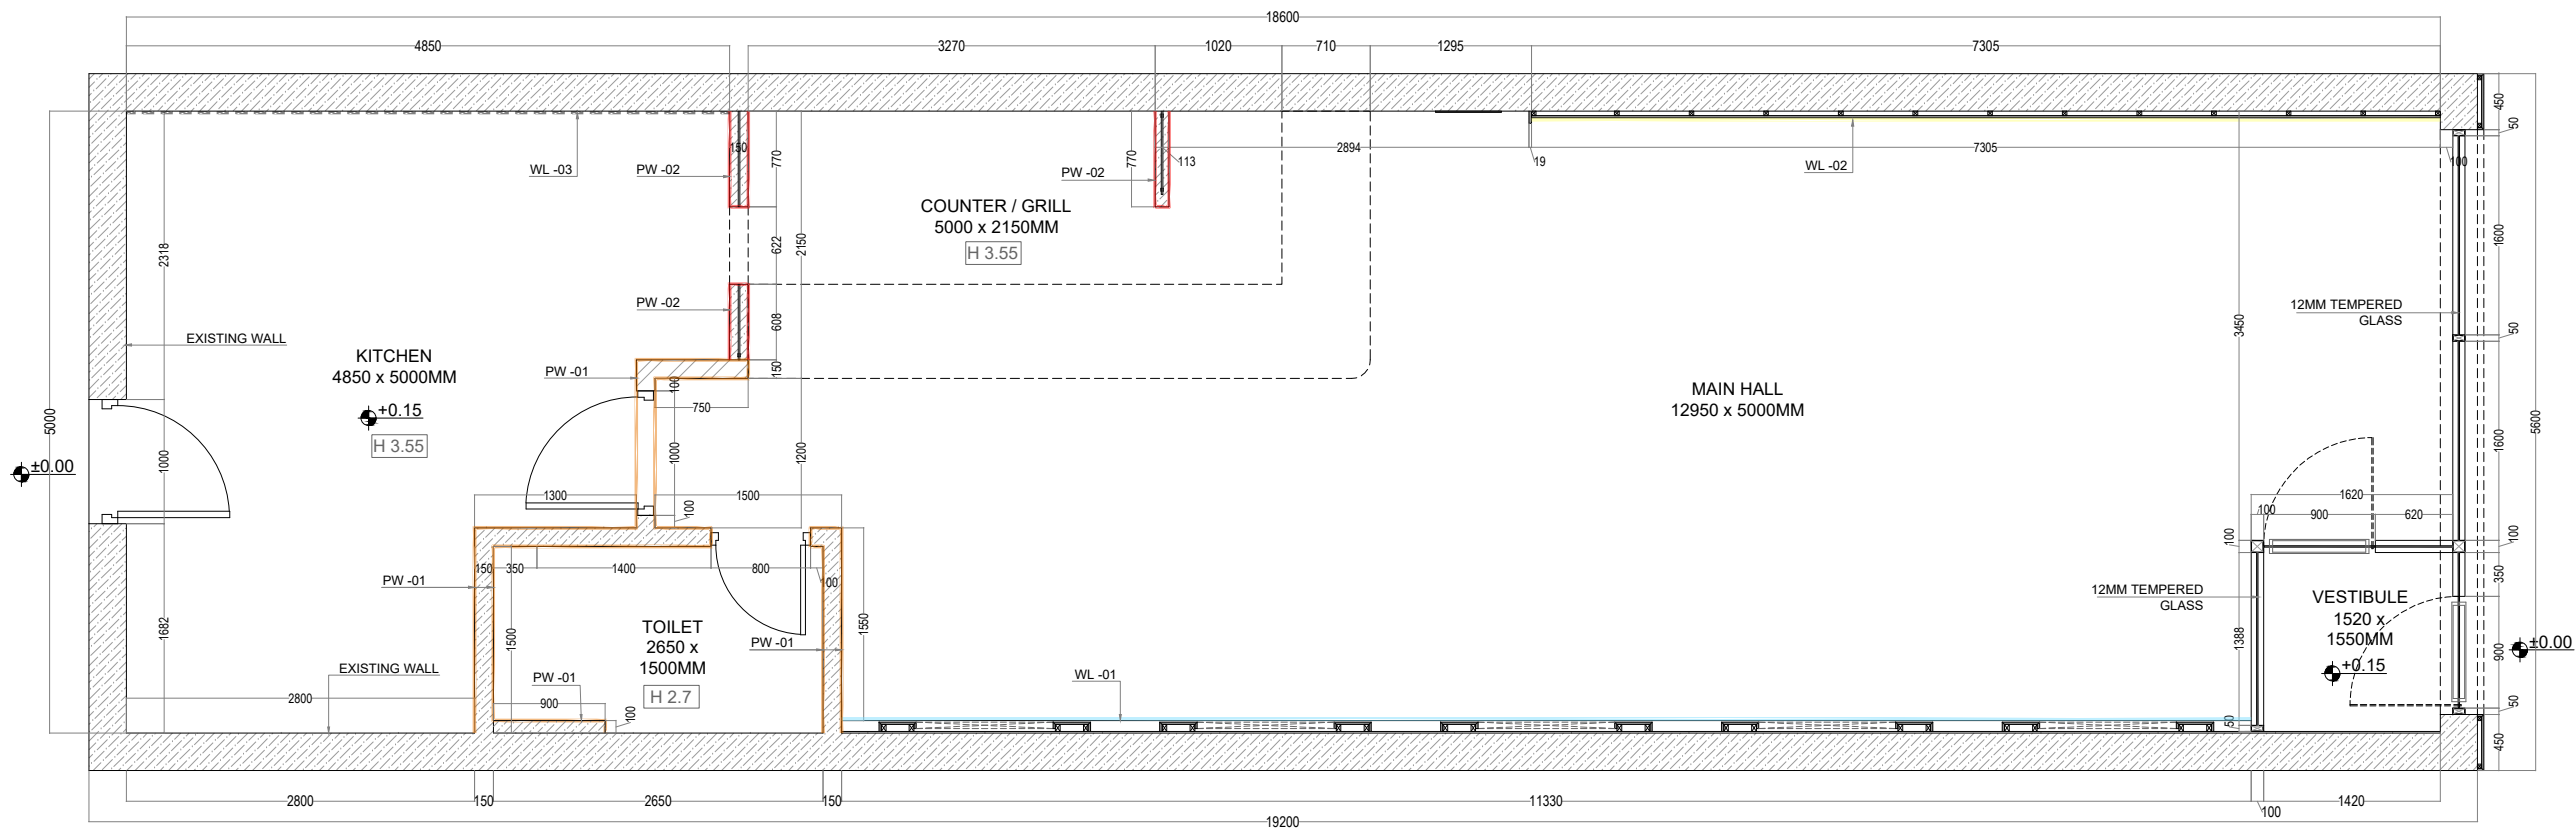

36 ARCLAY CLOSE UB8 3WP
UXBRIDGE LONDON UK
+44 743 8881857

PROJECT NAME:
TASTE OF VILLAGE

OWNER'S NAME:
TASTE OF VILLAGE

PRINCIPAL ARCHITECT;
M.S.
TITLE
GROUND FLOOR
WALL IDENTIFICATION
PLAN

CHECKED BY :
M.S.
DRAWN BY:
FAIZAN ALI

Revised Dates :
Rev. _____
Rev. _____
Rev. _____
Rev. _____
Rev. _____


SCALE:
N.T.S

DATE:
22-10-2025

JOB NO.	DRG NO.
25.1030	ID -05

NOTES:
PRESENTATION
DRAWING NOT FOR
CONSTRUCTION

HVAC	
	CEILING CASSETTE AIR CONDITION 60 X 60 CM
	AIR CURTAIN
	EXTRACT & AIR INPUT HOOD
	EXHAUST FAN 30 x 30 CM

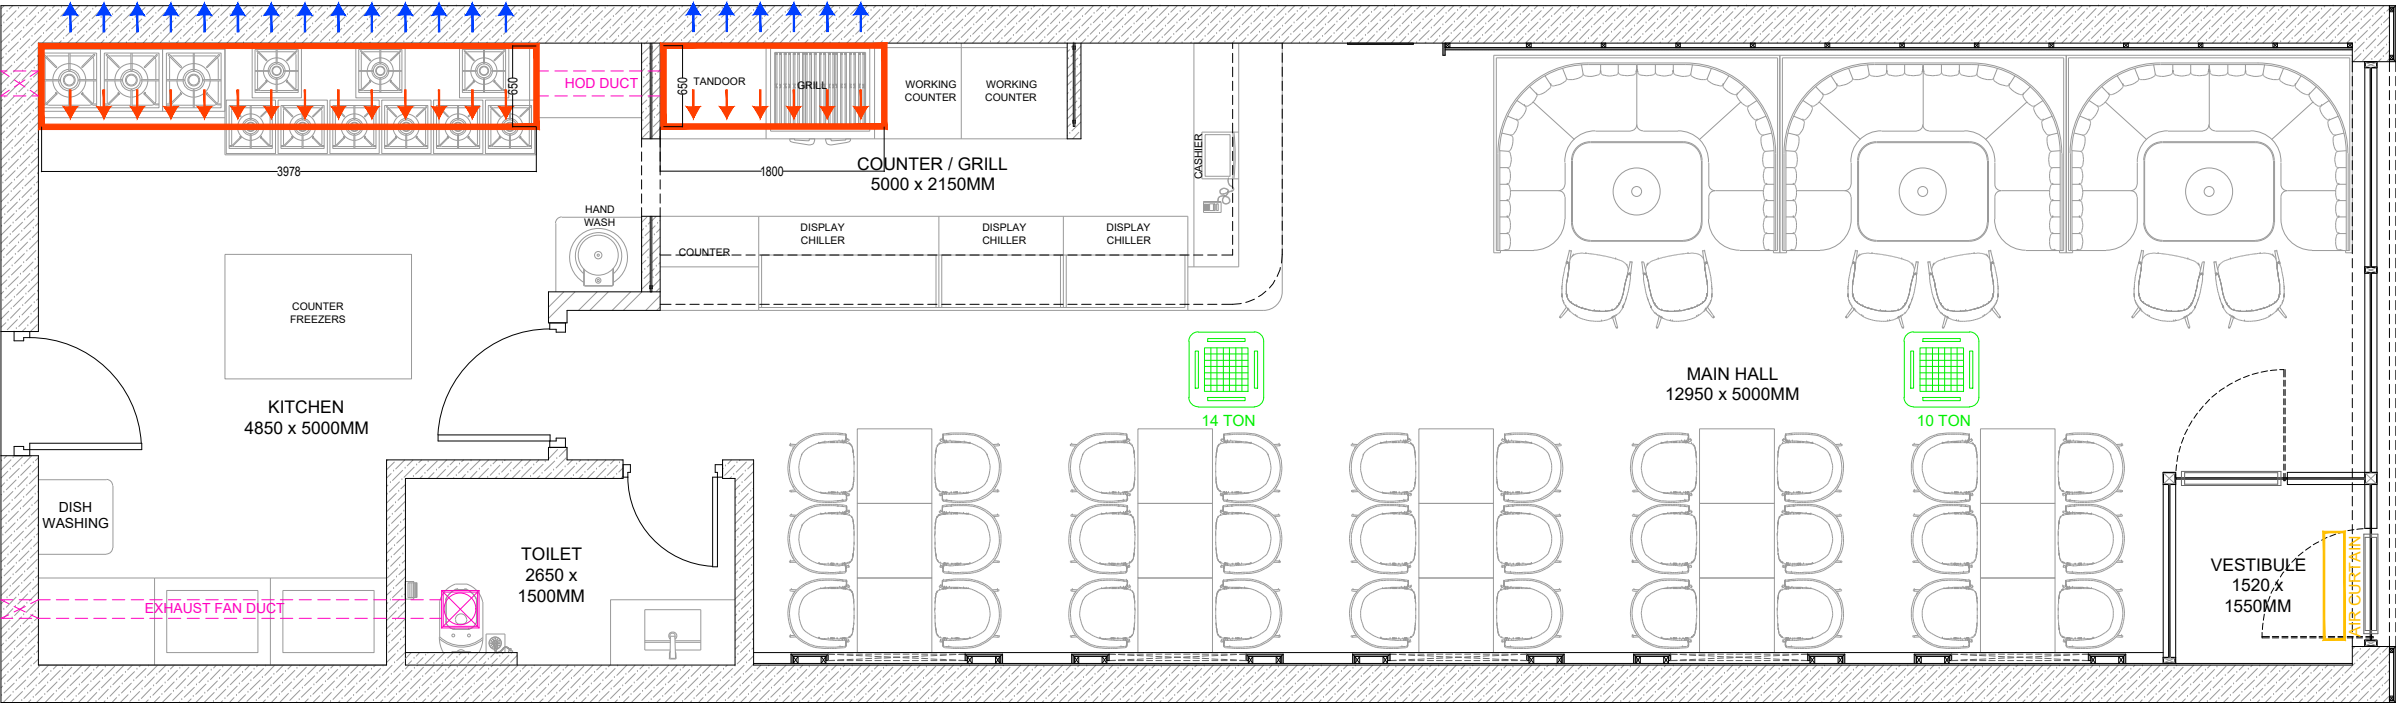

36 ARCLAY CLOSE UB8 3WP
UXBRIDGE LONDON UK
+44 743 8881857

PROJECT NAME:

TASTE OF VILLAGE

OWNER'S NAME:

TASTE OF VILLAGE

PRINCIPAL ARCHITECT;

M.S.

TITLE

GROUND FLOOR

HVAC PLAN

CHECKED BY :

M.S.

DRAWN BY:

FAIZAN ALI

Revised Dates :

Rev. _____

Rev. _____

Rev. _____

Rev. _____

SCALE:

N.T.S

DATE:

22-10-2025

JOB NO.

25.1030


DRG NO.

ID -07

NOTES:

PRESENTATION
DRAWING NOT FOR
CONSTRUCTION

ELECTRICAL ALIMENTATION	
	ELECTRICAL SWITCHBOARD
	CABLE OUTLET
	3 PIN 13A PLUG + TYPE UCB C
	3 PIN 13A PLUG
	32A 3 PHASE WATERPROOF SOCKET
	16A SINGLE PHASE WATERPROOF SOCKET
	TV
	RJ45 PLUG
	IN - CEILING SPEAKER
	FIRE EXIT SIGN

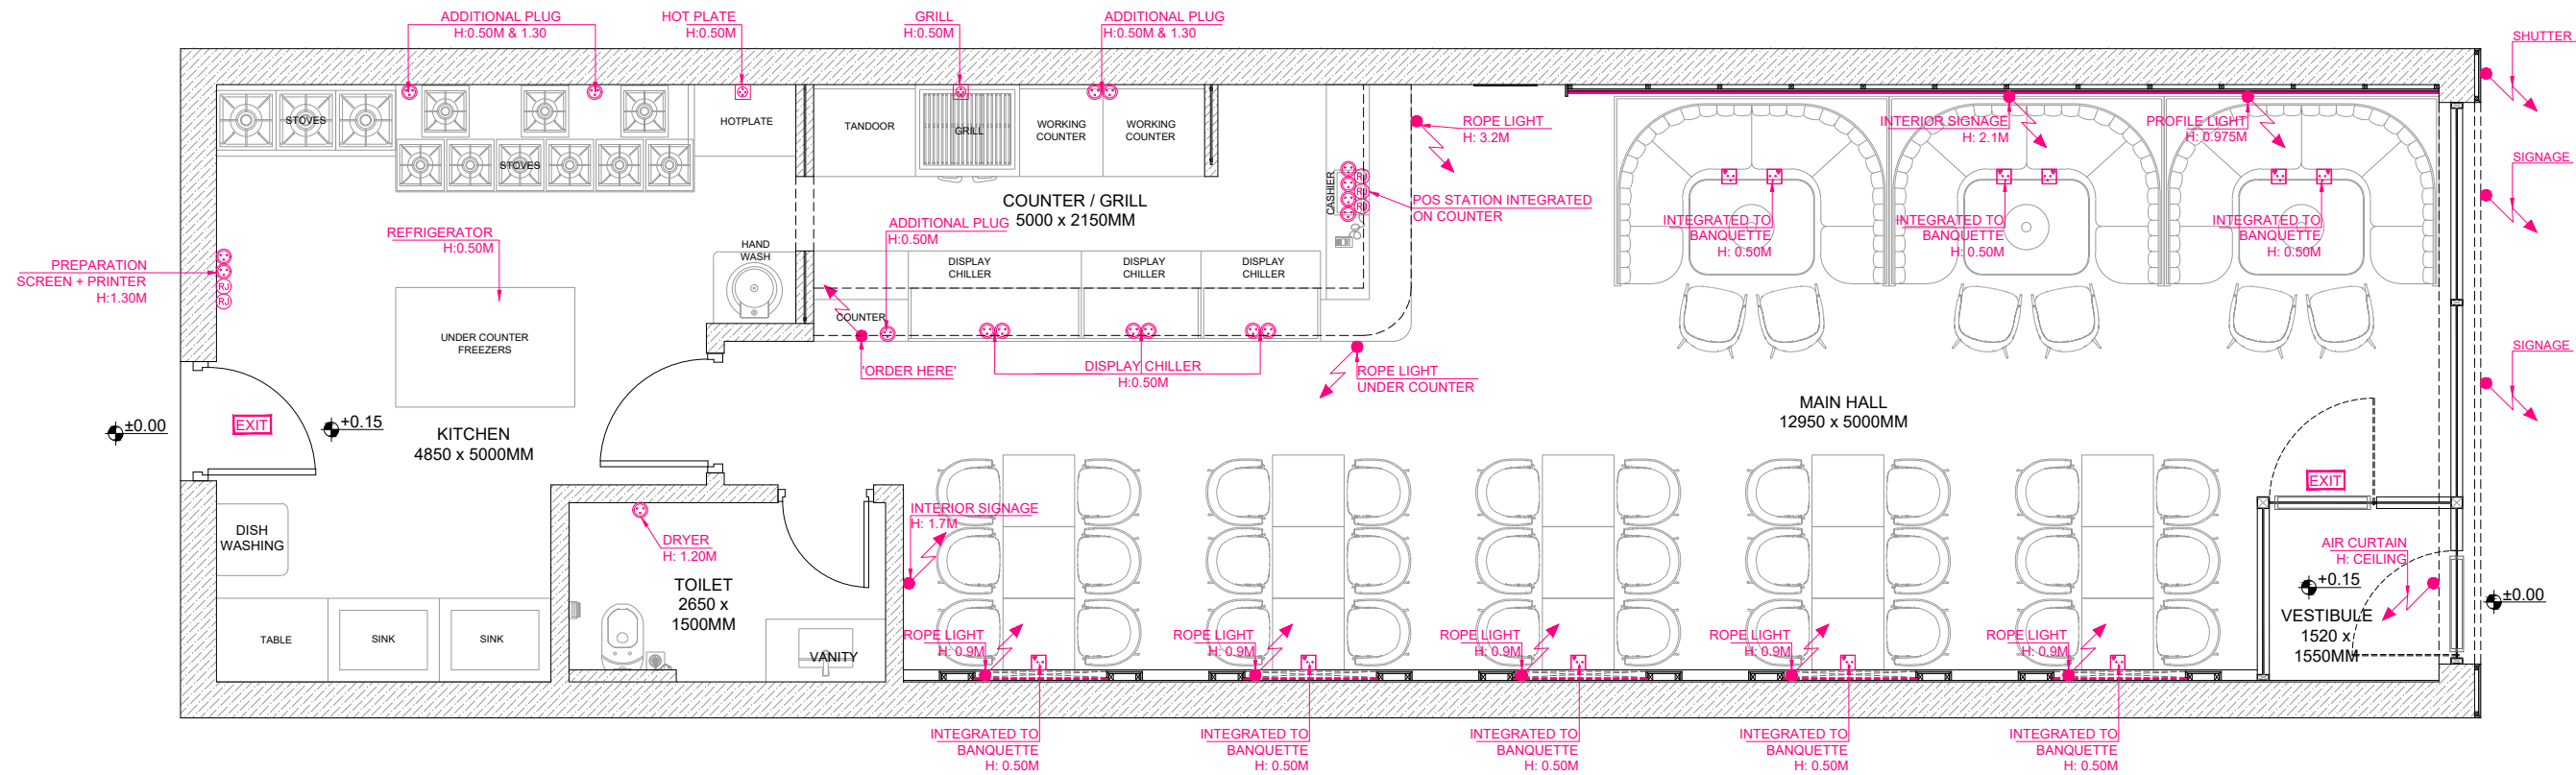

36 ARCLAY CLOSE UB8 3WP
UXBRIDGE LONDON UK
+44 743 8881857

PROJECT NAME:
TASTE OF VILLAGE

OWNER'S NAME:
TASTE OF VILLAGE

PRINCIPAL ARCHITECT;
M.S.

TITLE
GROUND FLOOR
ELECTRICAL INSTALLATION PLAN

CHECKED BY:
M.S.

DRAWN BY:
FAIZAN ALI

Revised Dates :
Rev. _____
Rev. _____
Rev. _____
Rev. _____
Rev. _____

SCALE:
N.T.S


DATE:
22-10-2025

JOB NO. 25.1030	DRG NO. ID -08
--------------------	-------------------

NOTES:

PRESENTATION
DRAWING NOT FOR
CONSTRUCTION

LIGHTING	
	PENDENT LIGHT
	ULTRA SLIM RECESSED FLAT PANEL CEILING SPOT
	LED ROPE LIGHTING / PROFILE LIGHT
	TRACK LIGHTING
	LED PANEL ULTRA SLIM 60 X 60 CM
	WATERPROOF LED LIGHTING
	BATH VANITY LIGHT
	MOTION SENSOR
	GENERAL SWITCH
	SWITCH 1 POLE
	SPEAKER
	FLY KILLER

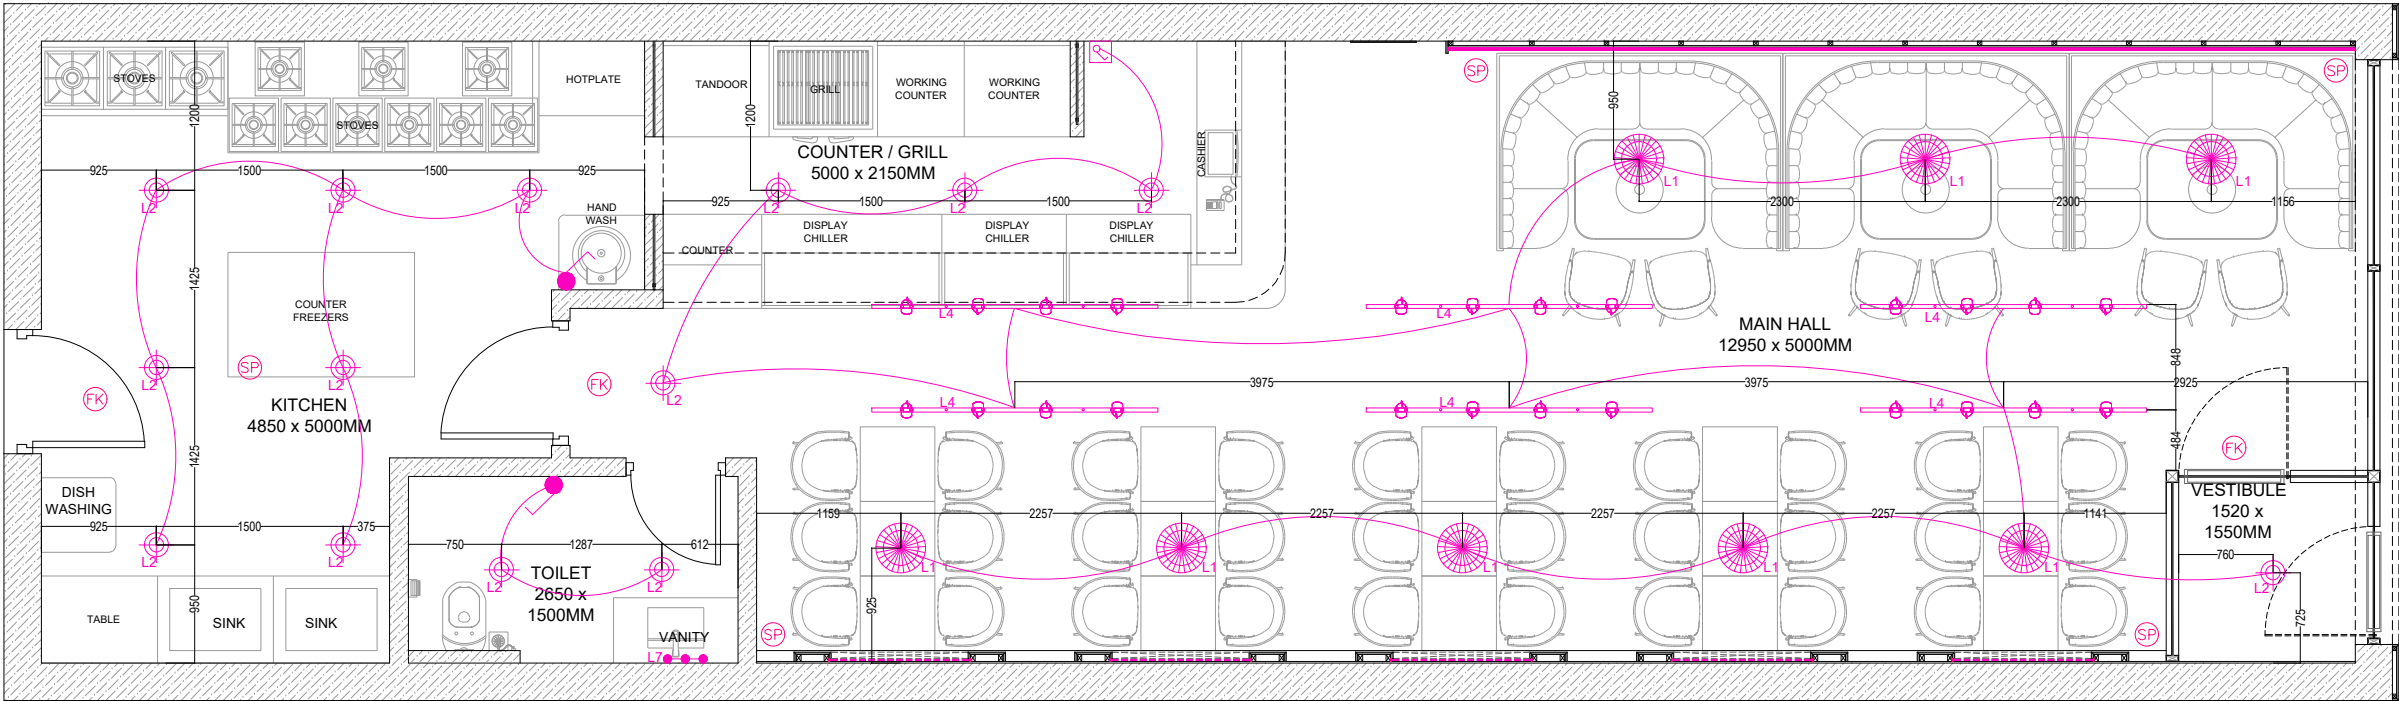

36 ARCLAY CLOSE UB8 3WP
UXBRIDGE LONDON UK
+44 743 8881857

PROJECT NAME:

TASTE OF VILLAGE

OWNER'S NAME:

TASTE OF VILLAGE

PRINCIPAL ARCHITECT;

M.S.

TITLE

GROUND FLOOR
LIGHTING PLAN

CHECKED BY :

M.S.

DRAWN BY:

FAIZAN ALI

Revised Dates :

Rev. _____

Rev. _____

Rev. _____

Rev. _____

SCALE:

N.T.S

DATE:

22-10-2025

JOB NO.

25.1030


DRG NO.

ID -09

NOTES:

PRESENTATION
DRAWING NOT FOR
CONSTRUCTION

LIGHTING	
	PENDENT LIGHT
	ULTRA SLIM RECESSED FLAT PANEL CEILING SPOT
	LED ROPE LIGHTING / PROFILE LIGHT
	TRACK LIGHTING
	LED PANEL ULTRA SLIM 60 X 60 CM
	WATERPROOF LED LIGHTING
	BATH VANITY LIGHT
	MOTION SENSOR
	GENERAL SWITCH
	SWITCH 1 POLE
	SPEAKER
	FLY KILLER

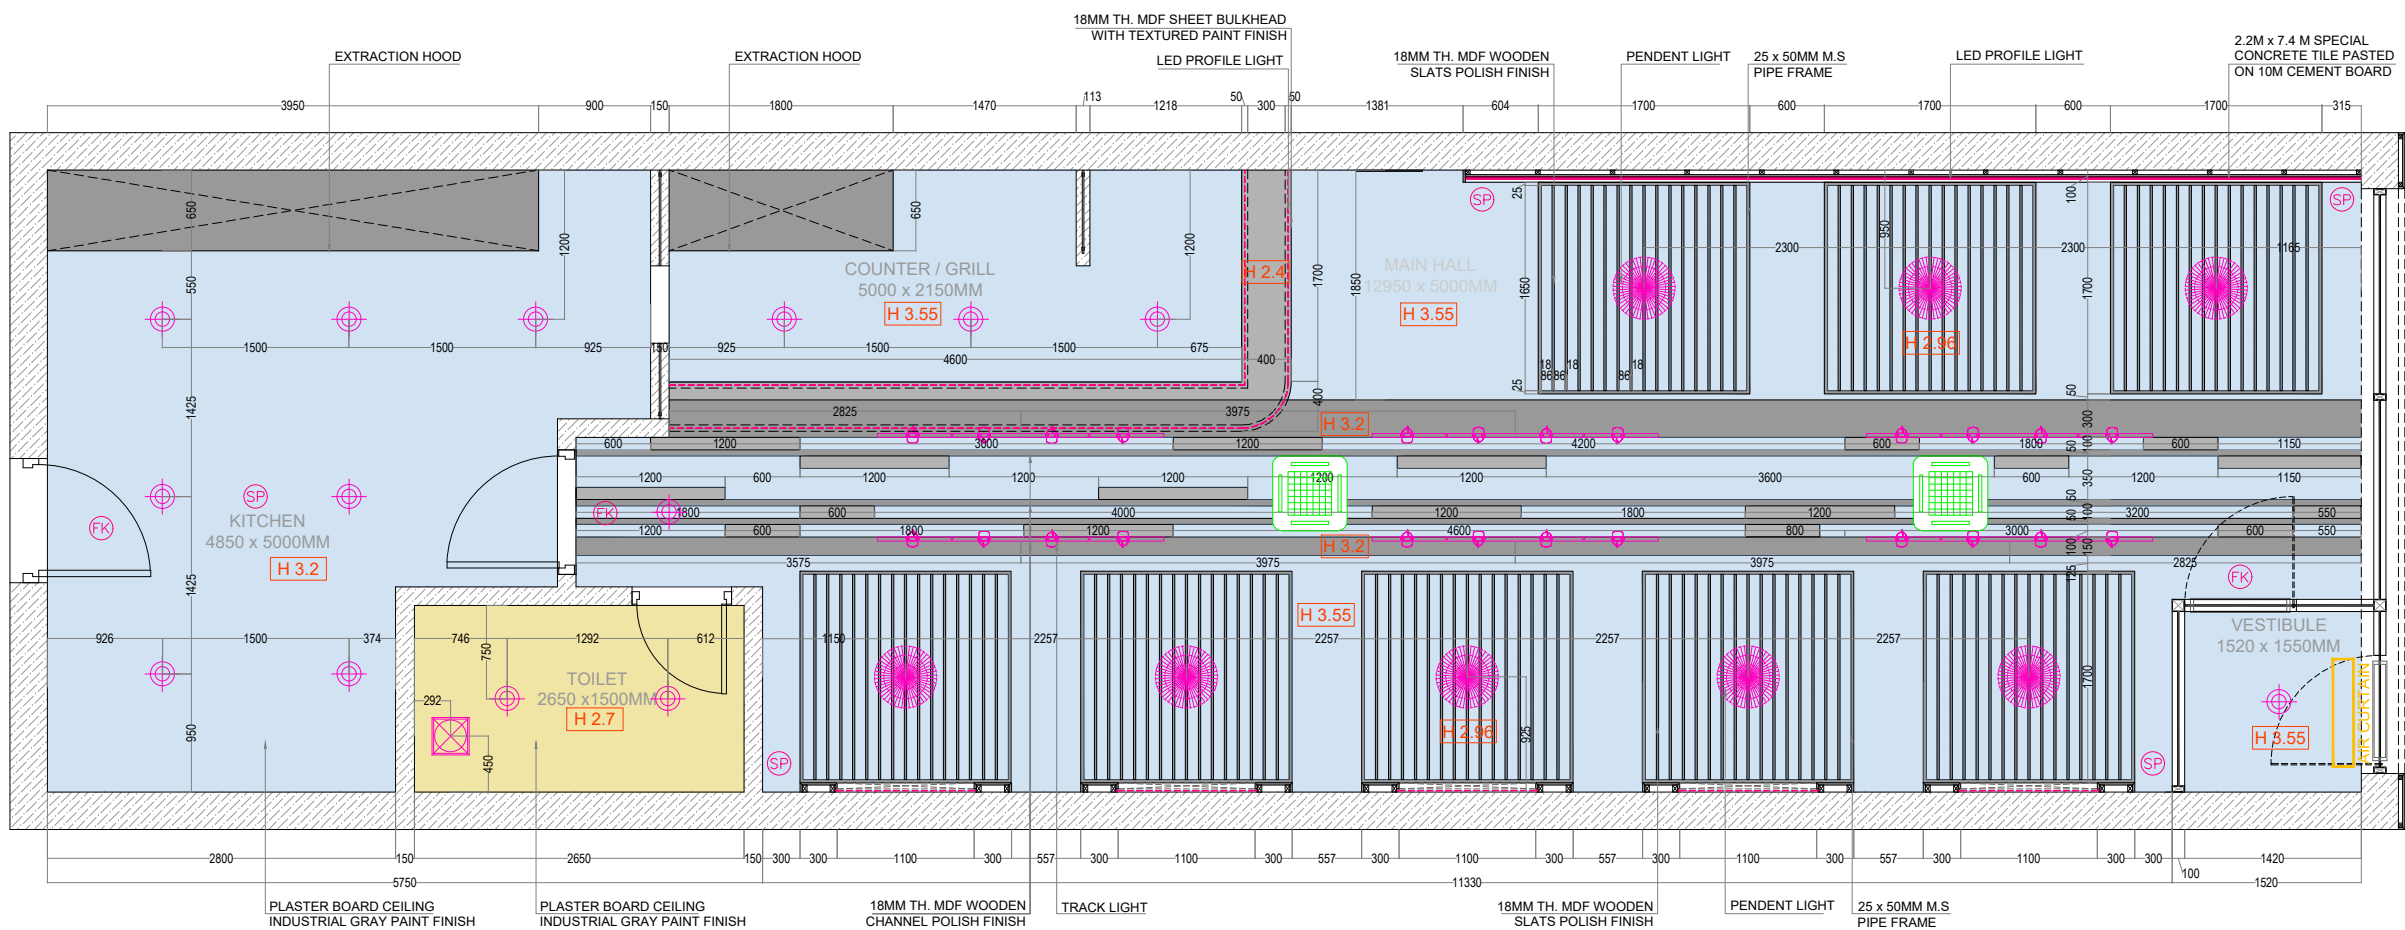

36 ARCLAY CLOSE UB8 3WP
UXBRIDGE LONDON UK

+44 743 8881857

PROJECT NAME:

TASTE OF VILLAGE

OWNER'S NAME:

TASTE OF VILLAGE

PRINCIPAL ARCHITECT;

M.S.

TITLE

GROUND FLOOR
CEILING PLAN

CHECKED BY :

M.S.

DRAWN BY:

FAIZAN ALI

Revised Dates :

Rev. _____

Rev. _____

Rev. _____

Rev. _____

Rev. _____

SCALE:

N.T.S

DATE:

18-10-2025

JOB NO.


25.1030

DRG NO.


ID -10

NOTES:


PRESENTATION
DRAWING NOT FOR
CONSTRUCTION

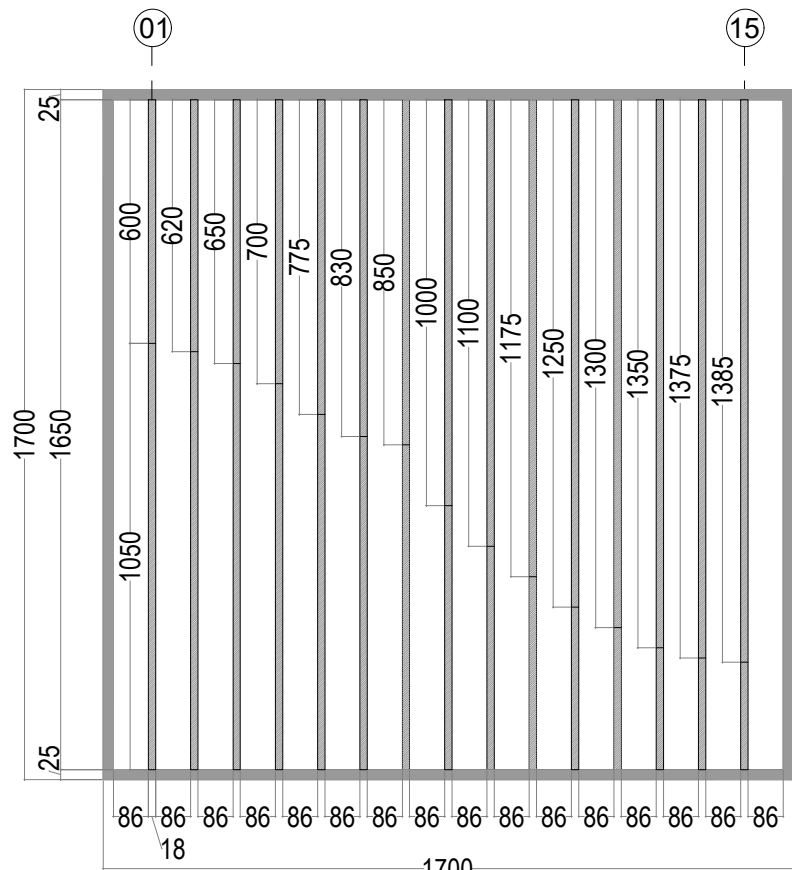

CEILING WOODEN
PANEL PLAN

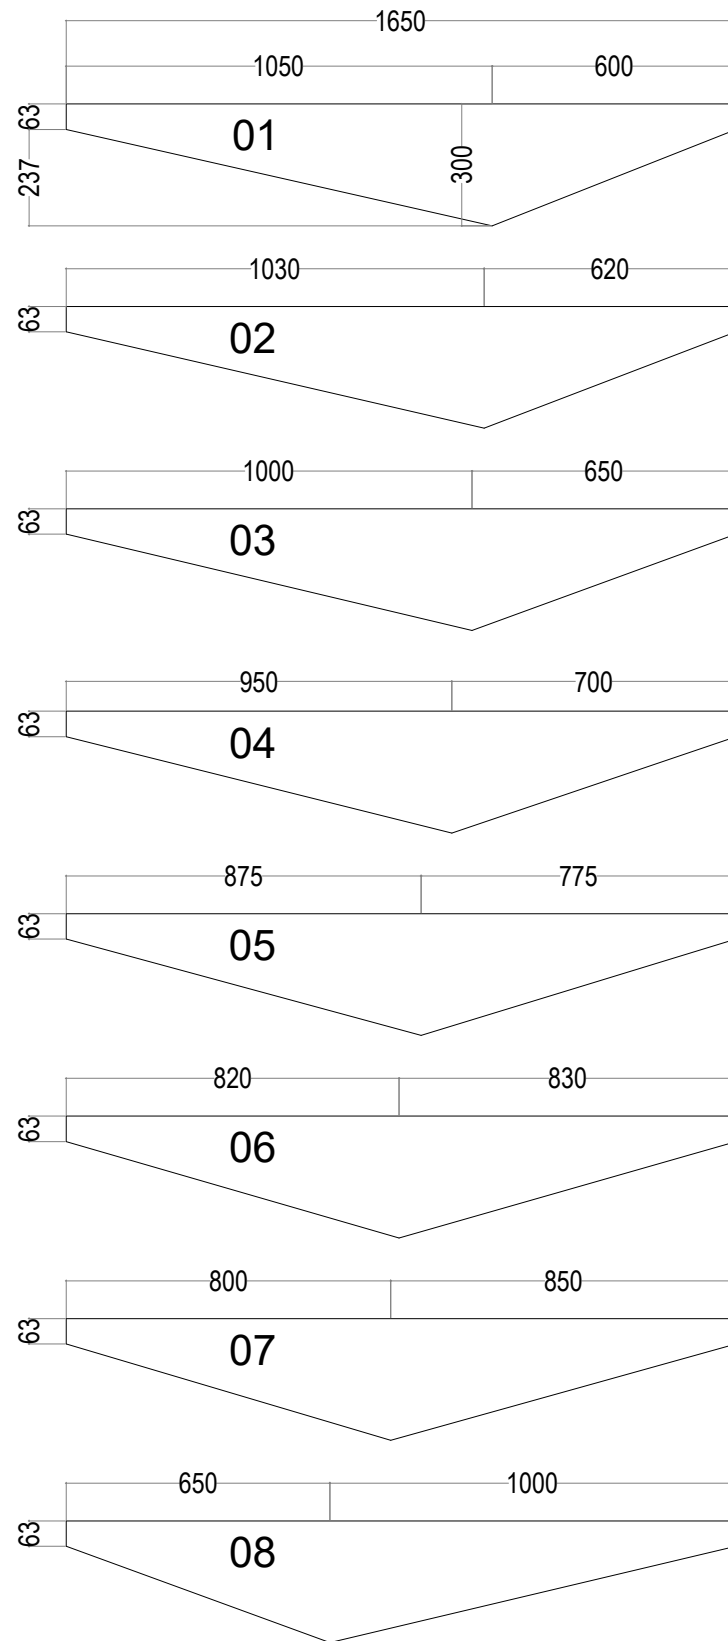

CEILING WOODEN
RAFTER ELEVATION

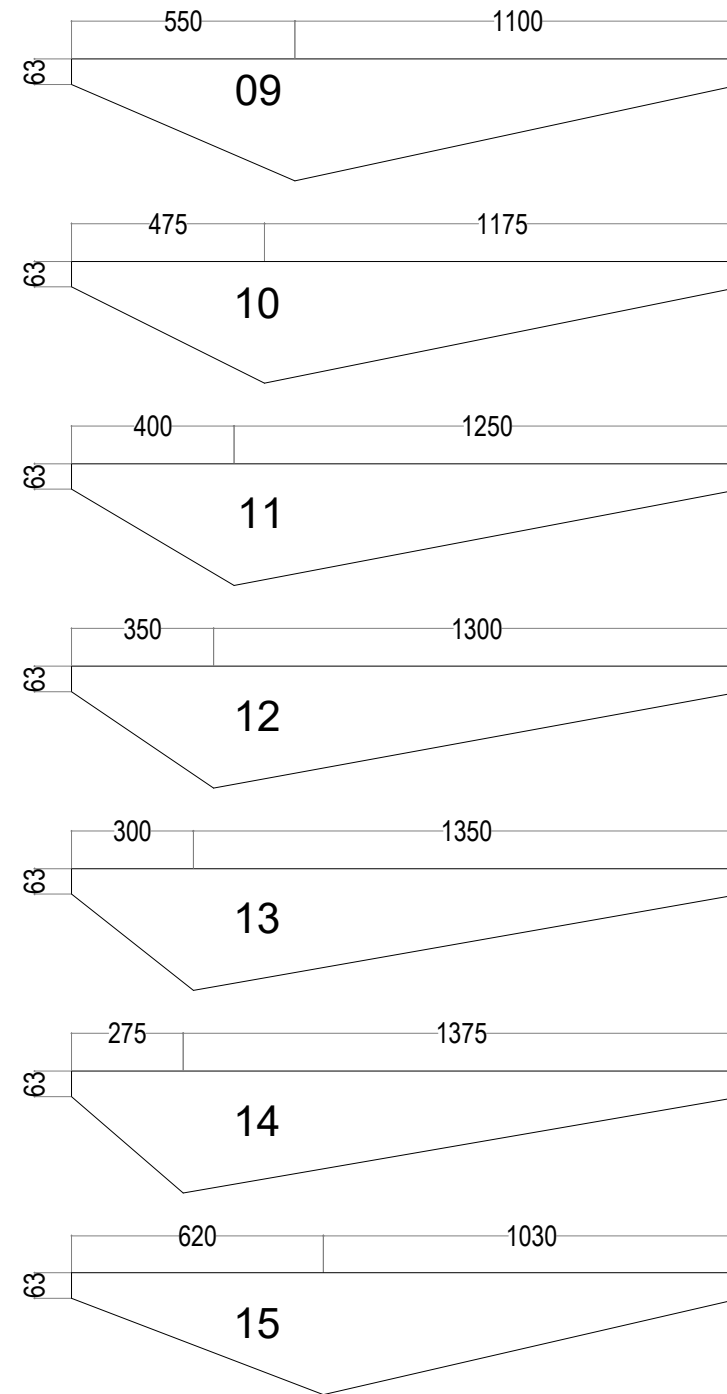

36 ARCLAY CLOSE UB8 3WP
UXBRIDGE LONDON UK

+44 743 8881857

PROJECT NAME:

TASTE OF VILLAGE

OWNER'S NAME:

TASTE OF VILLAGE

PRINCIPAL ARCHITECT;

M.S.

TITLE

GROUND FLOOR
CEILING PANEL DETAIL

CHECKED BY :

M.S.

DRAWN BY:

FAIZAN ALI

Revised Dates :

Rev. _____

Rev. _____

Rev. _____

Rev. _____

Rev. _____

SCALE:

N.T.S

DATE:

18-10-2025

JOB NO.

25.1030


DRG NO.

ID -11

NOTES:

PRESENTATION
DRAWING NOT FOR
CONSTRUCTION

FLOOR FINISHING		
F-01	PRINTED DOOR MAT	2.3 SQM
F-02	VOLTE BEECH WOVEN WOOD EFFECT MATT PORCELAIN FLOOR TILE (90 x 90CM)	18 SQM
F-03	DISCOTHEQUE TOYAH TILE (19.8 x 19.8CM)	50 SQM
F-04	EPOXY FLOOR	20 SQM
F-05	TRANSITION PROFILE - ALUMINUM	25.3 M
F-06	STONE / TILE SKIRTING	22.2 M

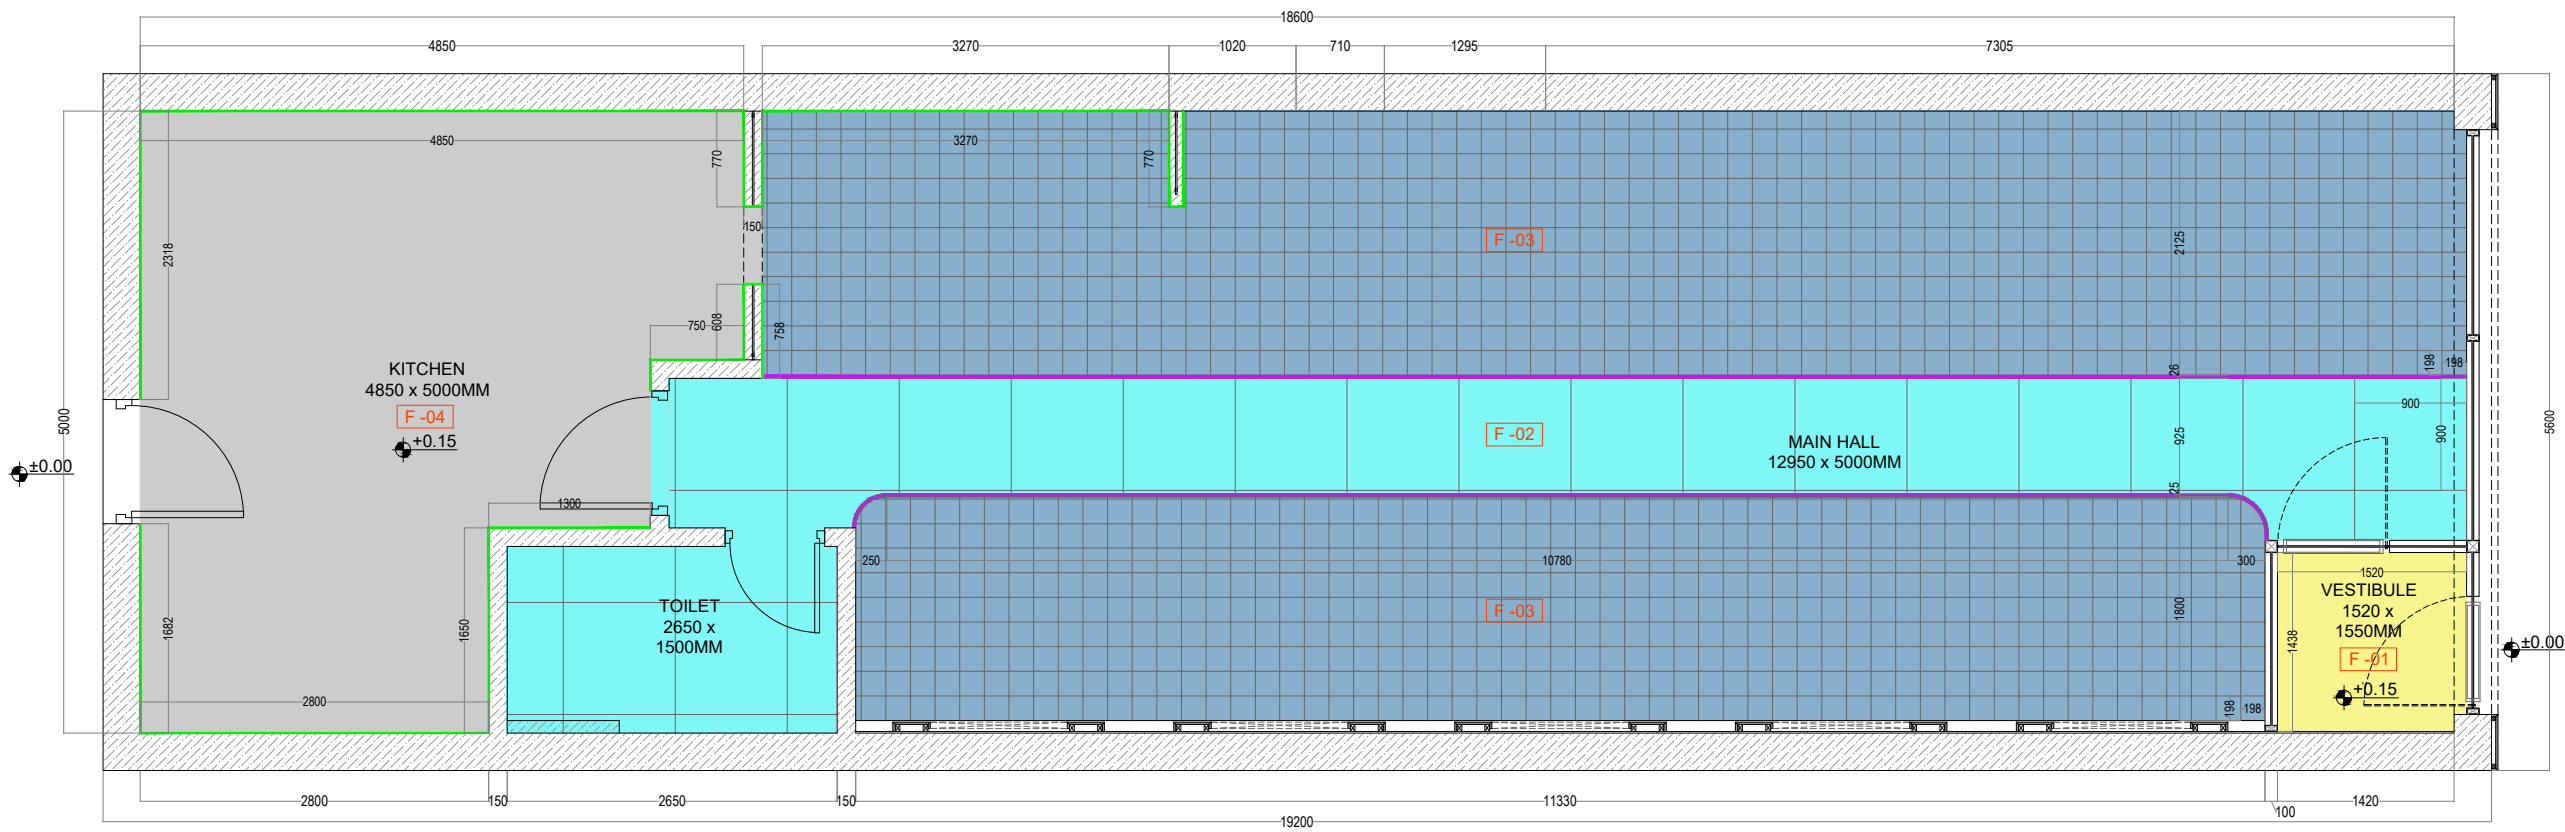

36 ARCLAY CLOSE UB8 3WP
UXBRIDGE LONDON UK
+44 743 8881857

PROJECT NAME:
TASTE OF VILLAGE

OWNER'S NAME:
TASTE OF VILLAGE

PRINCIPAL ARCHITECT;
M.S.
TITLE
GROUND FLOOR
FLOOR FINISHING PLAN

CHECKED BY :
M.S.

DRAWN BY:
FAIZAN ALI

Revised Dates :
Rev. _____
Rev. _____
Rev. _____
Rev. _____
Rev. _____


SCALE:
N.T.S

DATE:
22-10-2025

JOB NO.	DRG NO.
25.1030	ID -12

NOTES:
PRESENTATION
DRAWING NOT FOR
CONSTRUCTION

WALL FINISHING	
WF-01	18MM TH. PLASTER BOARD SHEET + SKIMMING WITH ULTRA MAT TEXTURED PAINT FINISH (ARCH WALL MAIN BATH OUTER WALL)
WF-02	TERRACOTA ULTRA MAT PLASTER BOARD SHEET + SKIMMING WITH PAINT FINISH ARCH BACK WALL
WF-03	20 x 10 CM METRO FOREST TILE (ARCH BOTTOM WALL)
WF-04	STAINLESS STEEL WALL PANEL ON 18MM TH. PLASTER BOARD SHEET + SKIMMING (KITCHEN WALLS)
WF-05	MDF SHEET CNC CUTTING WITH TEXTURED PAINT FINISH

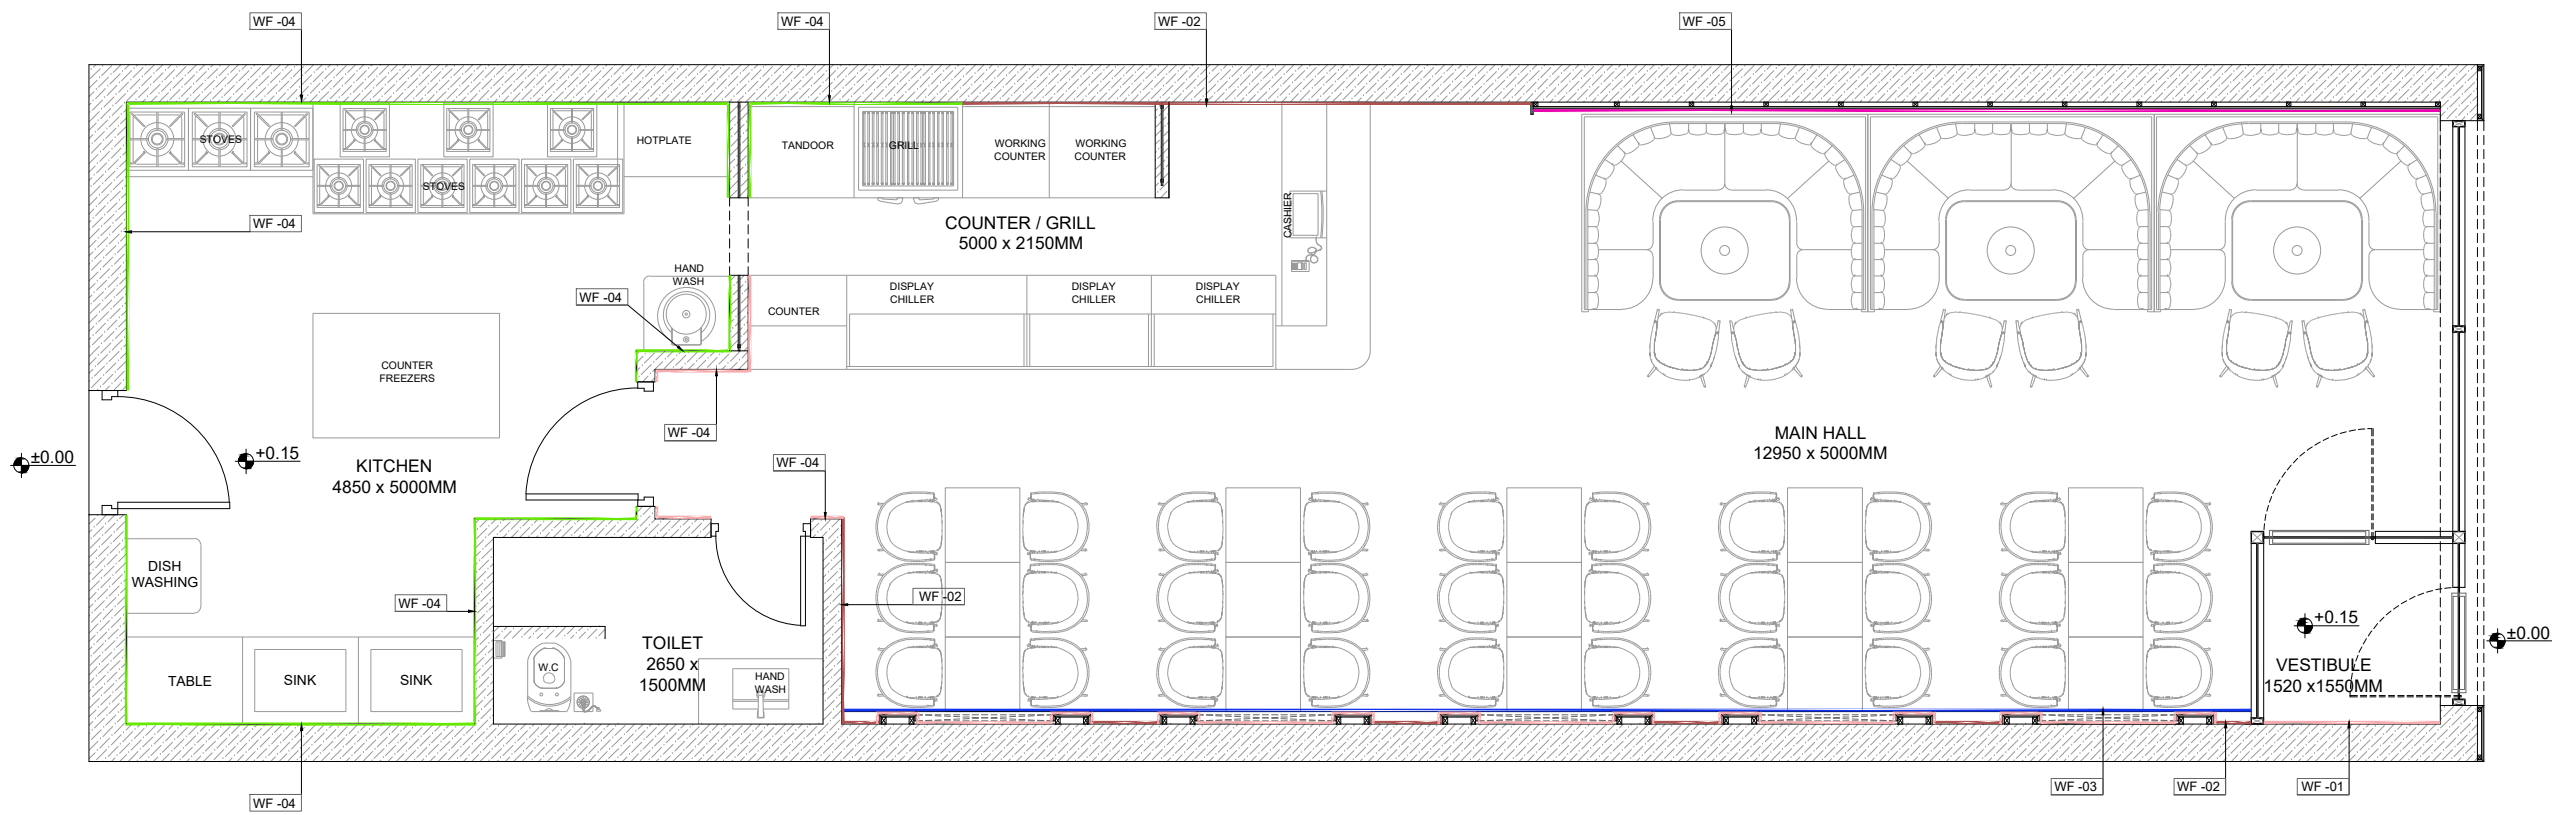

36 ARCLAY CLOSE UB8 3WP
UXBRIDGE LONDON UK

+44 743 8881857

PROJECT NAME:

TASTE OF VILLAGE

OWNER'S NAME:

TASTE OF VILLAGE

PRINCIPAL ARCHITECT;

M.S.

TITLE

GROUND FLOOR
WALL FINISHING PLAN

CHECKED BY :

M.S.

DRAWN BY:

FAIZAN ALI

Revised Dates :

Rev. _____

Rev. _____

Rev. _____

Rev. _____

Rev. _____

SCALE:

N.T.S

DATE:

22-10-2025

JOB NO.


25.1030

DRG NO.


ID -13

NOTES:

PRESENTATION
DRAWING NOT FOR
CONSTRUCTION

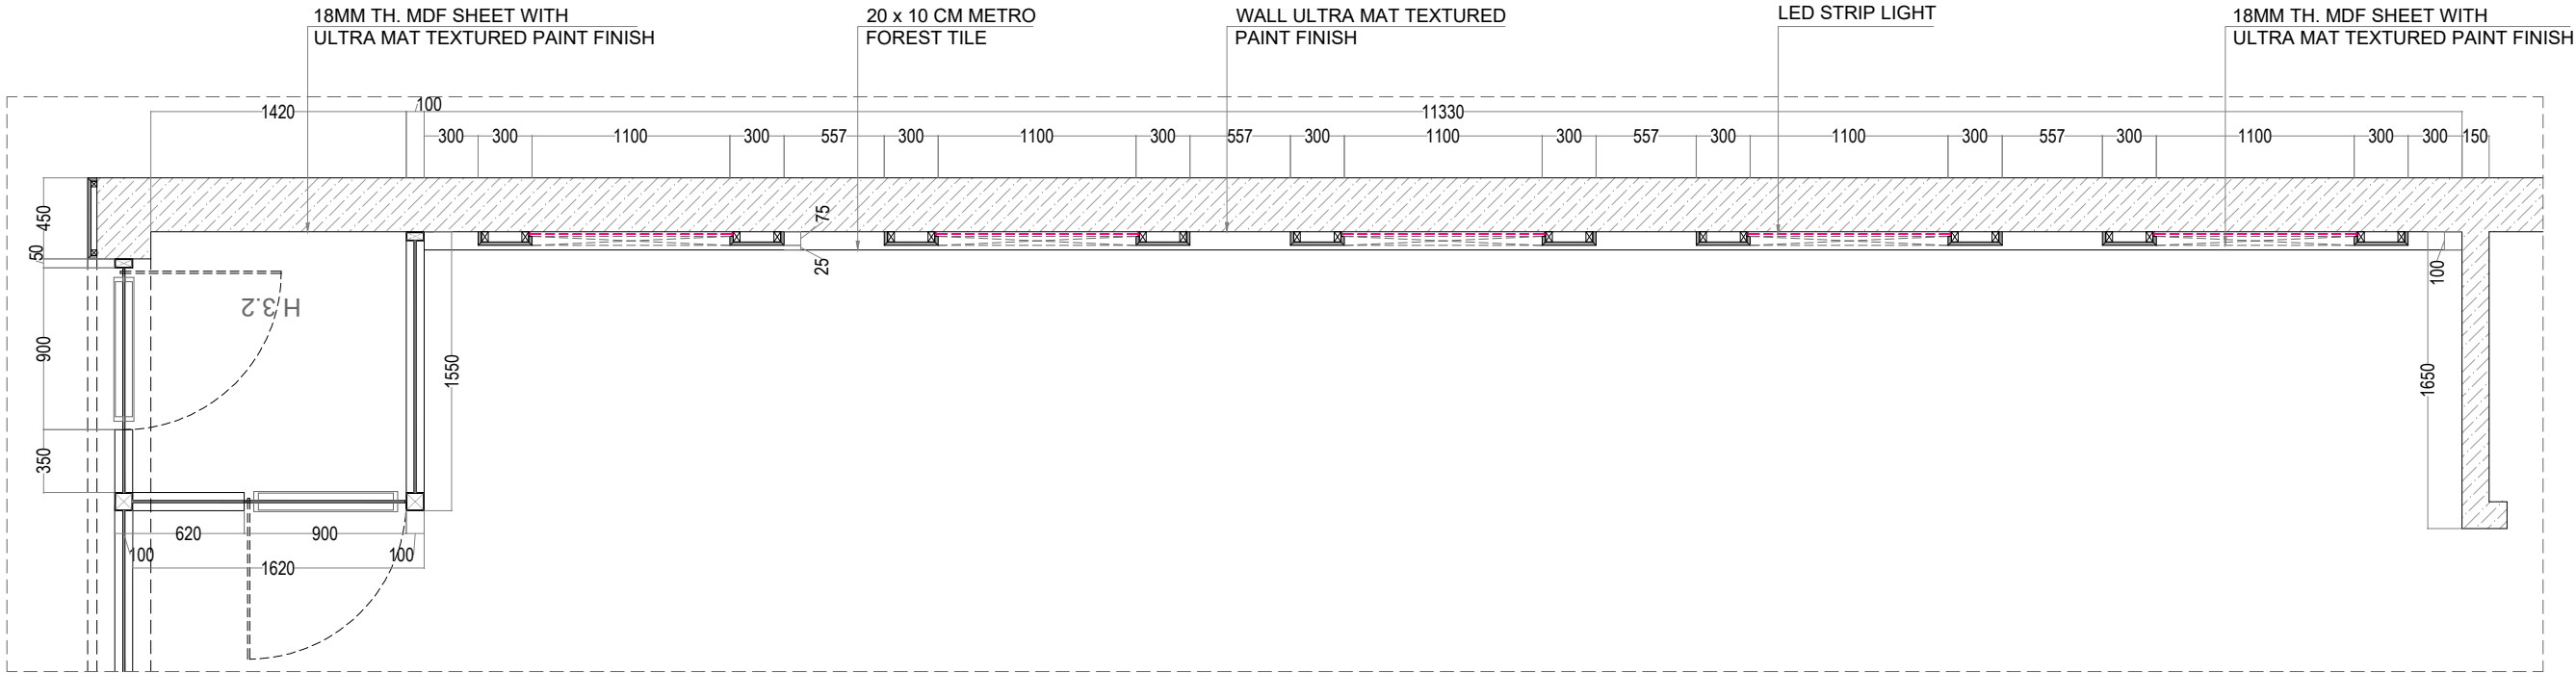

ARCH FEATURE WALL PLAN

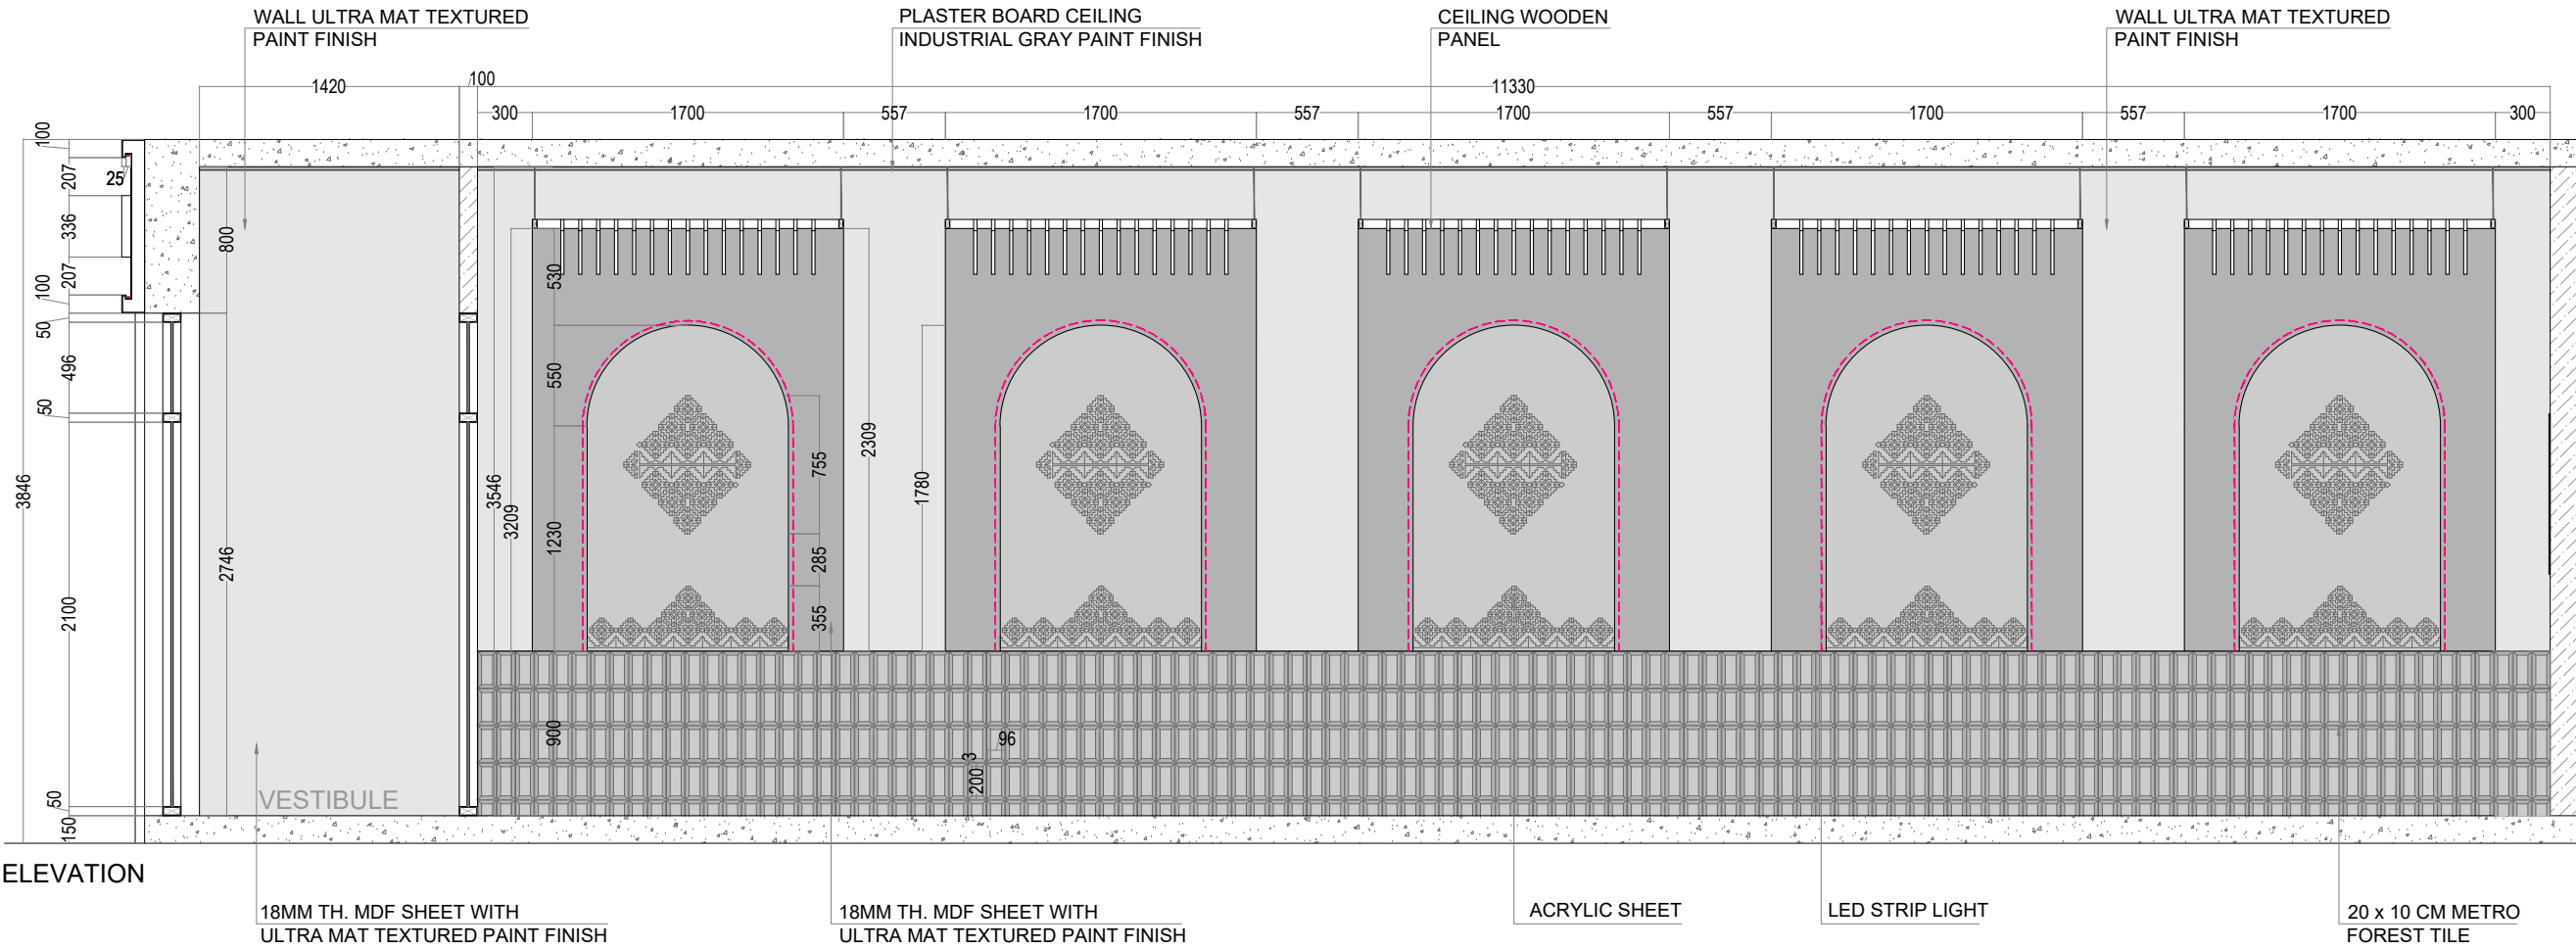

ELEVATION



36 ARCLAY CLOSE UB8 3WP
UXBRIDGE LONDON UK
+44 743 8881857

PROJECT NAME:

TASTE OF VILLAGE

OWNER'S NAME:

TASTE OF VILLAGE

PRINCIPAL ARCHITECT;

M.S.

TITLE

ARCH FEATURE WALL
ELEVATION -01

CHECKED BY:

M.S.

DRAWN BY:

FAIZAN ALI

Revised Dates:

Rev.

Rev.

Rev.

Rev.

Rev.

Rev.

SCALE:

N.T.S

DATE:

18-10-2025

JOB NO.


25.1030

DRG NO.

ID -14

NOTES:

PRESENTATION
DRAWING NOT FOR
CONSTRUCTION

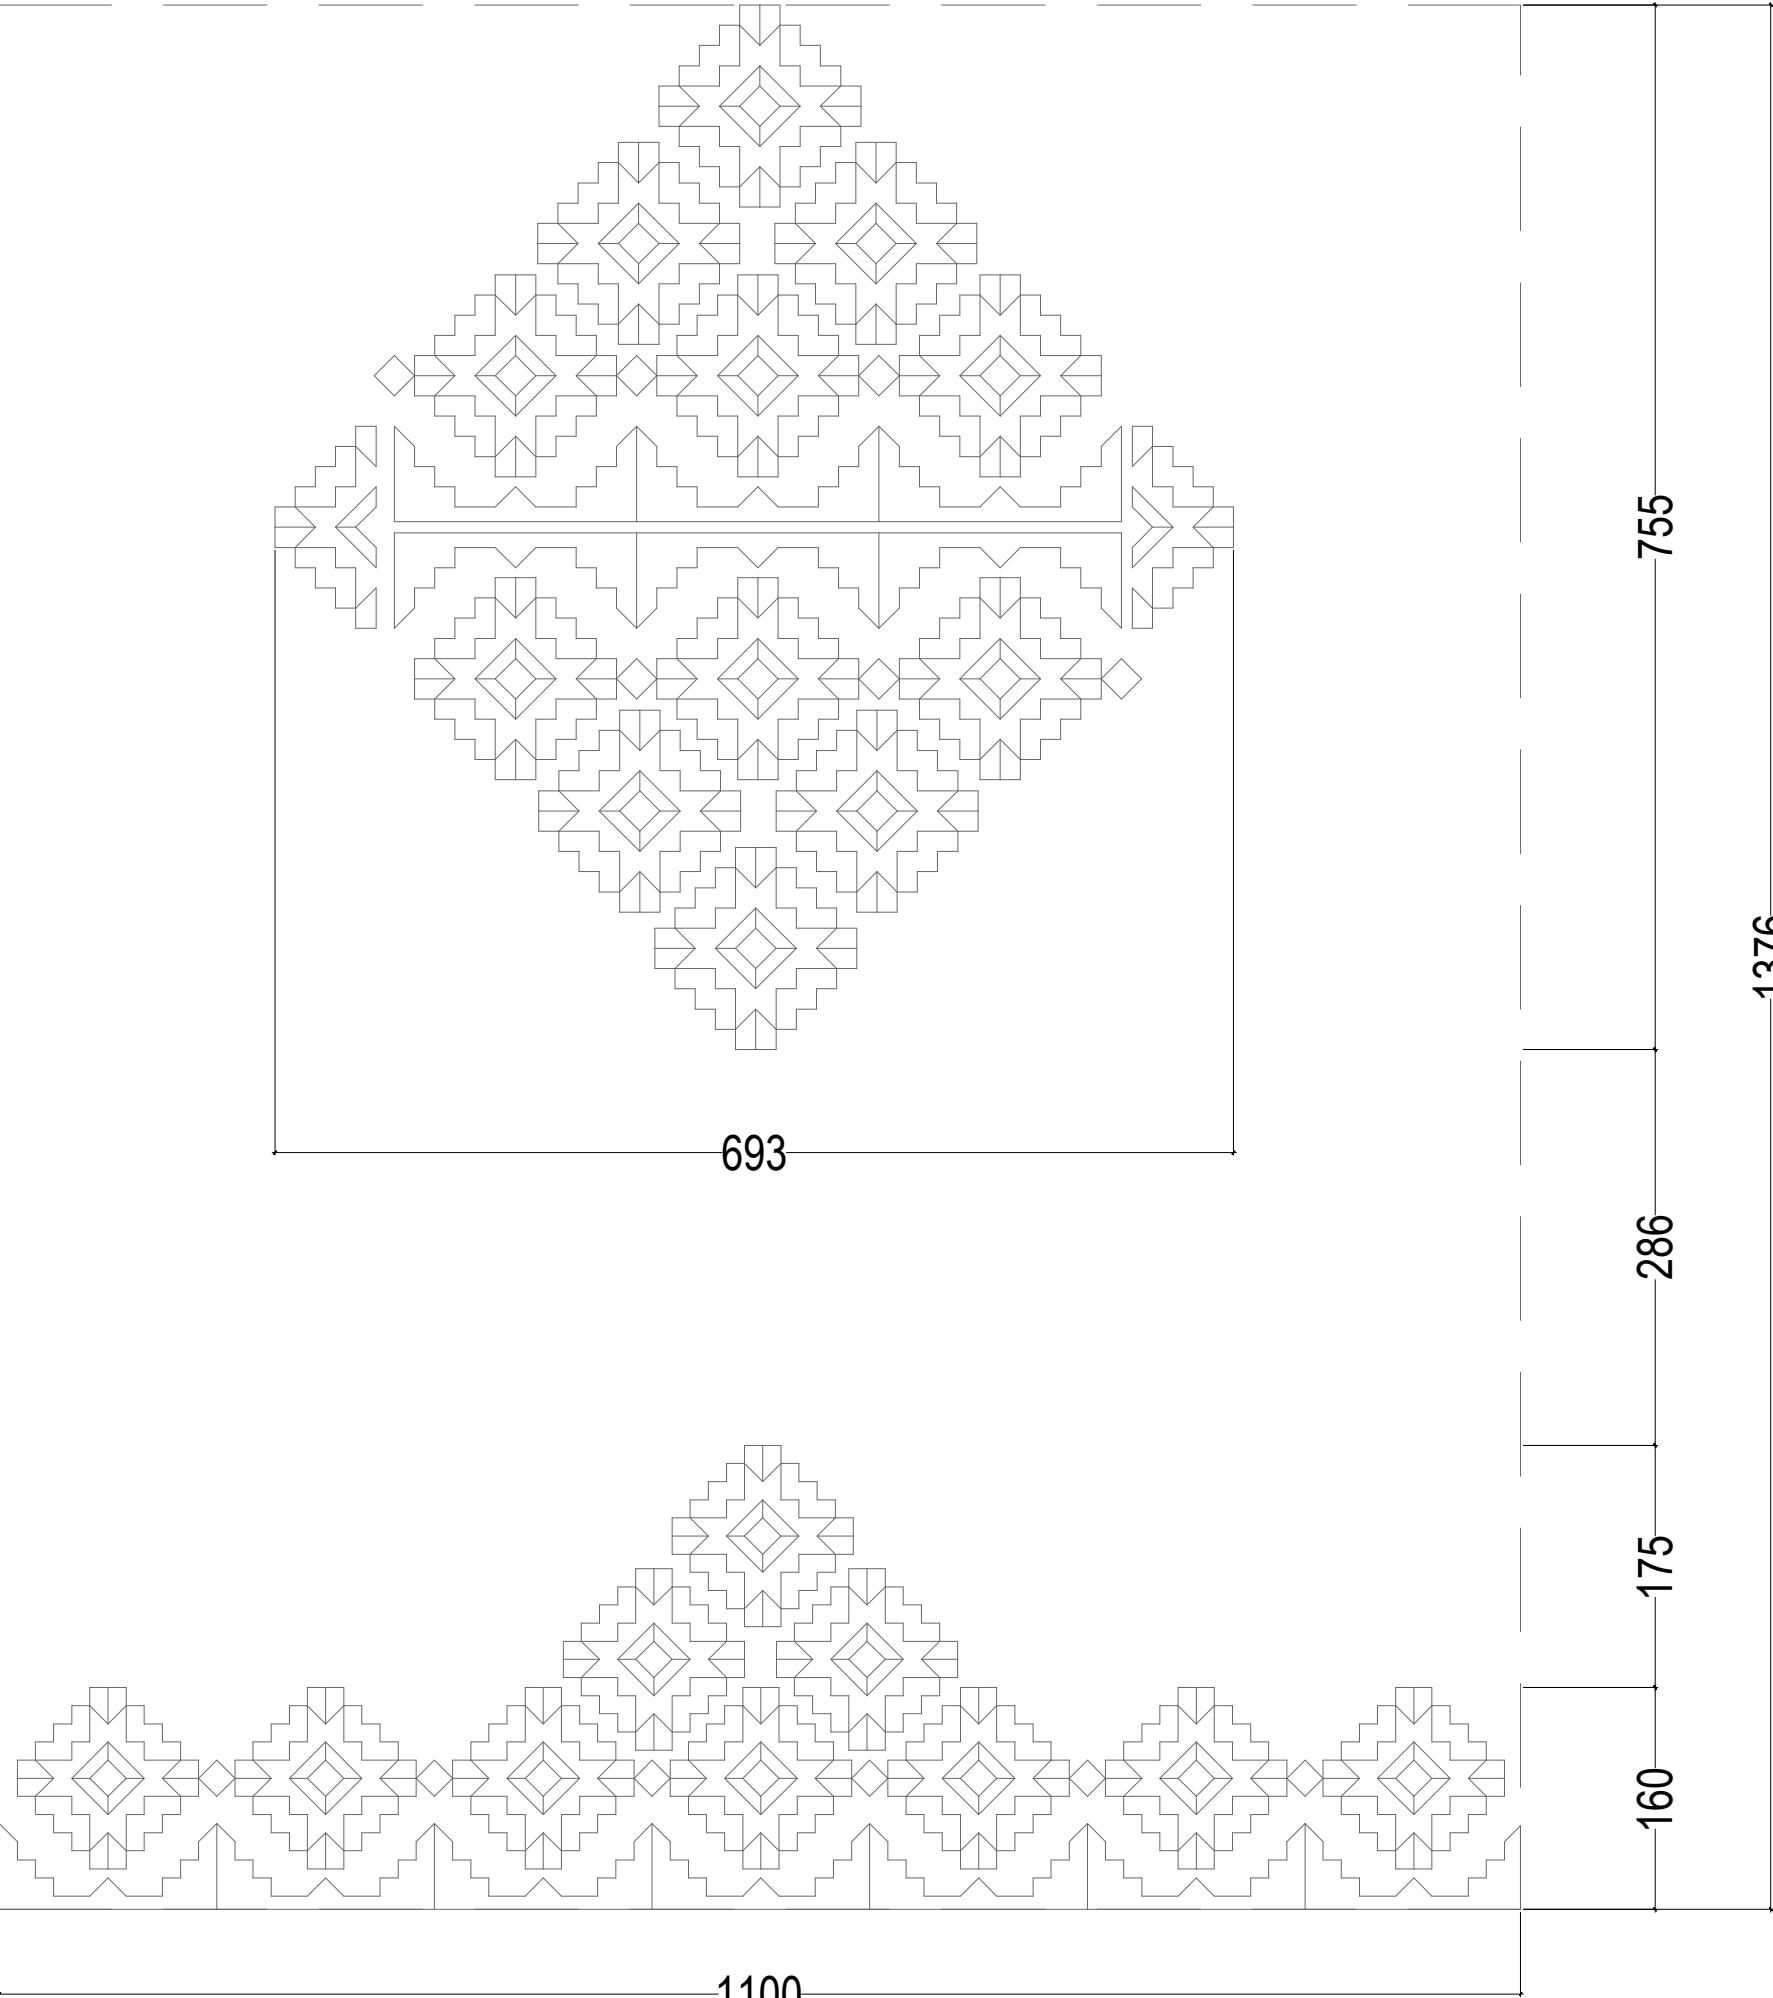

36 ARCLAY CLOSE UB8 3WP
UXBRIDGE LONDON UK
+44 743 8881857

PROJECT NAME:
TASTE OF VILLAGE

OWNER'S NAME:
TASTE OF VILLAGE

PRINCIPAL ARCHITECT;
M.S.

TITLE
ARCH FEATURE WALL
CNC CUTTING BLOWUP DETAIL

CHECKED BY :
M.S.

DRAWN BY:
FAIZAN ALI

Revised Dates :
Rev.....
Rev.....
Rev.....
Rev.....
Rev.....


SCALE:
N.T.S

DATE:
18-10-2025


JOB NO.
25.1030

DRG NO.
ID -15


NOTES:
PRESENTATION
DRAWING NOT FOR
CONSTRUCTION

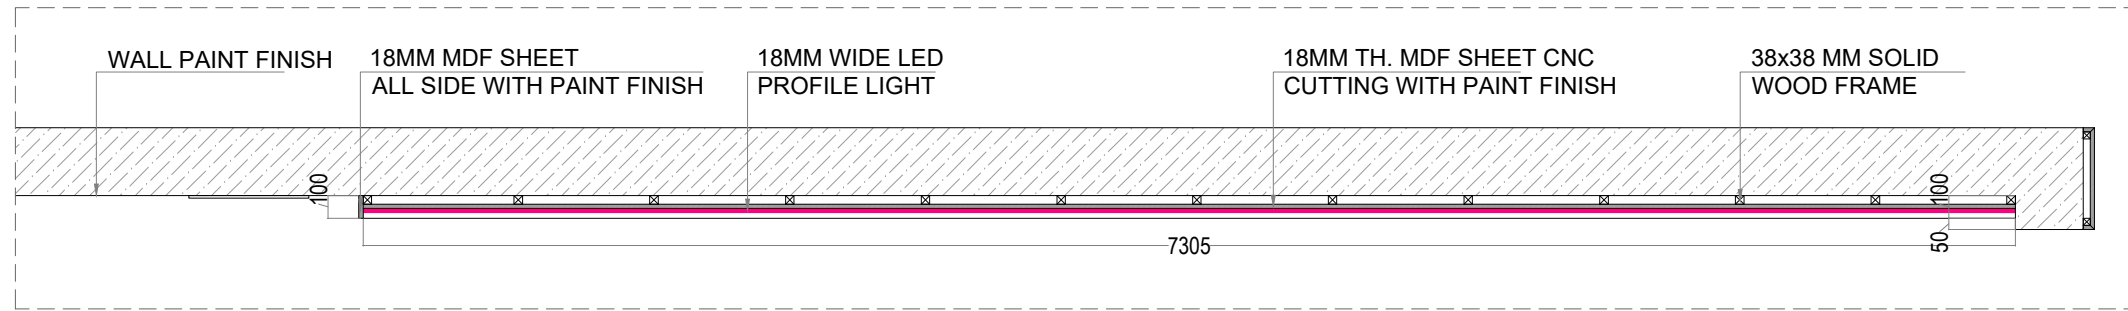

CNC CUTTING FEATURE WALL PLAN

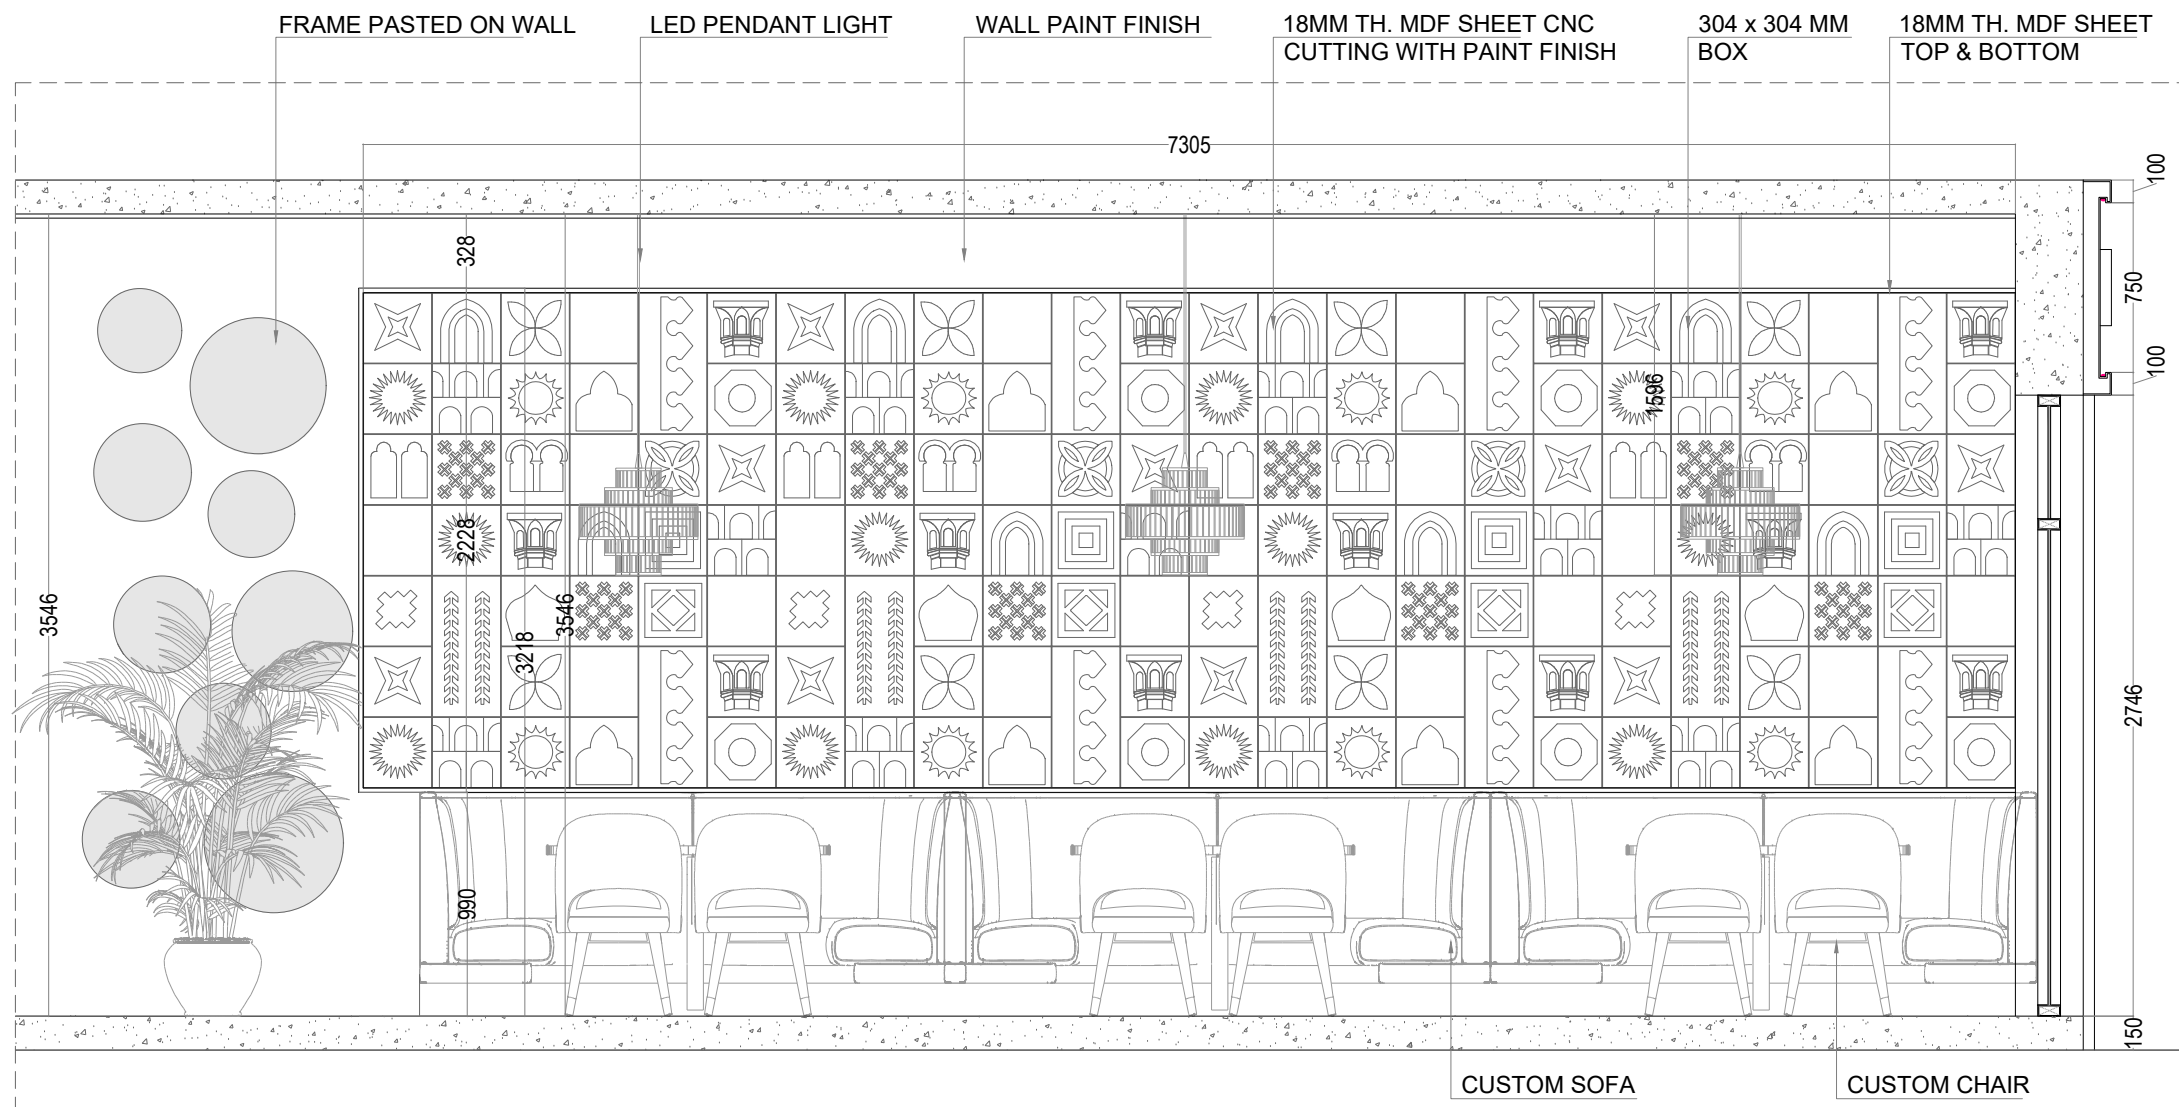

CNC CUTTING FEATURE WALL ELEVATION

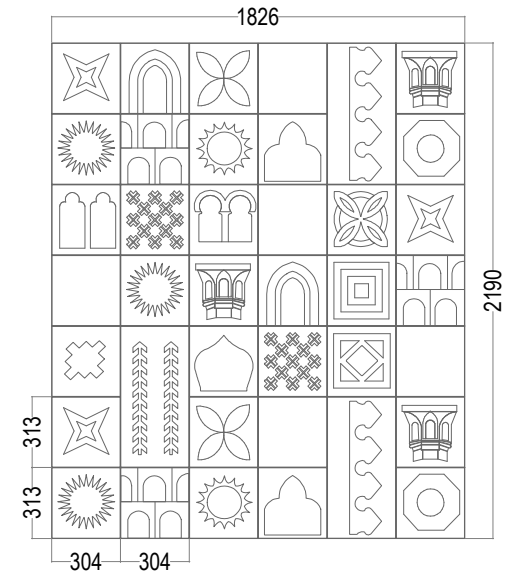

TYPICAL PATTERN FOR CNC CUTTING



36 ARCLAY CLOSE UB8 3WP
UXBRIDGE LONDON UK
+44 743 8881857

PROJECT NAME:

TASTE OF VILLAGE

OWNER'S NAME:

TASTE OF VILLAGE

PRINCIPAL ARCHITECT;

M.S.

TITLE

CNC CUTTING FEATURE WALL
ELEVATION -02

CHECKED BY :

M.S.

DRAWN BY:

FAIZAN ALI

Revised Dates :

Rev. _____

Rev. _____

Rev. _____

Rev. _____

Rev. _____

SCALE:

N.T.S

DATE:

22-10-2025

JOB NO.

25.1030

DRG NO.

ID -16

NOTES:

PRESENTATION
DRAWING NOT FOR
CONSTRUCTION



36 ARCLAY CLOSE UB8 3WP
UXBRIDGE LONDON UK

+44 743 8881857

PROJECT NAME:

TASTE OF VILLAGE

OWNER'S NAME:

TASTE OF VILLAGE

PRINCIPAL ARCHITECT;

M.S.

TITLE

FEATURE WALL ELEVATION -03

CHECKED BY :

M.S.

DRAWN BY:

FAIZAN ALI

Revised Dates :

Rev. _____

Rev. _____

Rev. _____

Rev. _____

SCALE:

N.T.S

DATE:

22-10-2025

JOB NO.

25.1030

DRG NO.

ID -17


NOTES:

PRESENTATION
DRAWING NOT FOR
CONSTRUCTION

18MM TH. MDF WOODEN
SLATS POLISH FINISH

18MM TH. MDF WOODEN
CHANNEL POLISH FINISH

18MM TH. MDF SHEET BULKHEAD
WITH TEXTURED PAINT FINISH

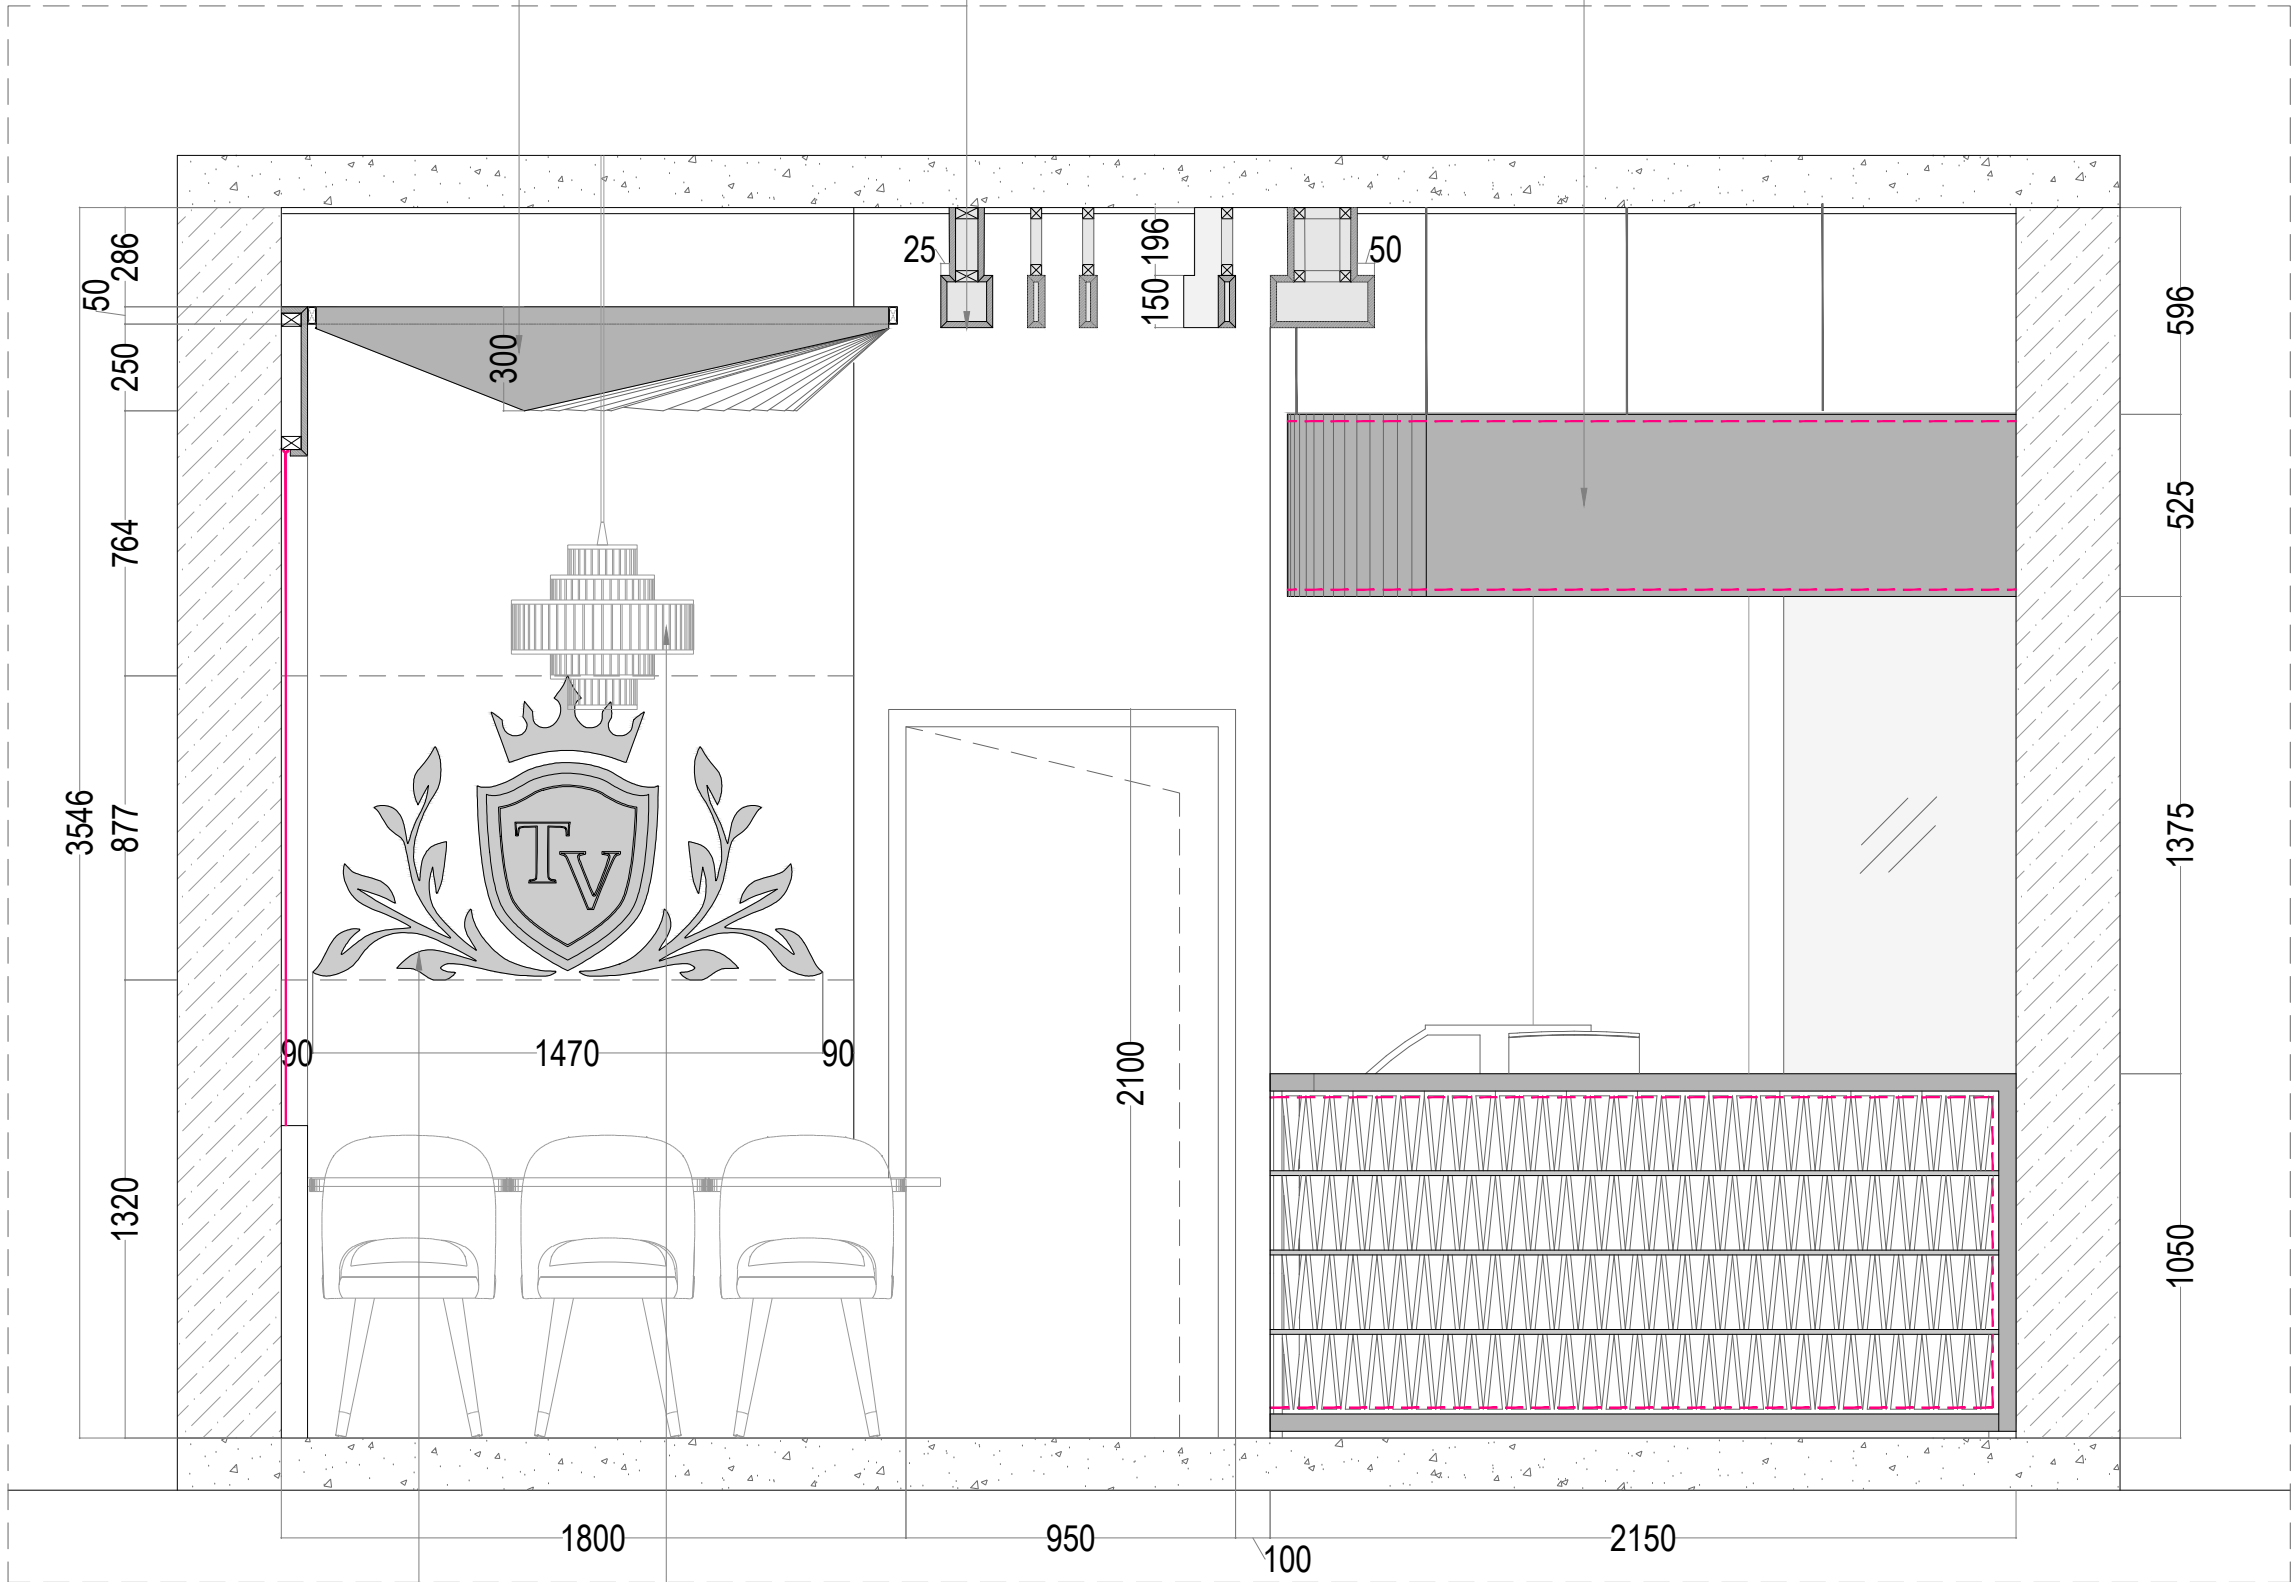

S.S LOGO
ELEVATION -03

PENDING LIGHT



36 ARCLAY CLOSE UB8 3WP
UXBRIDGE LONDON UK
+44 743 8881857

PROJECT NAME:

TASTE OF VILLAGE

OWNER'S NAME:

TASTE OF VILLAGE

PRINCIPAL ARCHITECT:

M.S.

TITLE

GROUND FLOOR
GRILL / COUNTER PLAN

CHECKED BY :

M.S.

DRAWN BY:

FAIZAN ALI

Revised Dates :

Rev. _____

Rev. _____

Rev. _____

Rev. _____

Rev. _____

SCALE:

N.T.S

DATE:

22-10-2025

JOB NO.


25.1030


DRG NO.

ID -18

NOTES:

PRESENTATION
DRAWING NOT FOR
CONSTRUCTION

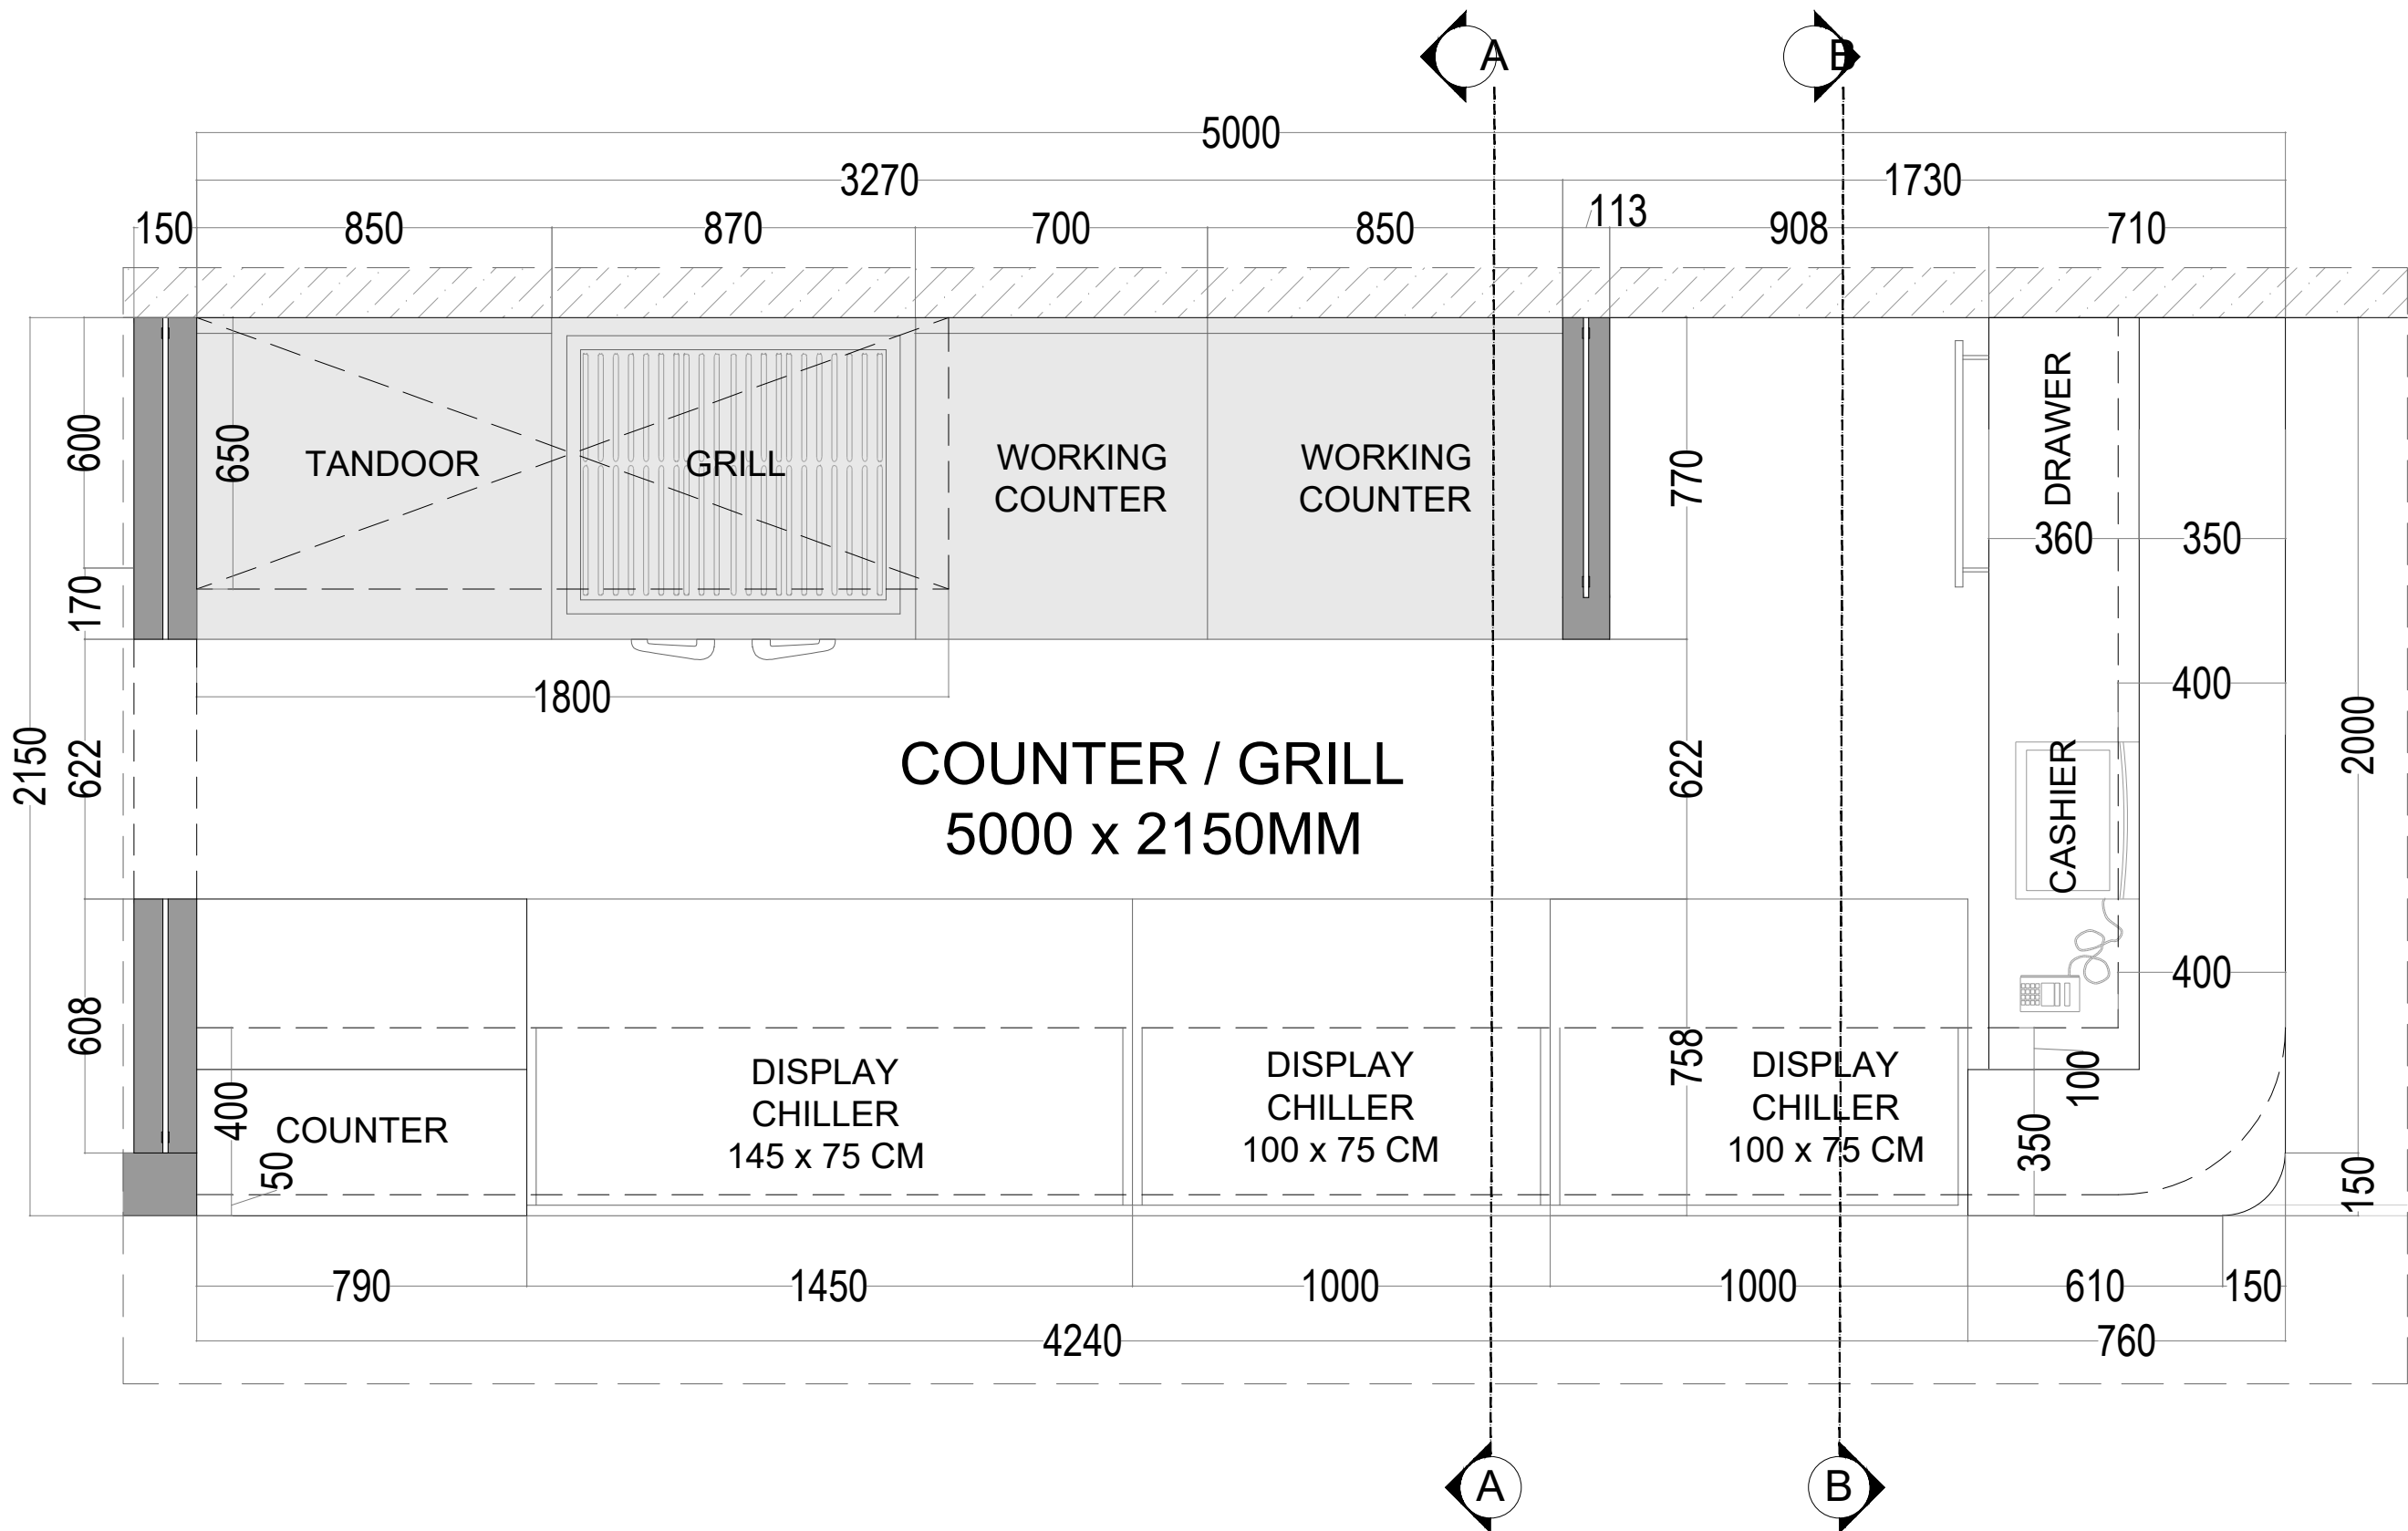

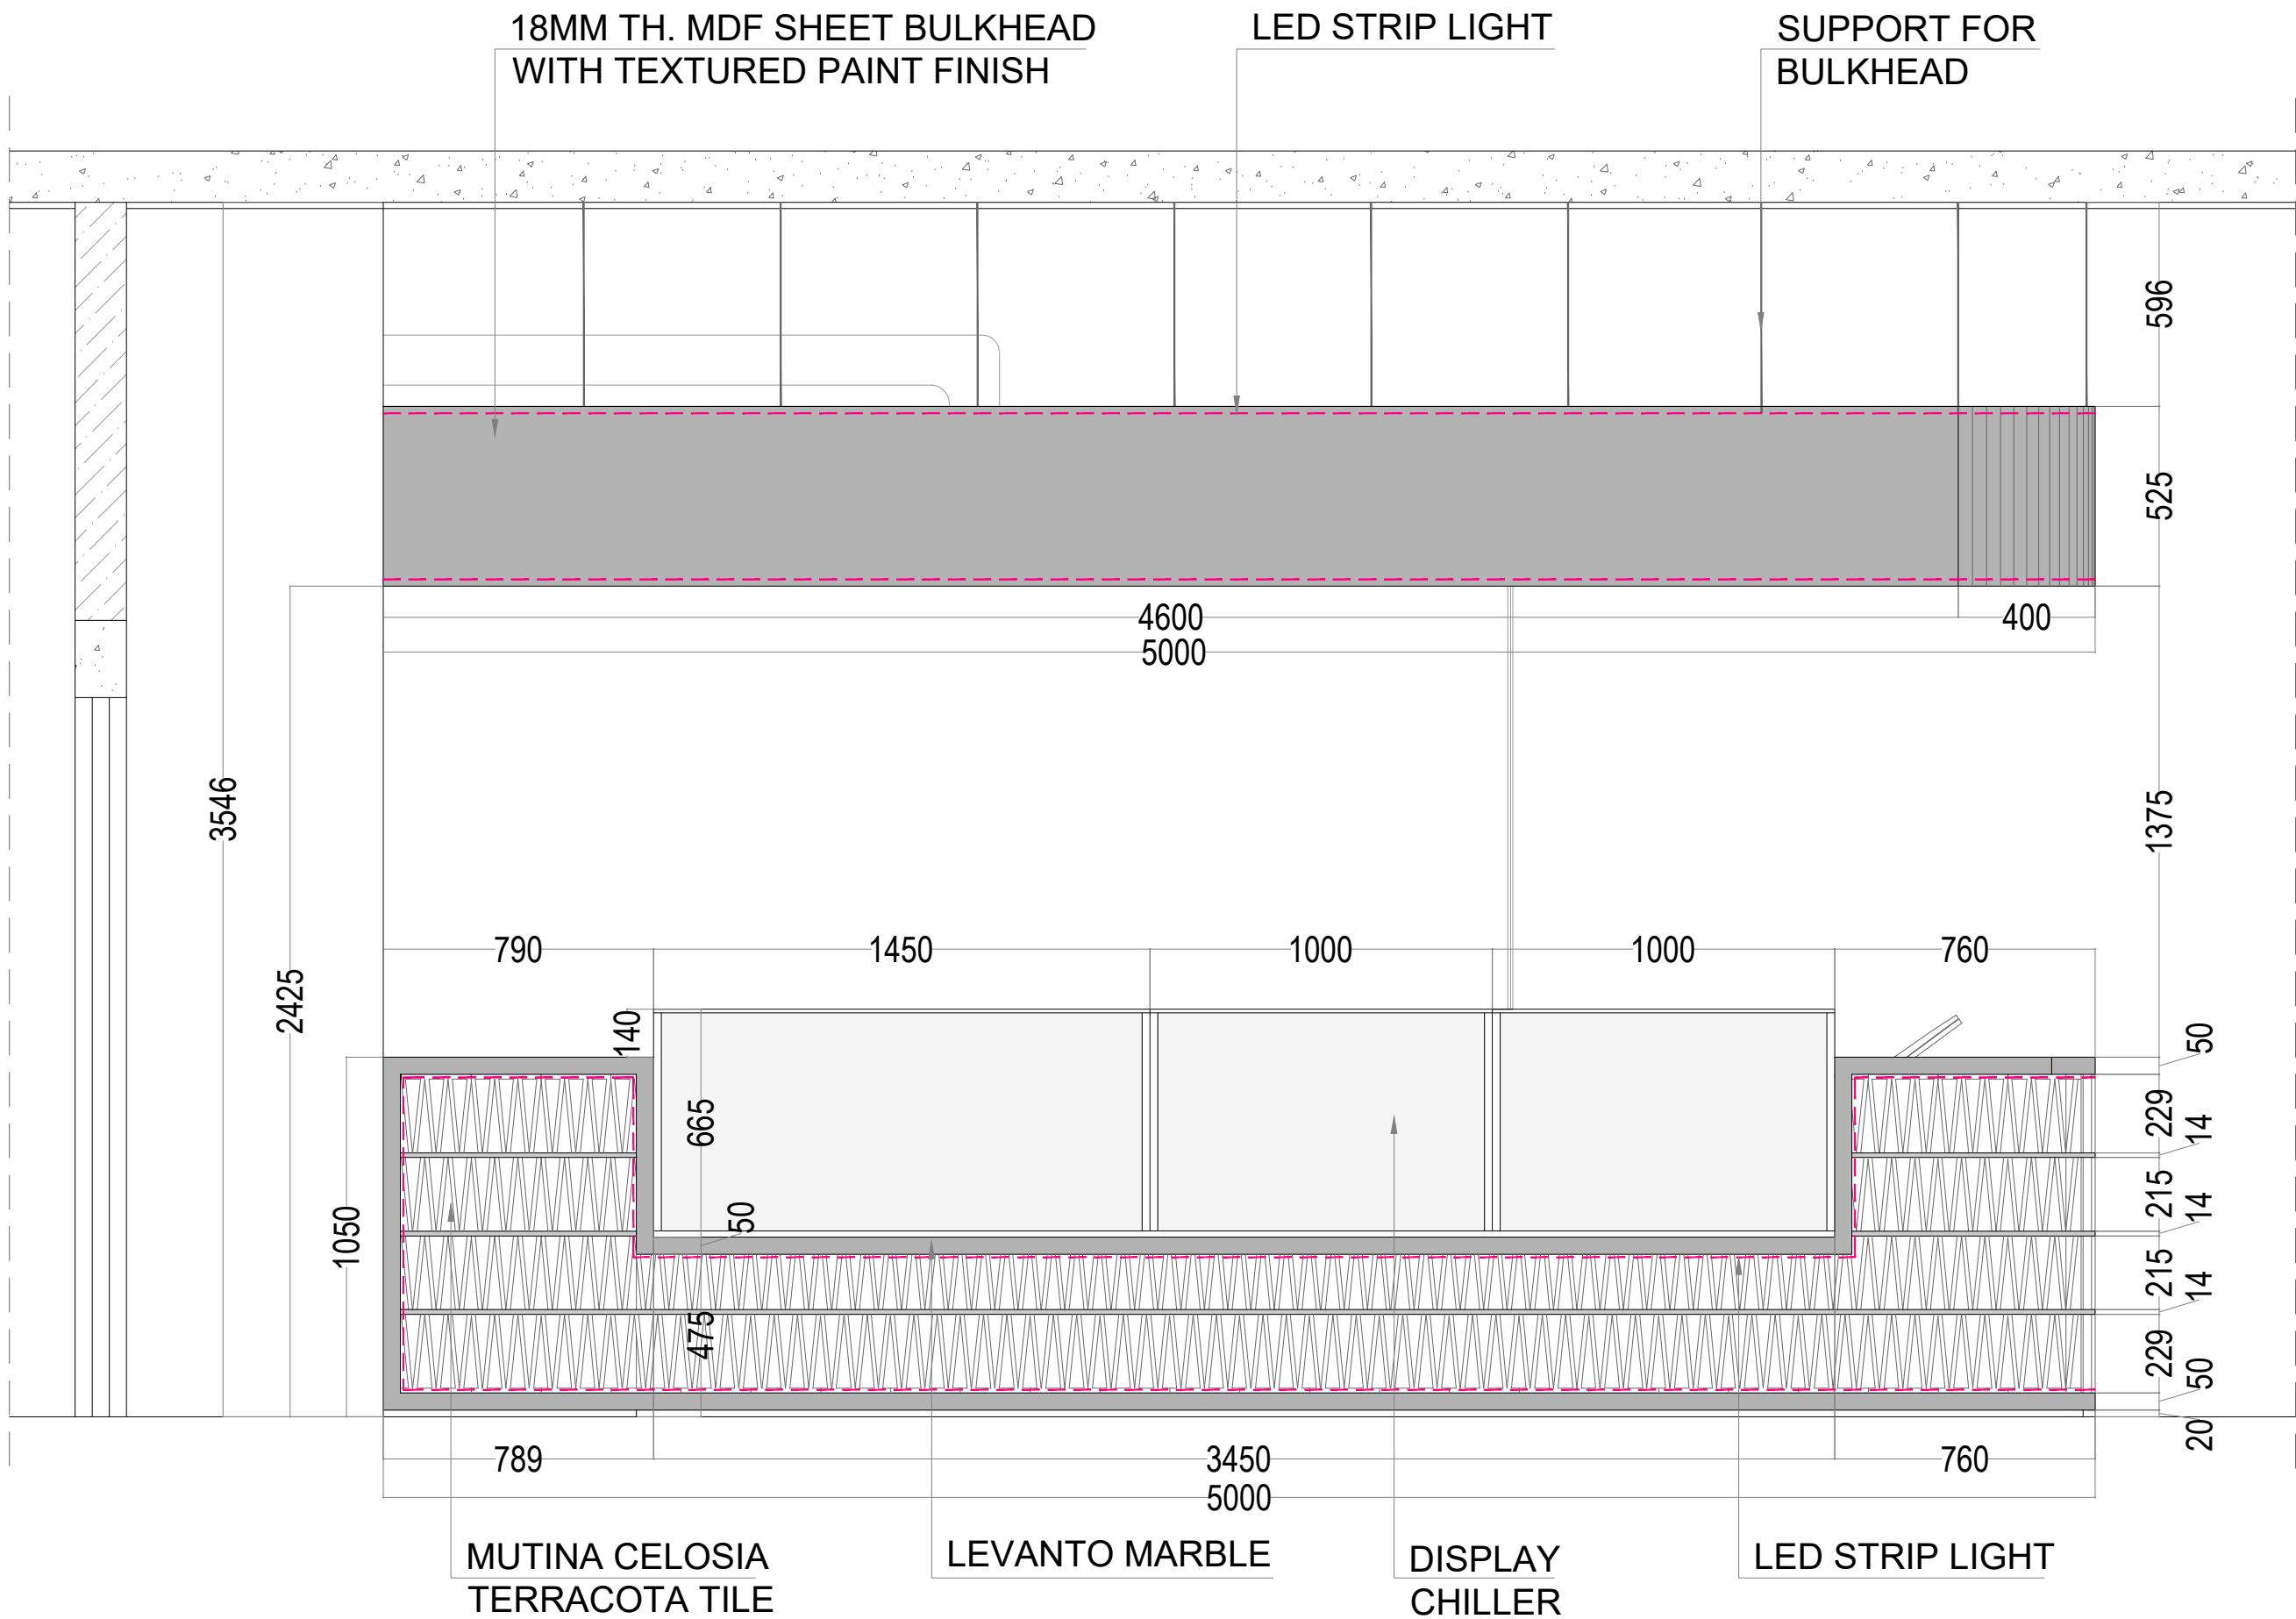

36 ARCLAY CLOSE UB8 3WP
UXBRIDGE LONDON UK
+44 743 8881857

PROJECT NAME:
TASTE OF VILLAGE

OWNER'S NAME:
TASTE OF VILLAGE

PRINCIPAL ARCHITECT;
M.S.
TITLE
GROUND FLOOR
GRILL / COUNTER FRONT
ELEVATION

CHECKED BY :
M.S.
DRAWN BY:
FAIZAN ALI


Revised Dates :
Rev. _____
Rev. _____
Rev. _____
Rev. _____
Rev. _____

SCALE:
N.T.S

DATE:
22-10-2025

JOB NO. DRG NO.
25.1030 ID -19

NOTES:
PRESENTATION
DRAWING NOT FOR
CONSTRUCTION

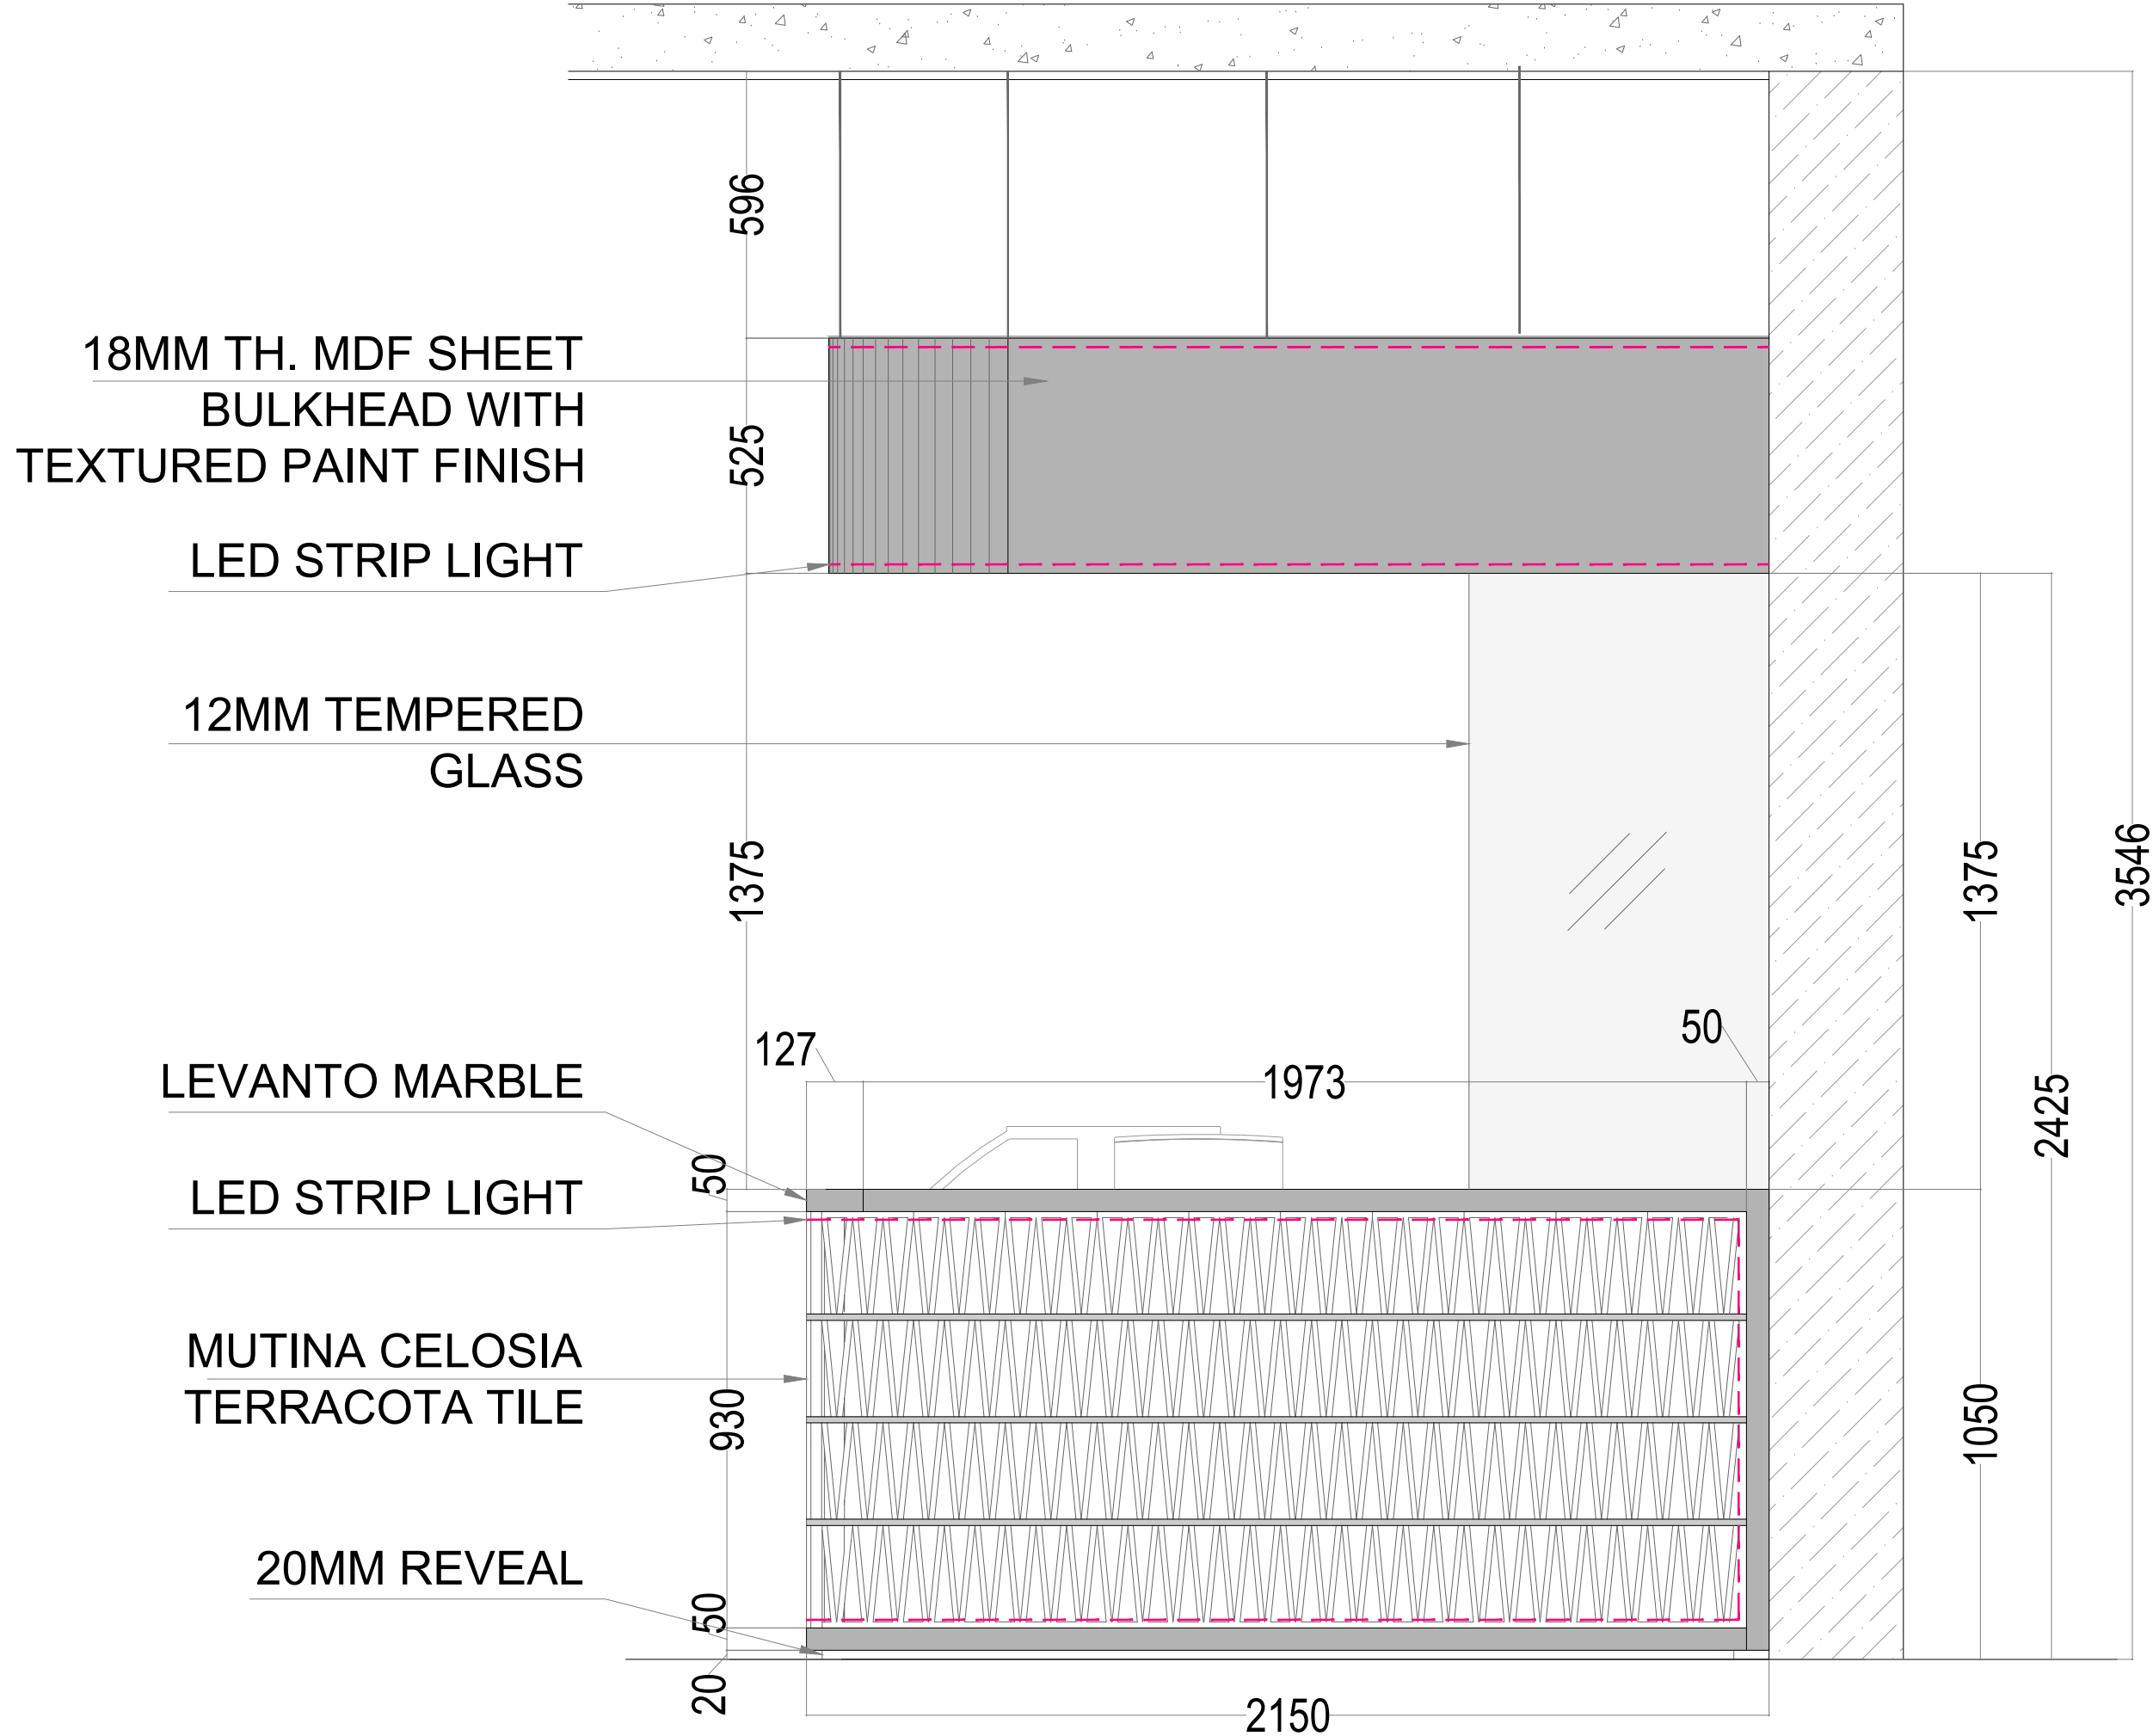

36 ARCLAY CLOSE UB8 3WP
UXBRIDGE LONDON UK
+44 743 8881857

PROJECT NAME:
TASTE OF VILLAGE

OWNER'S NAME:
TASTE OF VILLAGE

PRINCIPAL ARCHITECT;
M.S.

TITLE
GROUND FLOOR
GRILL / COUNTER SIDE
ELEVATION

CHECKED BY :
M.S.
DRAWN BY:
FAIZAN ALI


Revised Dates :
Rev. _____
Rev. _____
Rev. _____
Rev. _____
Rev. _____

SCALE:
N.T.S

DATE:
22-10-2025

JOB NO.	DRG NO.
25.1030	ID -20

NOTES:
PRESENTATION
DRAWING NOT FOR
CONSTRUCTION

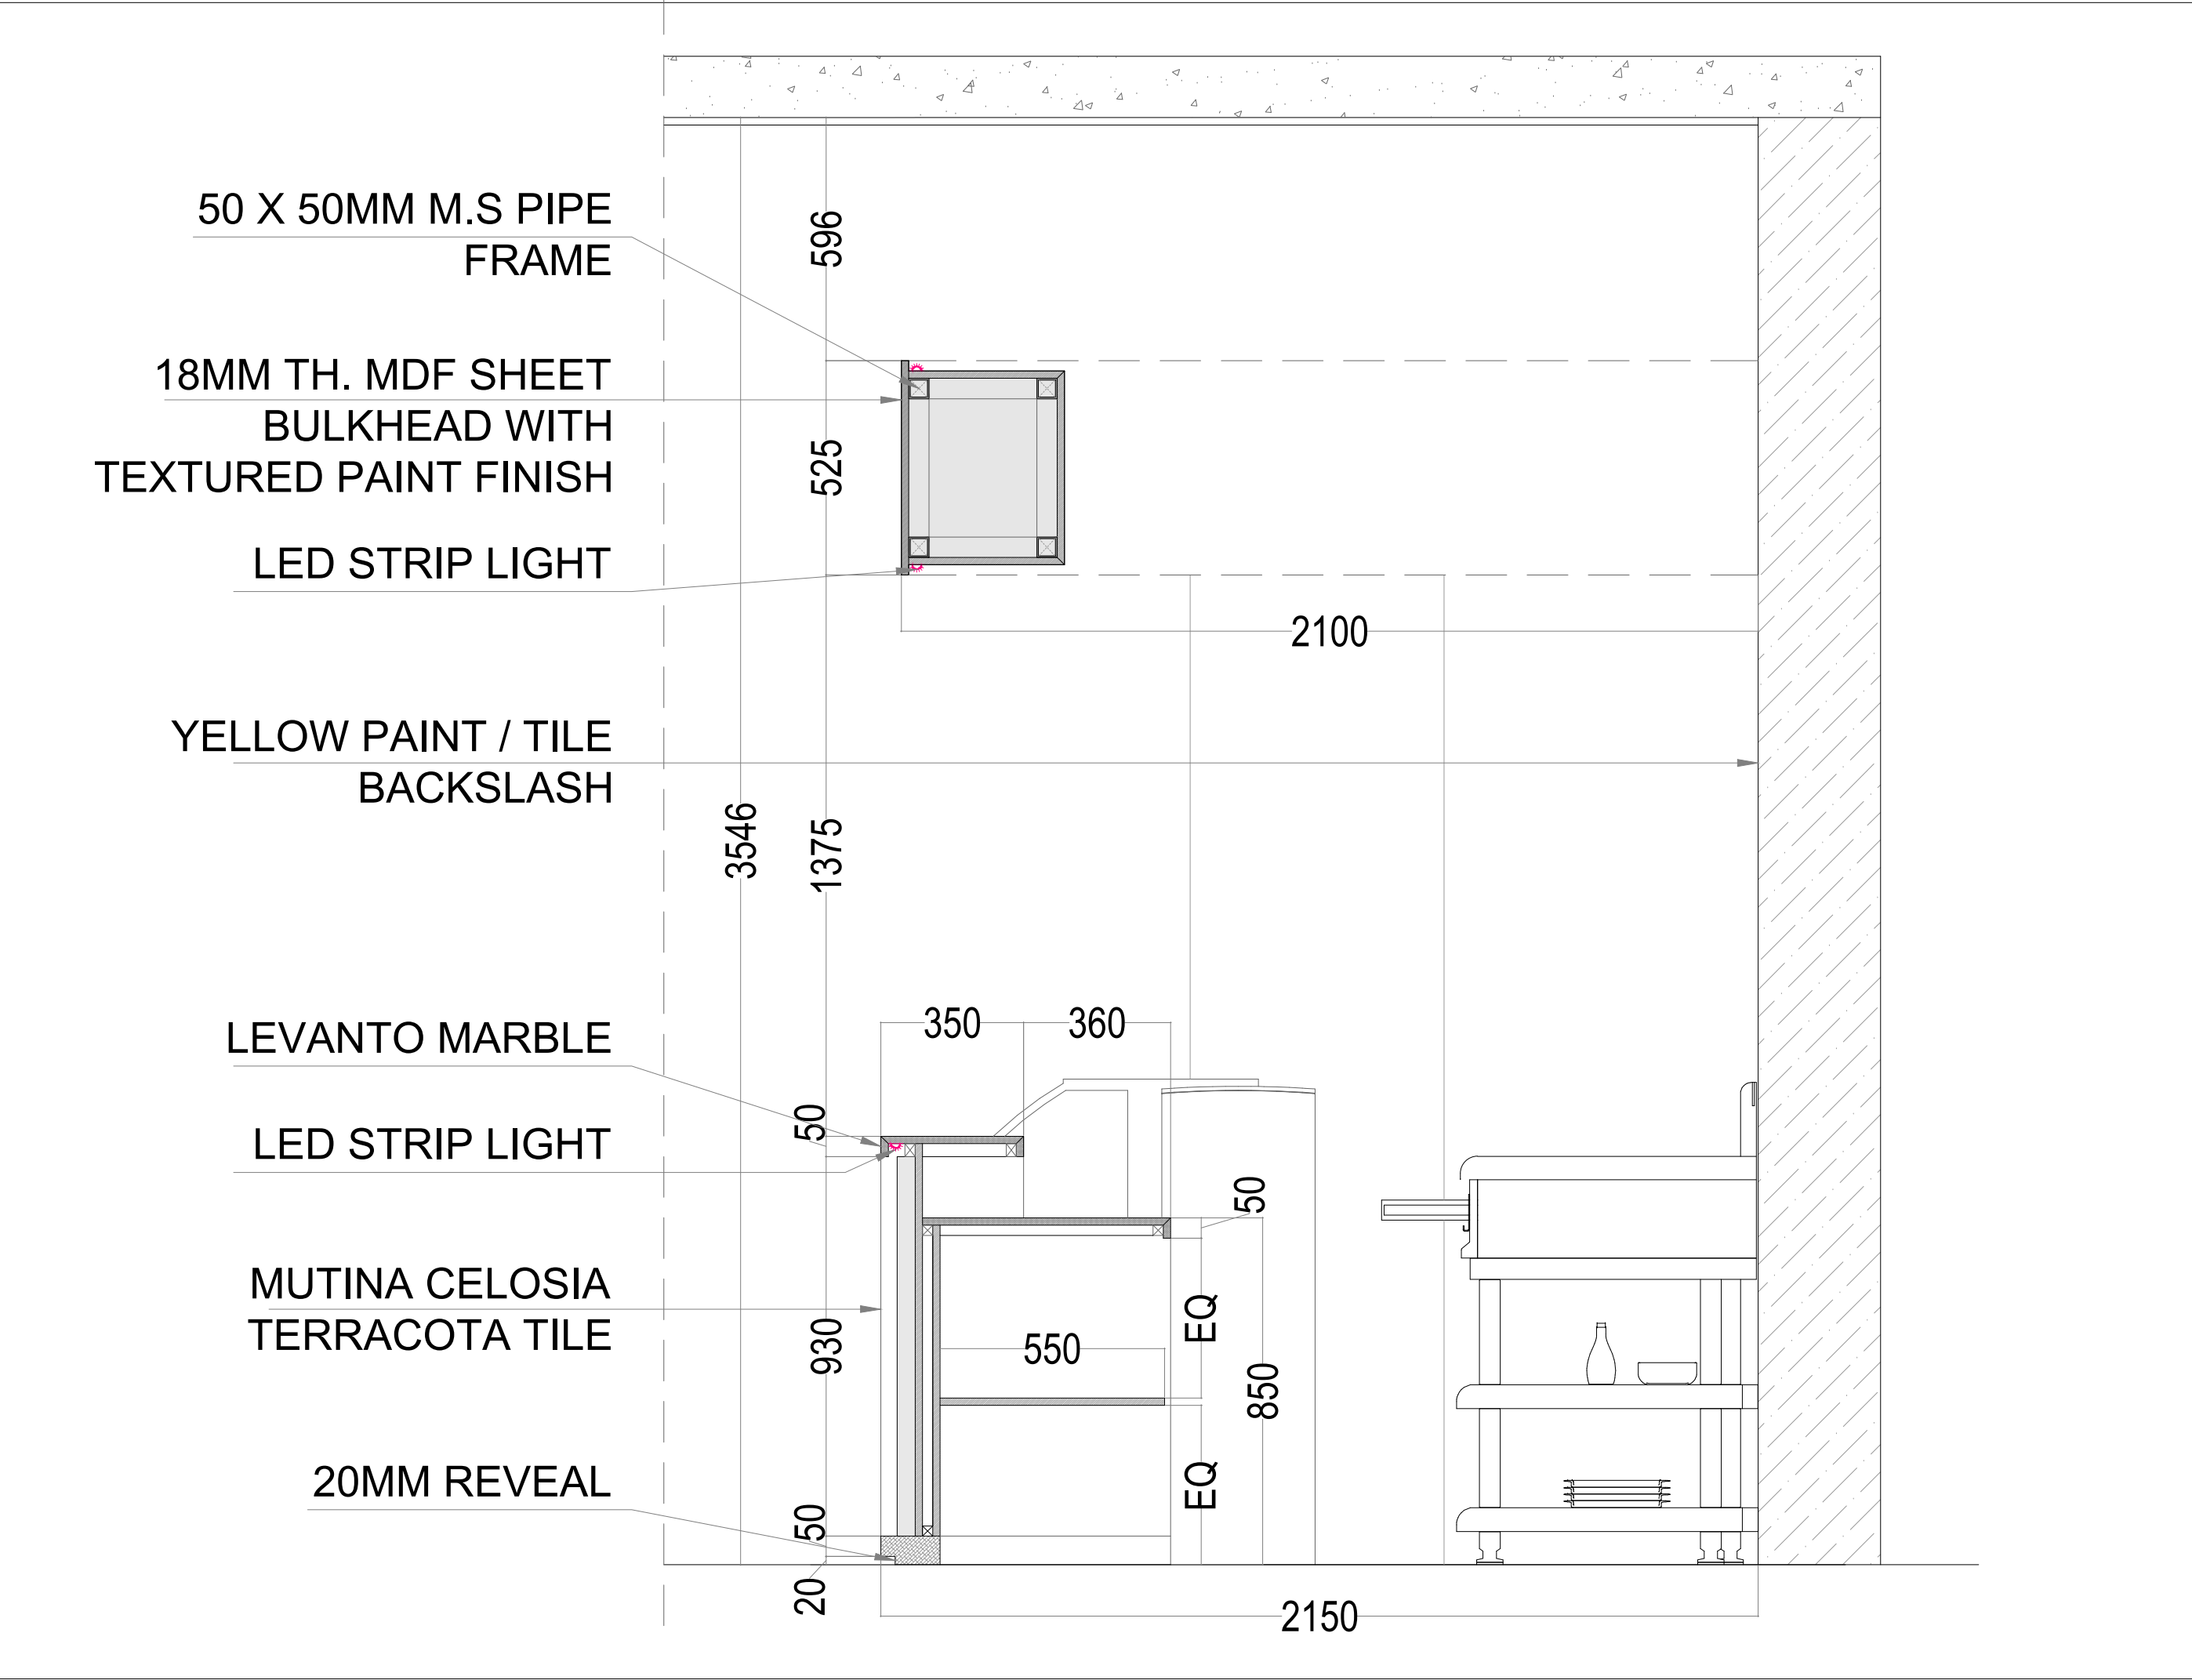

36 ARCLAY CLOSE UB8 3WP
UXBRIDGE LONDON UK
+44 743 8881857

PROJECT NAME:

TASTE OF VILLAGE

OWNER'S NAME:

TASTE OF VILLAGE

PRINCIPAL ARCHITECT;

M.S.

TITLE

GROUND FLOOR
GRILL / COUNTER
SECTION AT A-A'

CHECKED BY :

M.S.

DRAWN BY:

FAIZAN ALI

Revised Dates :

Rev. _____

Rev. _____

Rev. _____

Rev. _____

SCALE:

N.T.S

DATE:

22-10-2025

JOB NO.


25.1030

DRG NO.

ID -21

NOTES:

PRESENTATION
DRAWING NOT FOR
CONSTRUCTION

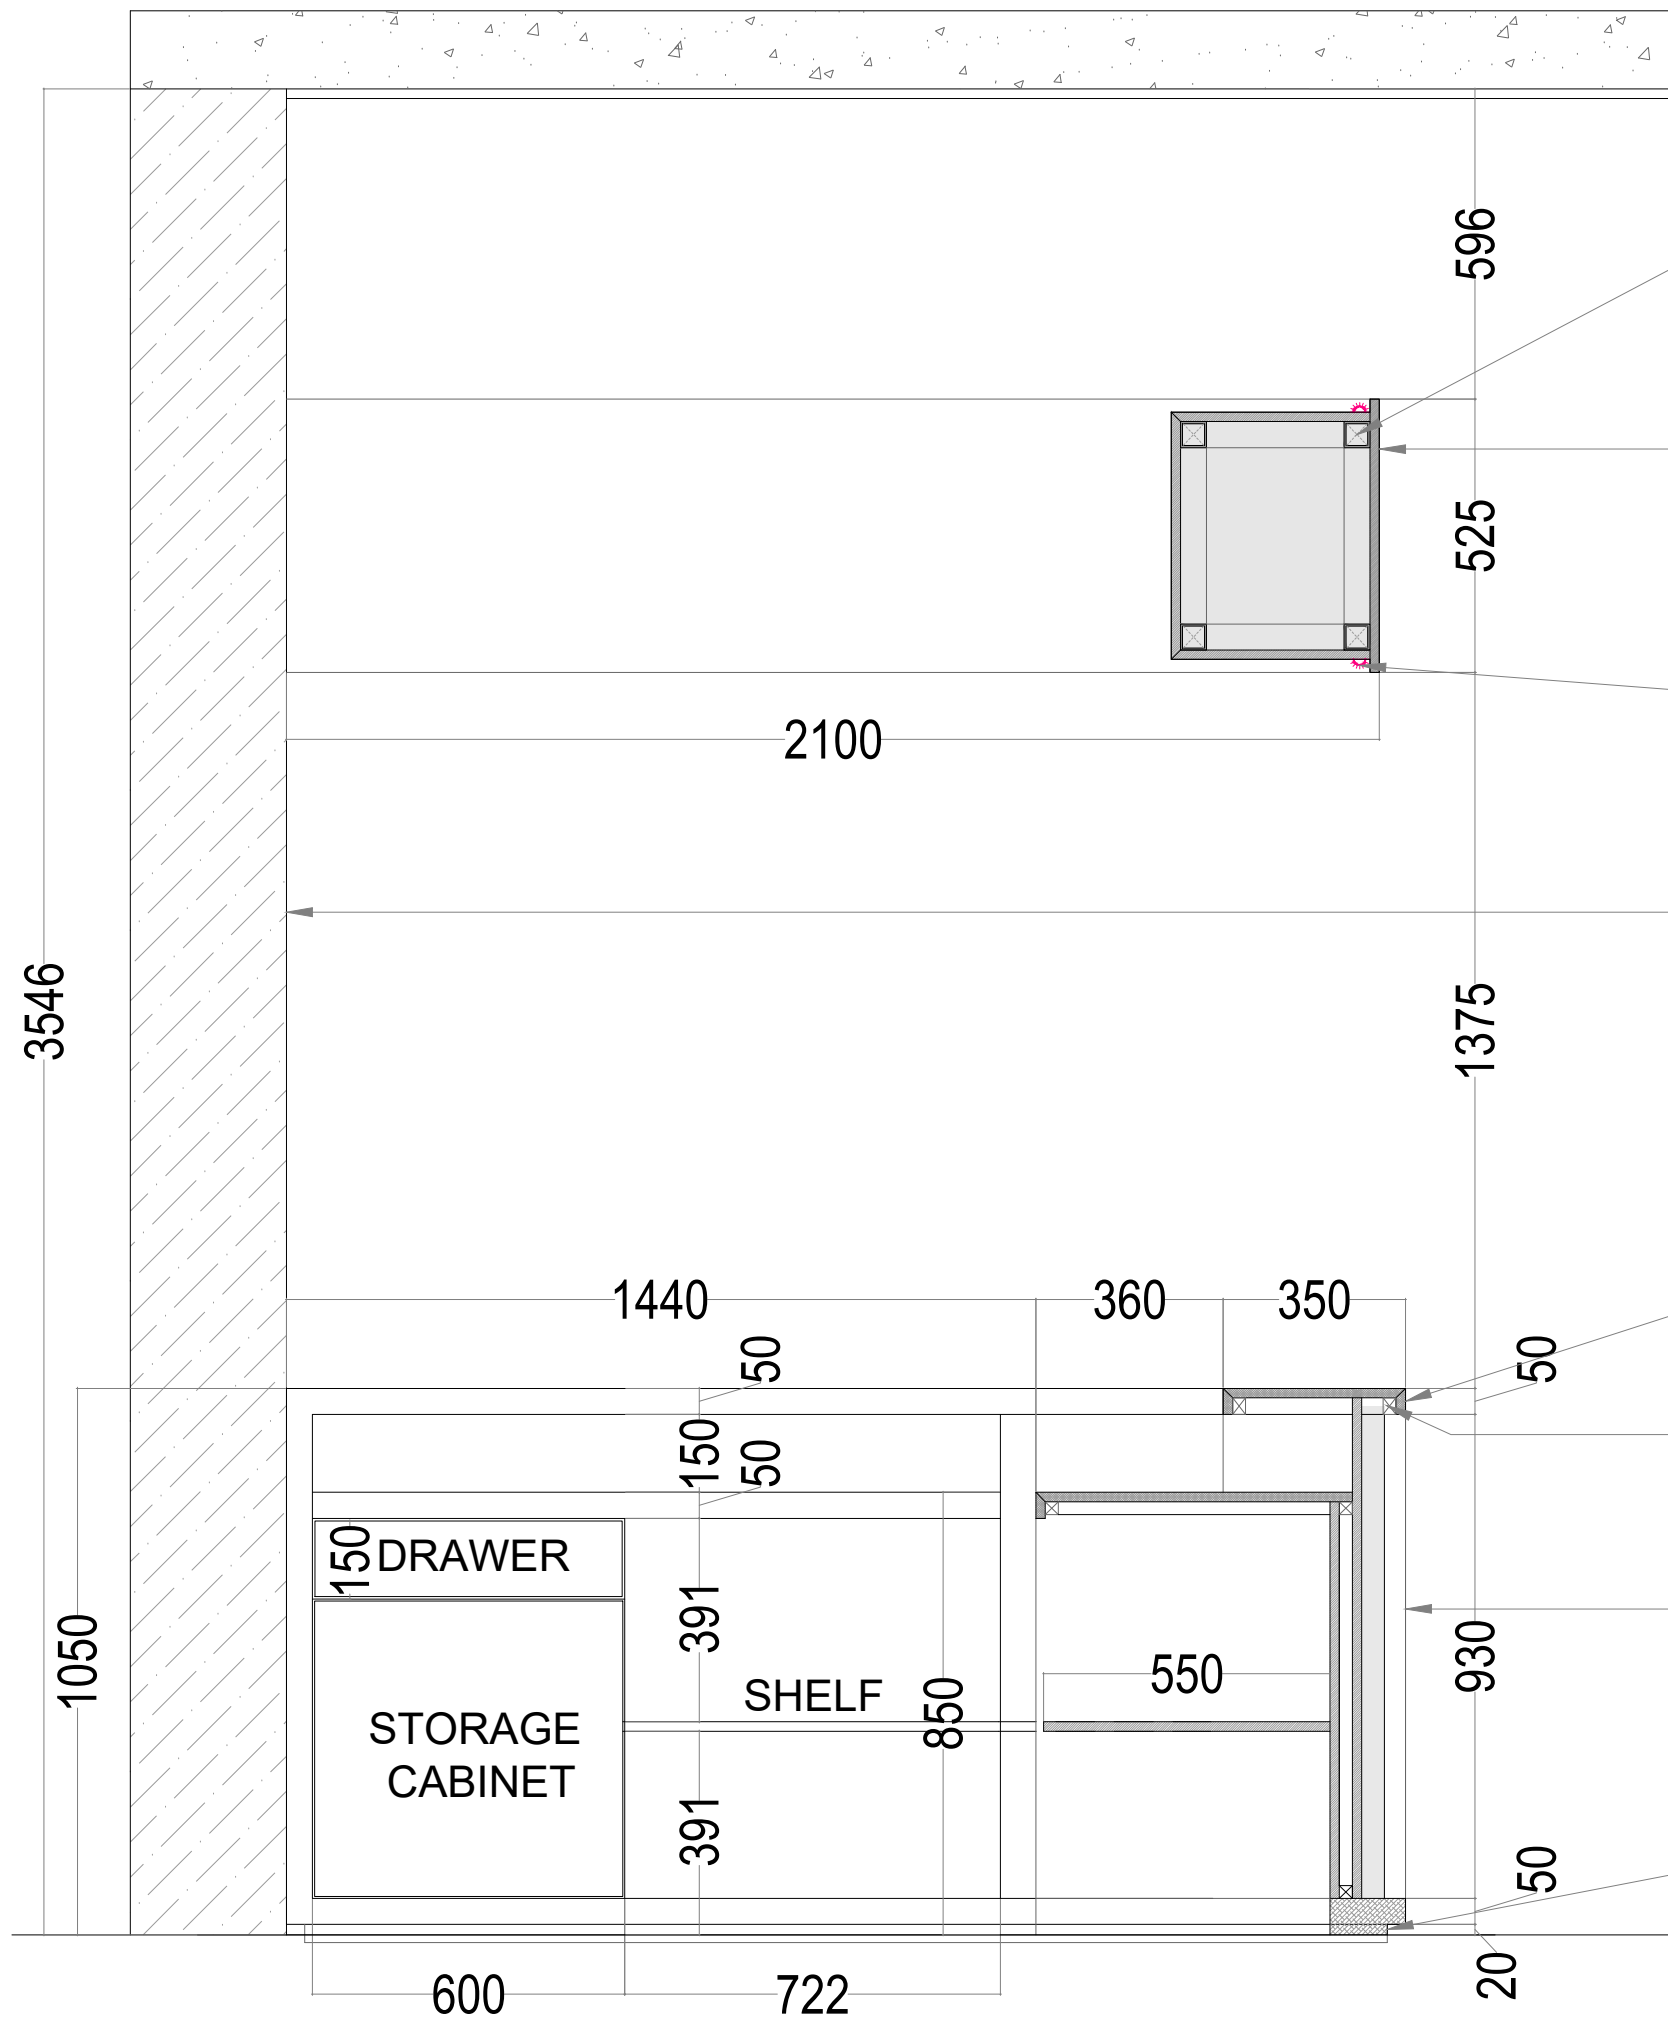

3546

1050

600

722

2100

1440

150

50

391

50

850

391

50

391

50

391

50

360

350

550

1375

525

596

50

50

20

50 X 50MM M.S PIPE
FRAME

18MM TH. MDF SHEET
BULKHEAD WITH
TEXTURED PAINT FINISH

LED STRIP LIGHT

YELLOW PAINT / TILE
BACKSLASH

LEVANTO MARBLE

LED STRIP LIGHT

MUTINA CELOSIA
TERRACOTA TILE

20MM REVEAL



36 ARCLAY CLOSE UB8 3WP
UXBRIDGE LONDON UK
+44 743 8881857

PROJECT NAME:
TASTE OF VILLAGE

OWNER'S NAME:
TASTE OF VILLAGE

PRINCIPAL ARCHITECT;
M.S.

TITLE
GROUND FLOOR
GRILL / COUNTER
SECTION AT B-B'

CHECKED BY :
M.S.

DRAWN BY:
FAIZAN ALI

Revised Dates :
Rev. _____
Rev. _____
Rev. _____
Rev. _____
Rev. _____
Rev. _____

SCALE:
N.T.S

DATE:
22-10-2025

JOB NO. 25.1030	DRG NO. ID -22
--------------------	-------------------

NOTES:
PRESENTATION
DRAWING NOT FOR
CONSTRUCTION



36 ARCLAY CLOSE UB8 3WP
UXBRIDGE LONDON UK
+44 743 8881857

PROJECT NAME:

TASTE OF VILLAGE

OWNER'S NAME:

TASTE OF VILLAGE

PRINCIPAL ARCHITECT;

M.S.

TITLE

GROUND FLOOR
MAIN ENTRANCE PLAN

CHECKED BY :

M.S.

DRAWN BY:

FAIZAN ALI

Revised Dates :

Rev. _____

Rev. _____

Rev. _____

Rev. _____

SCALE:

N.T.S

DATE:

22-10-2025

JOB NO.


25.1030

DRG NO.

ID -23

NOTES:

PRESENTATION
DRAWING NOT FOR
CONSTRUCTION

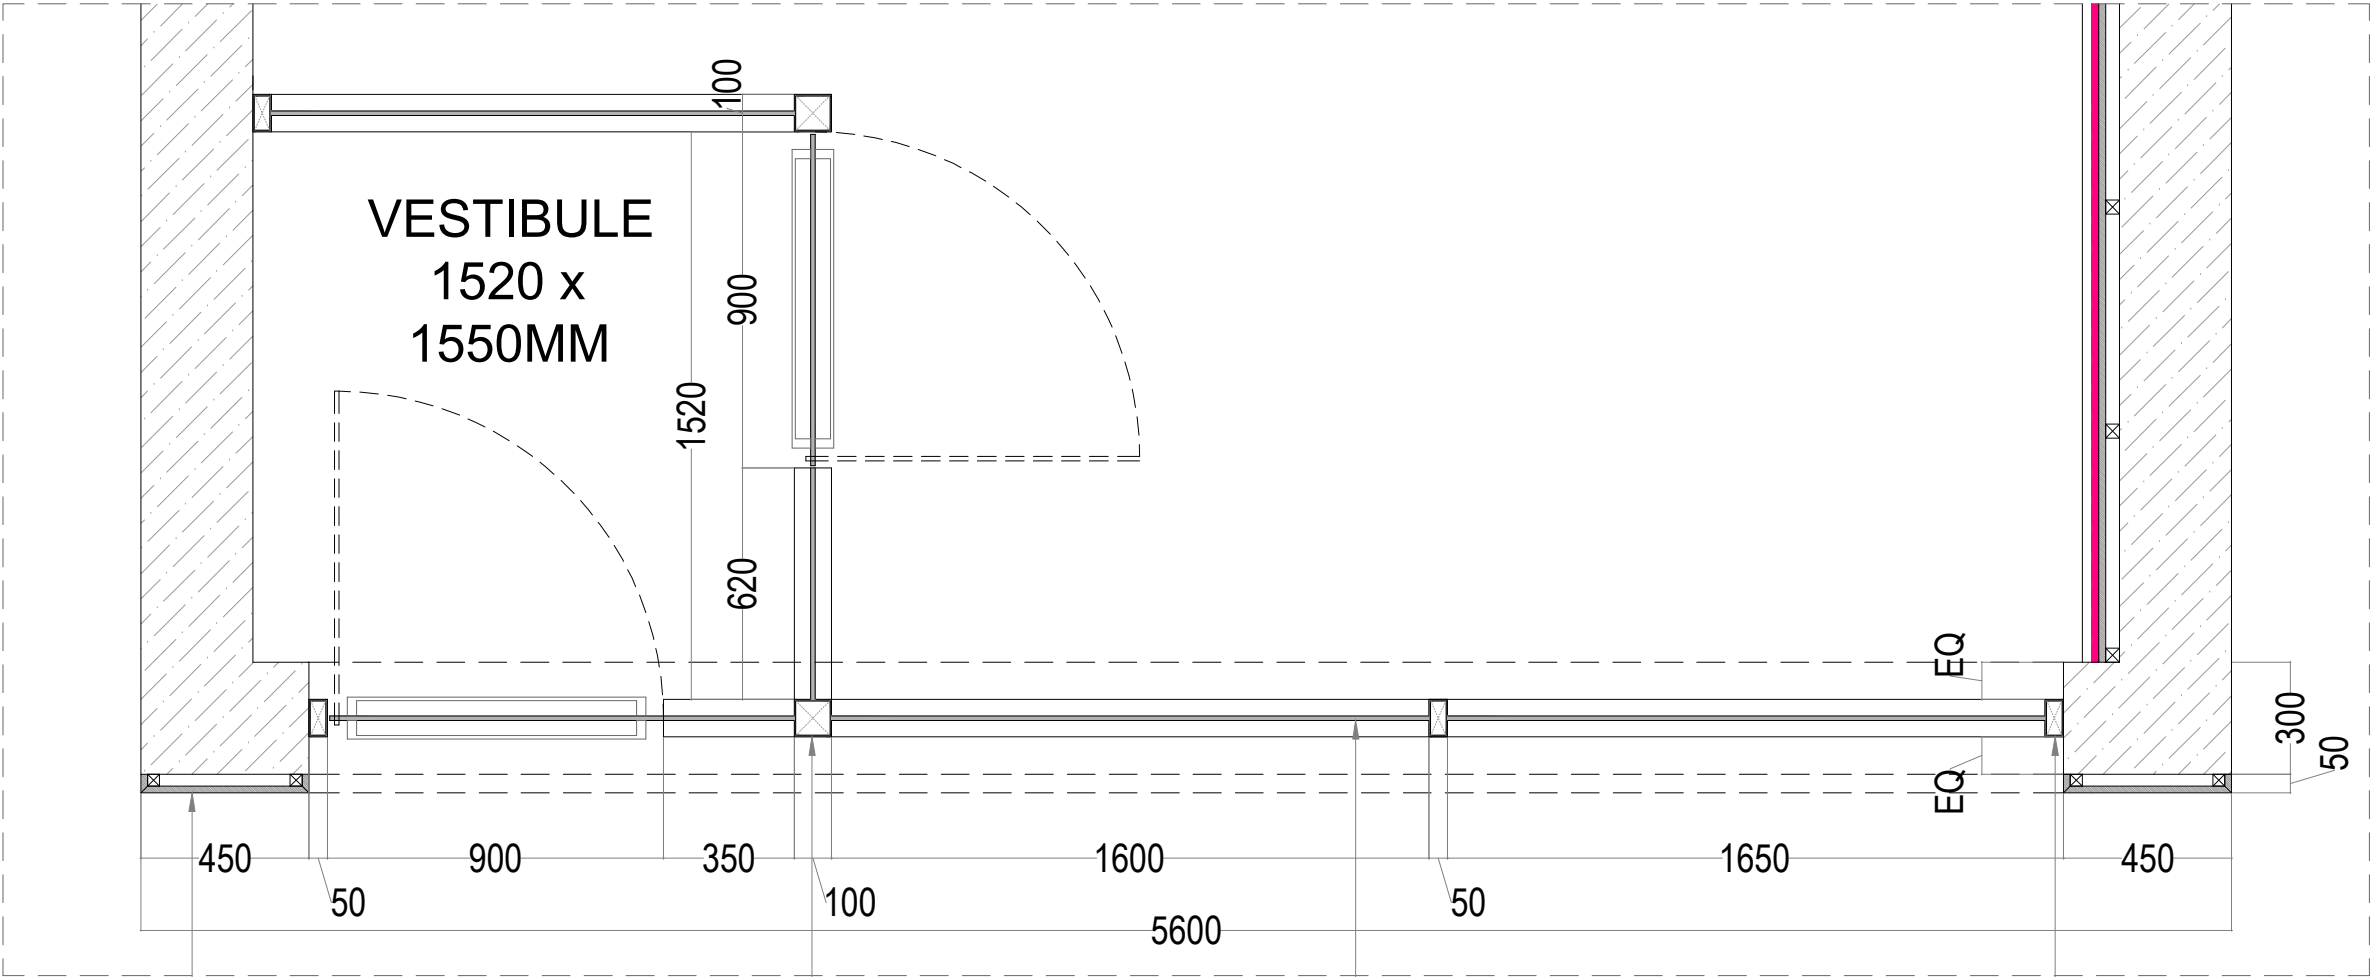


CEMENT BOARD WITH
PAINT FINISH

100 x 100MM ALUMINIUM
CHANNEL FOR GLASS

12MM TEMPERED GLASS
FULL HEIGHT WALL

50 x 100MM ALUMINIUM
CHANNEL FOR GLASS

MAIN ENT. PLAN

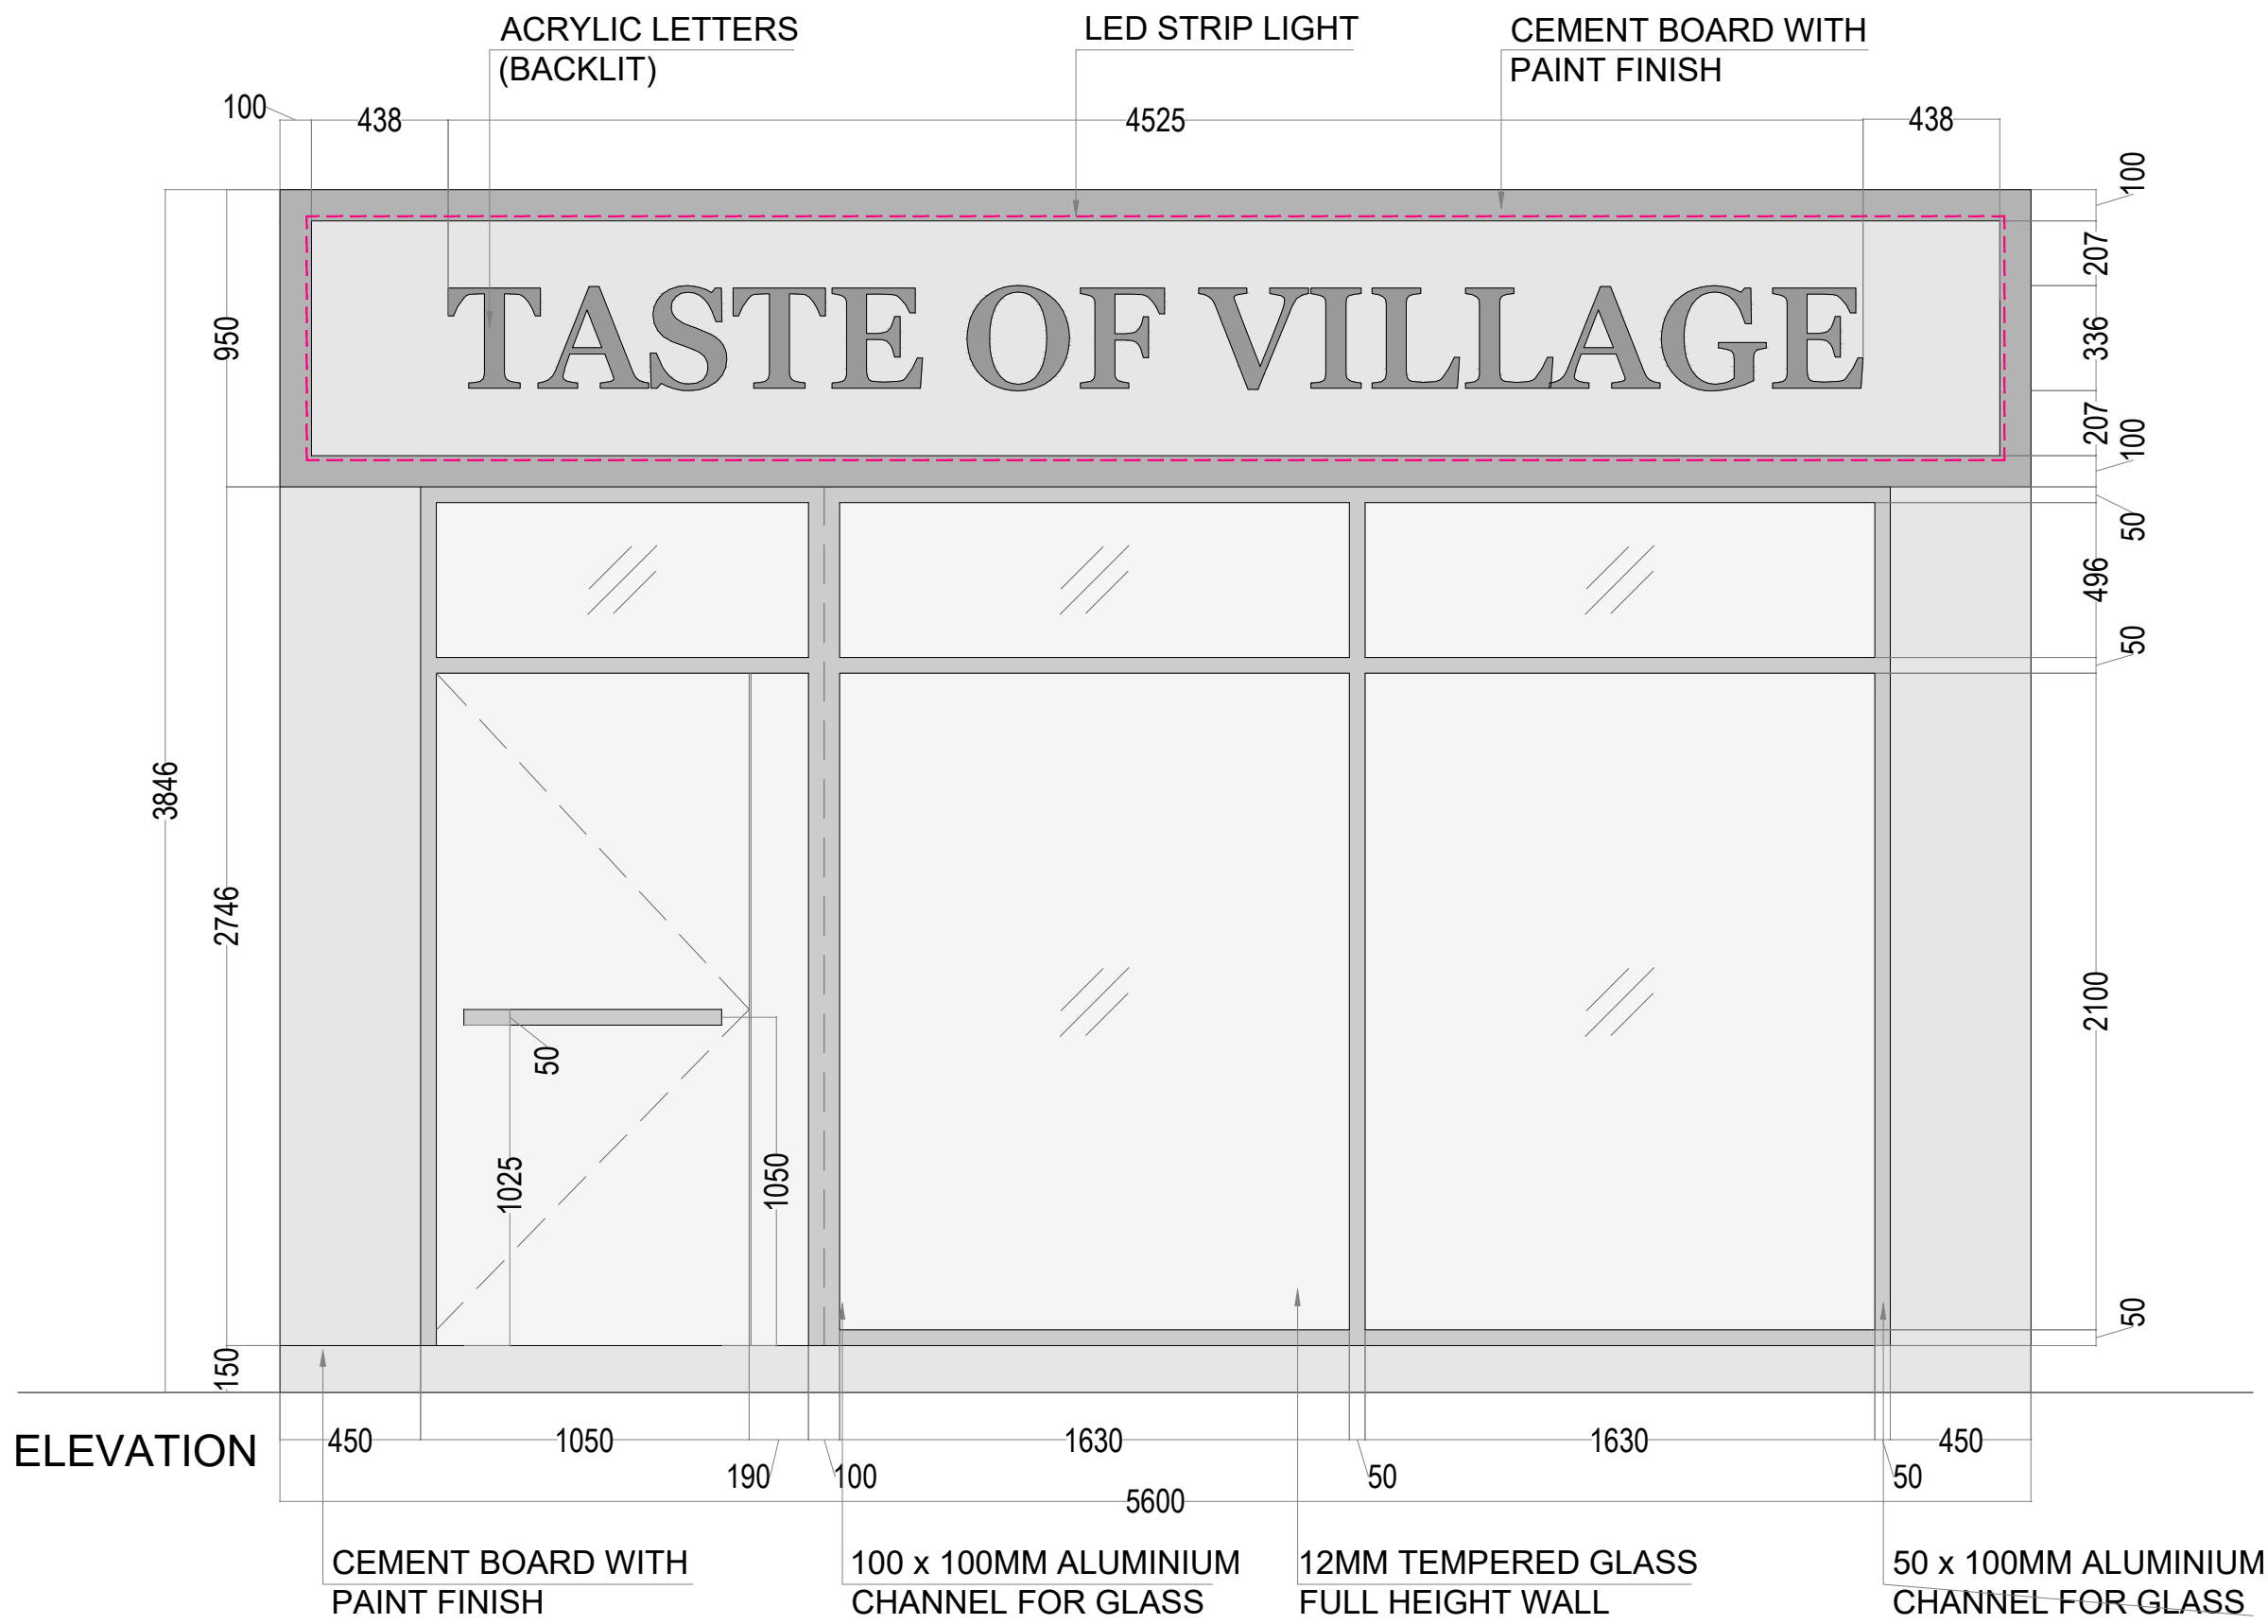

36 ARCLAY CLOSE UB8 3WP
UXBRIDGE LONDON UK
+44 743 8881857

PROJECT NAME:

TASTE OF VILLAGE

OWNER'S NAME:

TASTE OF VILLAGE

PRINCIPAL ARCHITECT;

M.S.

TITLE

GROUND FLOOR
MAIN ENTRANCE ELEVATION

CHECKED BY :

M.S.

DRAWN BY:

FAIZAN ALI

Revised Dates :

Rev. _____

Rev. _____

Rev. _____

Rev. _____

Rev. _____

SCALE:

N.T.S

DATE:

22-10-2025

JOB NO.


25.1030

DRG NO.

ID -24

NOTES:

PRESENTATION
DRAWING NOT FOR
CONSTRUCTION

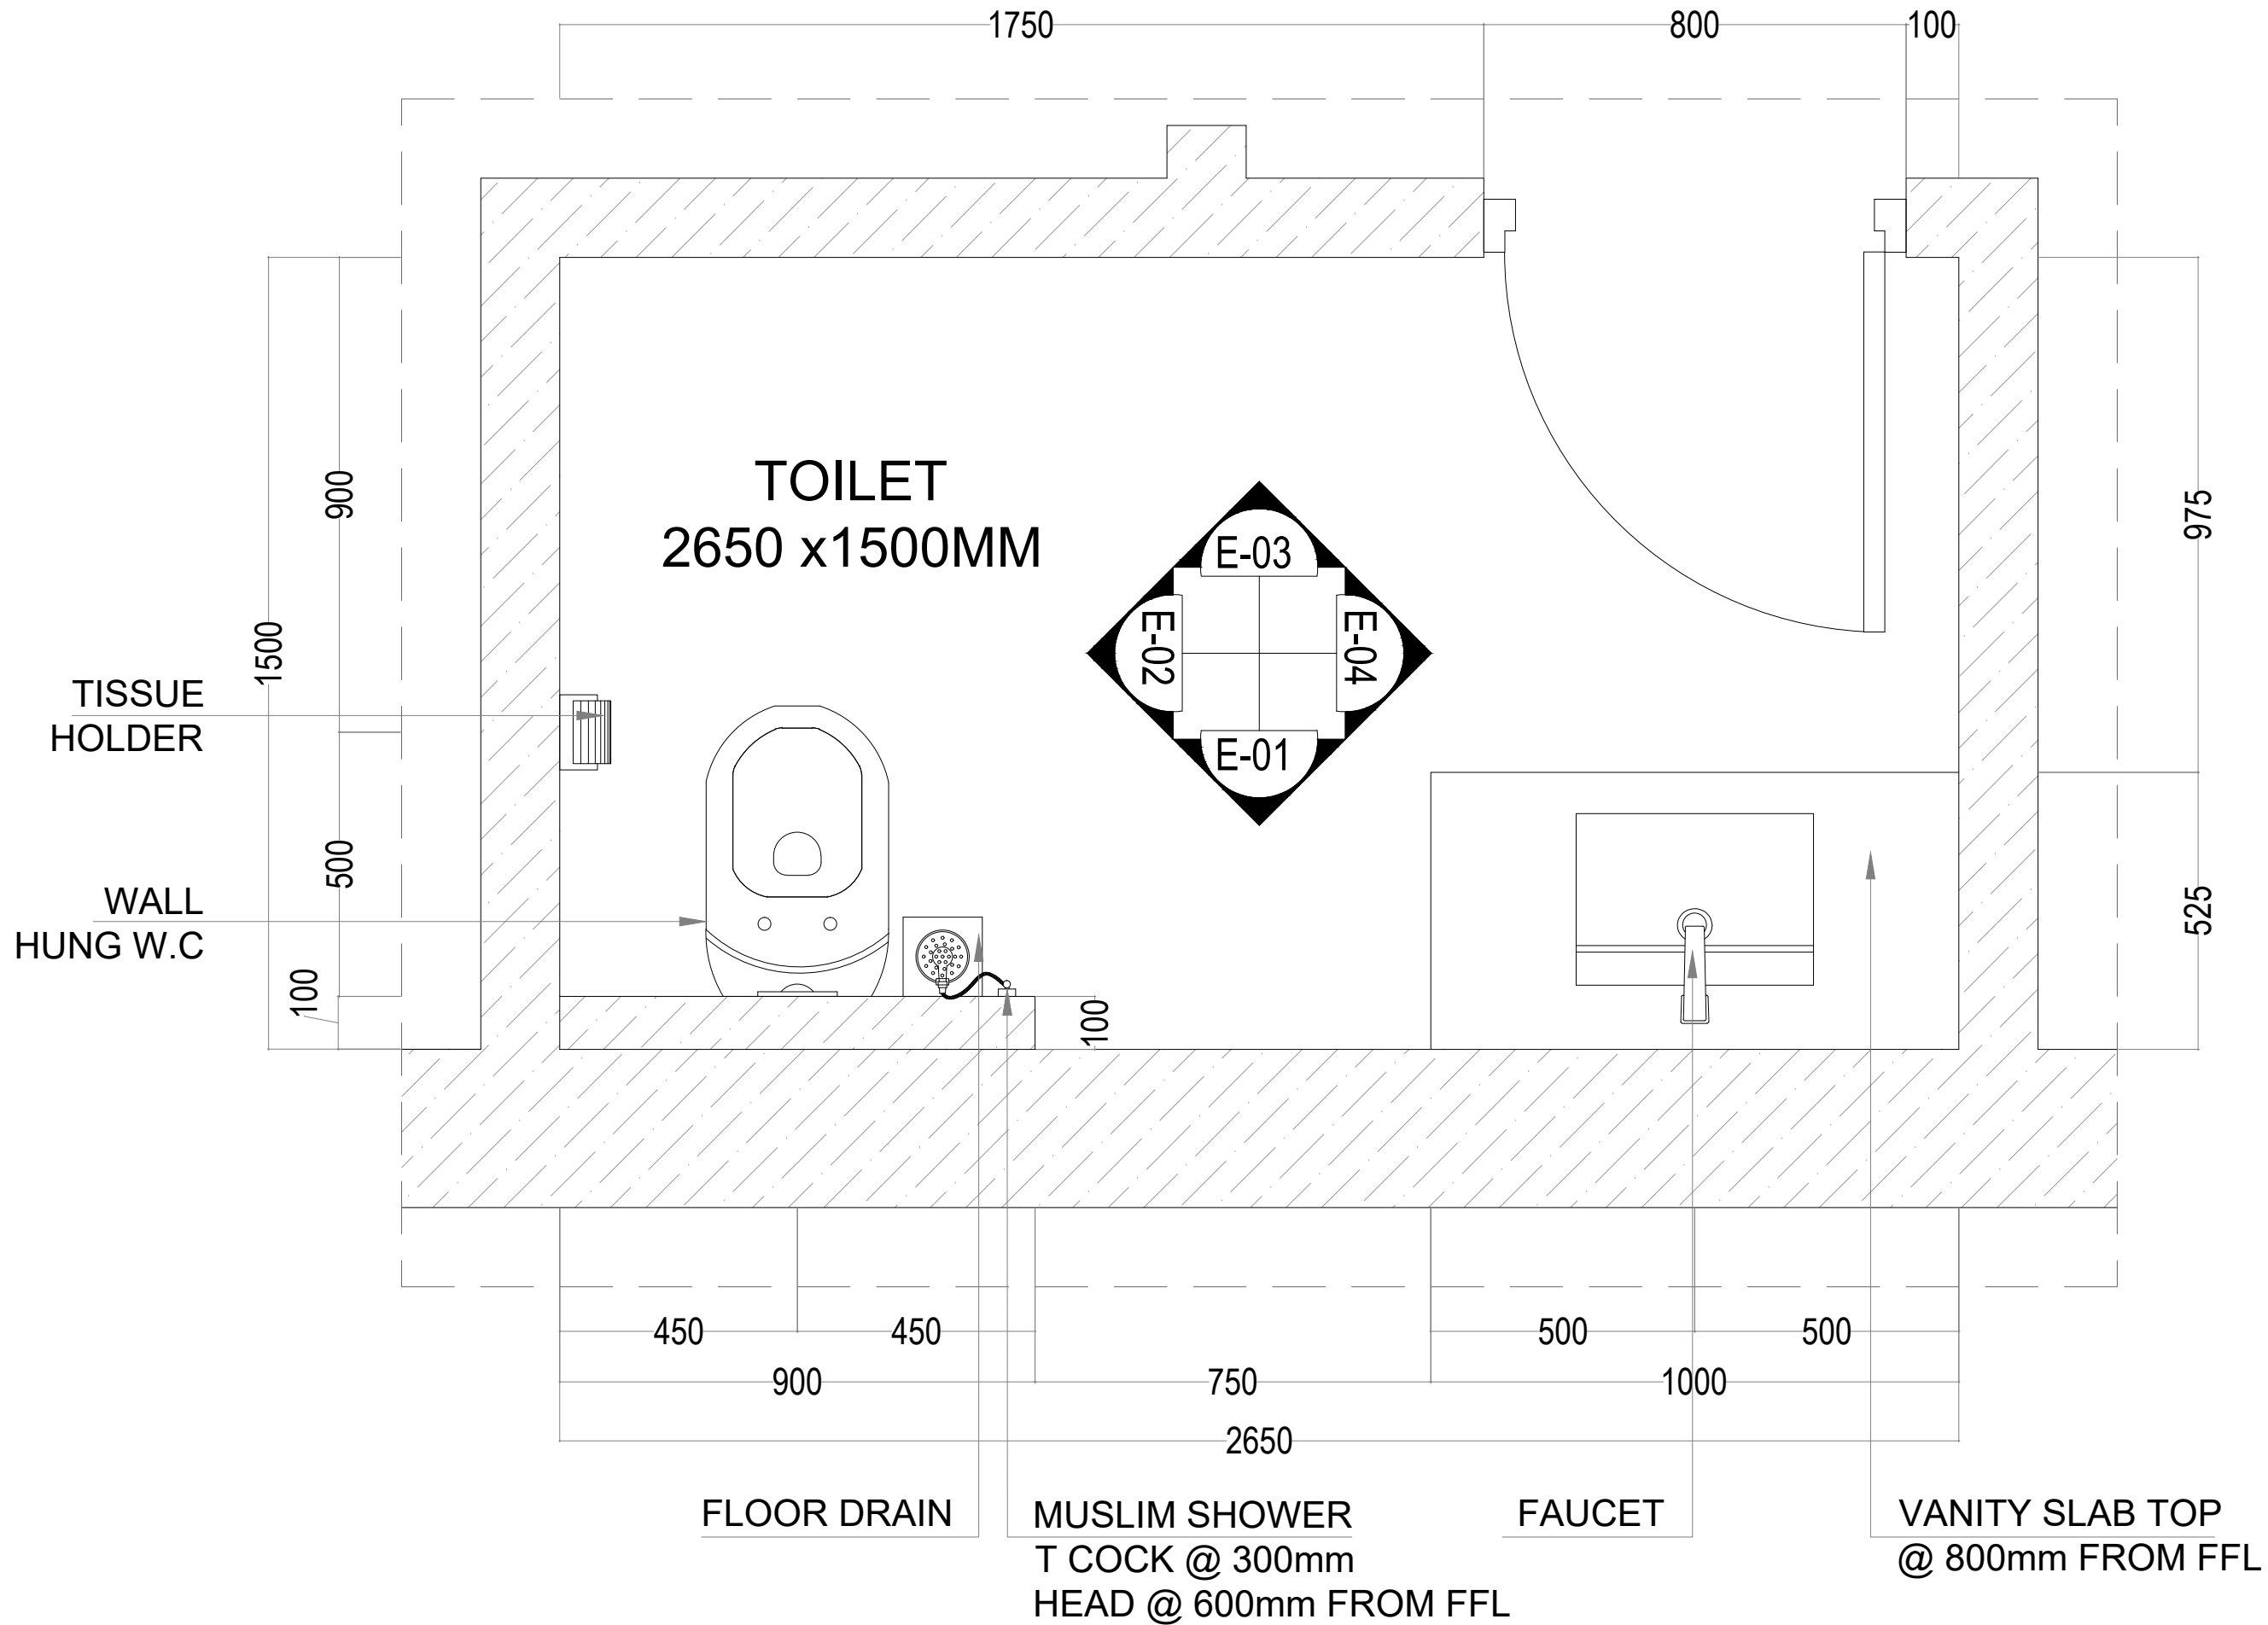

36 ARCLAY CLOSE UB8 3WP
UXBRIDGE LONDON UK
+44 743 8881857

PROJECT NAME:
TASTE OF VILLAGE

OWNER'S NAME:
TASTE OF VILLAGE

PRINCIPAL ARCHITECT;
M.S.
TITLE
TOILET WORKING PLAN

CHECKED BY :
M.S.
DRAWN BY:
FAIZAN ALI

Revised Dates :
Rev. _____
Rev. _____
Rev. _____
Rev. _____
Rev. _____

SCALE:
N.T.S

DATE:
22-10-2025

JOB NO.	DRG NO.
25.1030	ID -25

NOTES:
PRESENTATION
DRAWING NOT FOR
CONSTRUCTION



36 ARCLAY CLOSE UB8 3WP
UXBRIDGE LONDON UK
+44 743 8881857

PROJECT NAME:
TASTE OF VILLAGE

OWNER'S NAME:
TASTE OF VILLAGE

PRINCIPAL ARCHITECT;
M.S.
TITLE
TOILET WORKING ELEVATION-01

CHECKED BY :
M.S.
DRAWN BY:
FAIZAN ALI


Revised Dates :
Rev._____
Rev._____
Rev._____
Rev._____
Rev._____


SCALE:
N.T.S

DATE:
22-10-2025

JOB NO.	DRG NO.
25.1030	ID -26

NOTES:
PRESENTATION
DRAWING NOT FOR
CONSTRUCTION

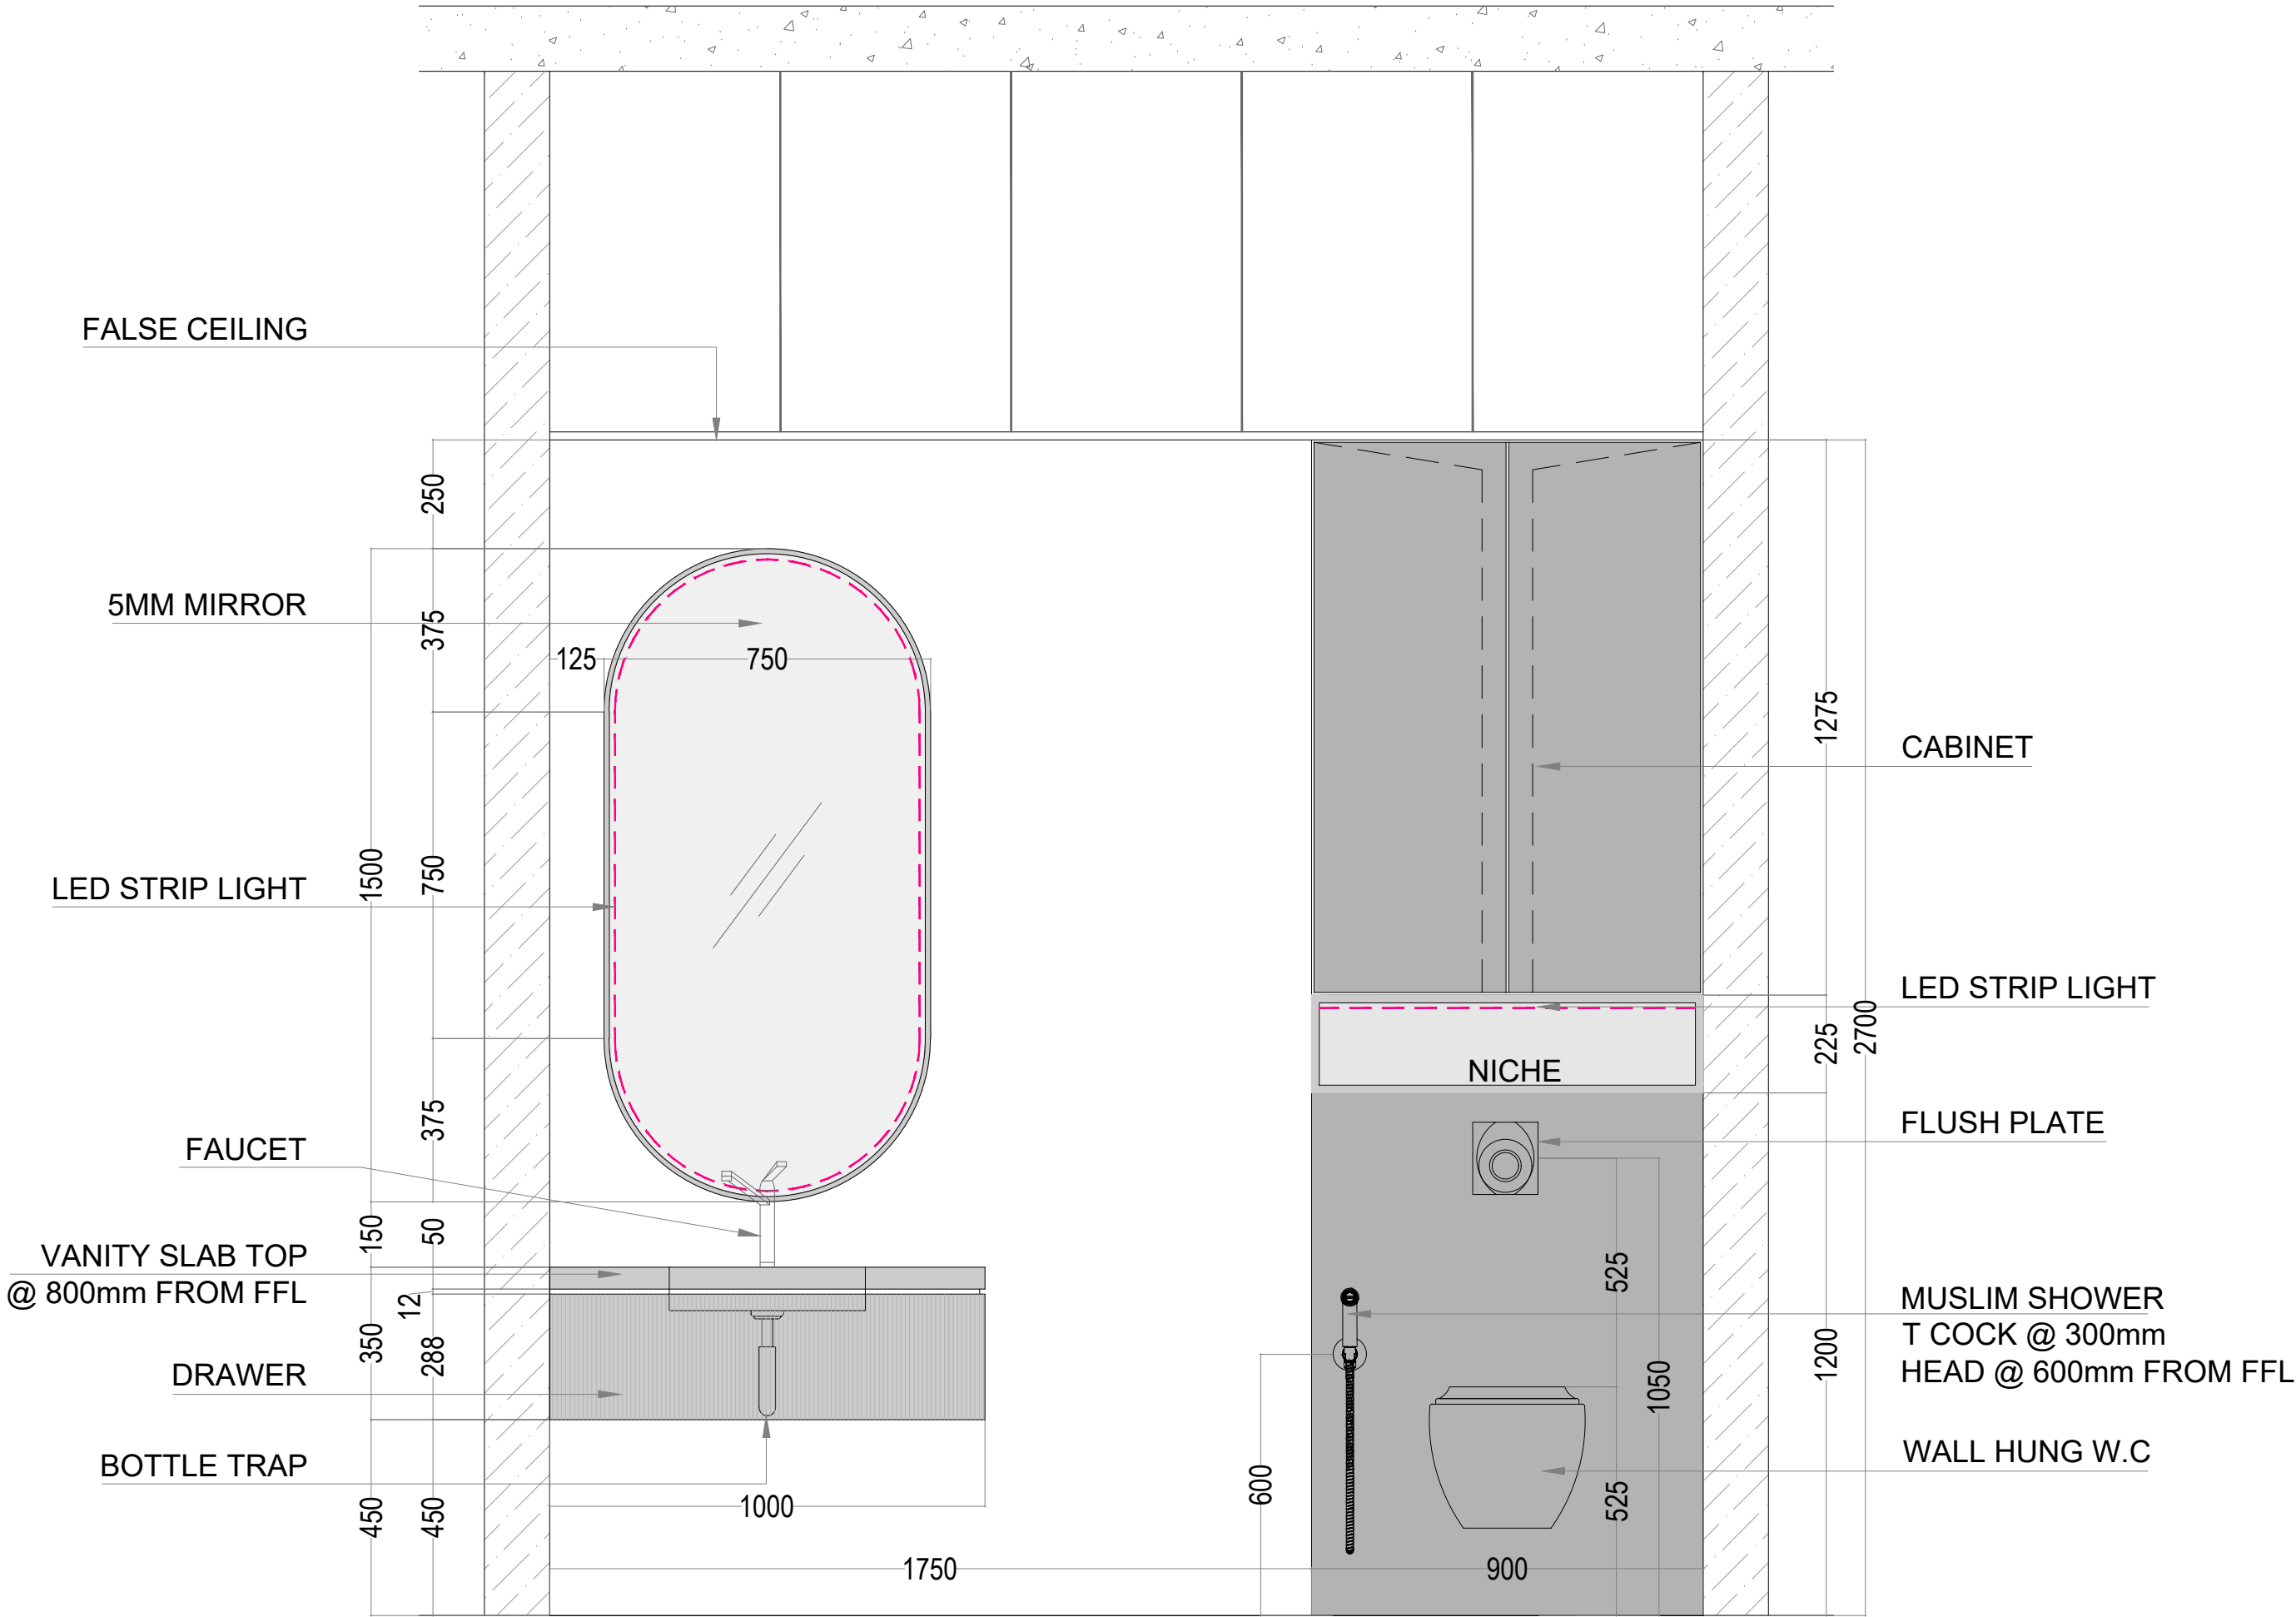

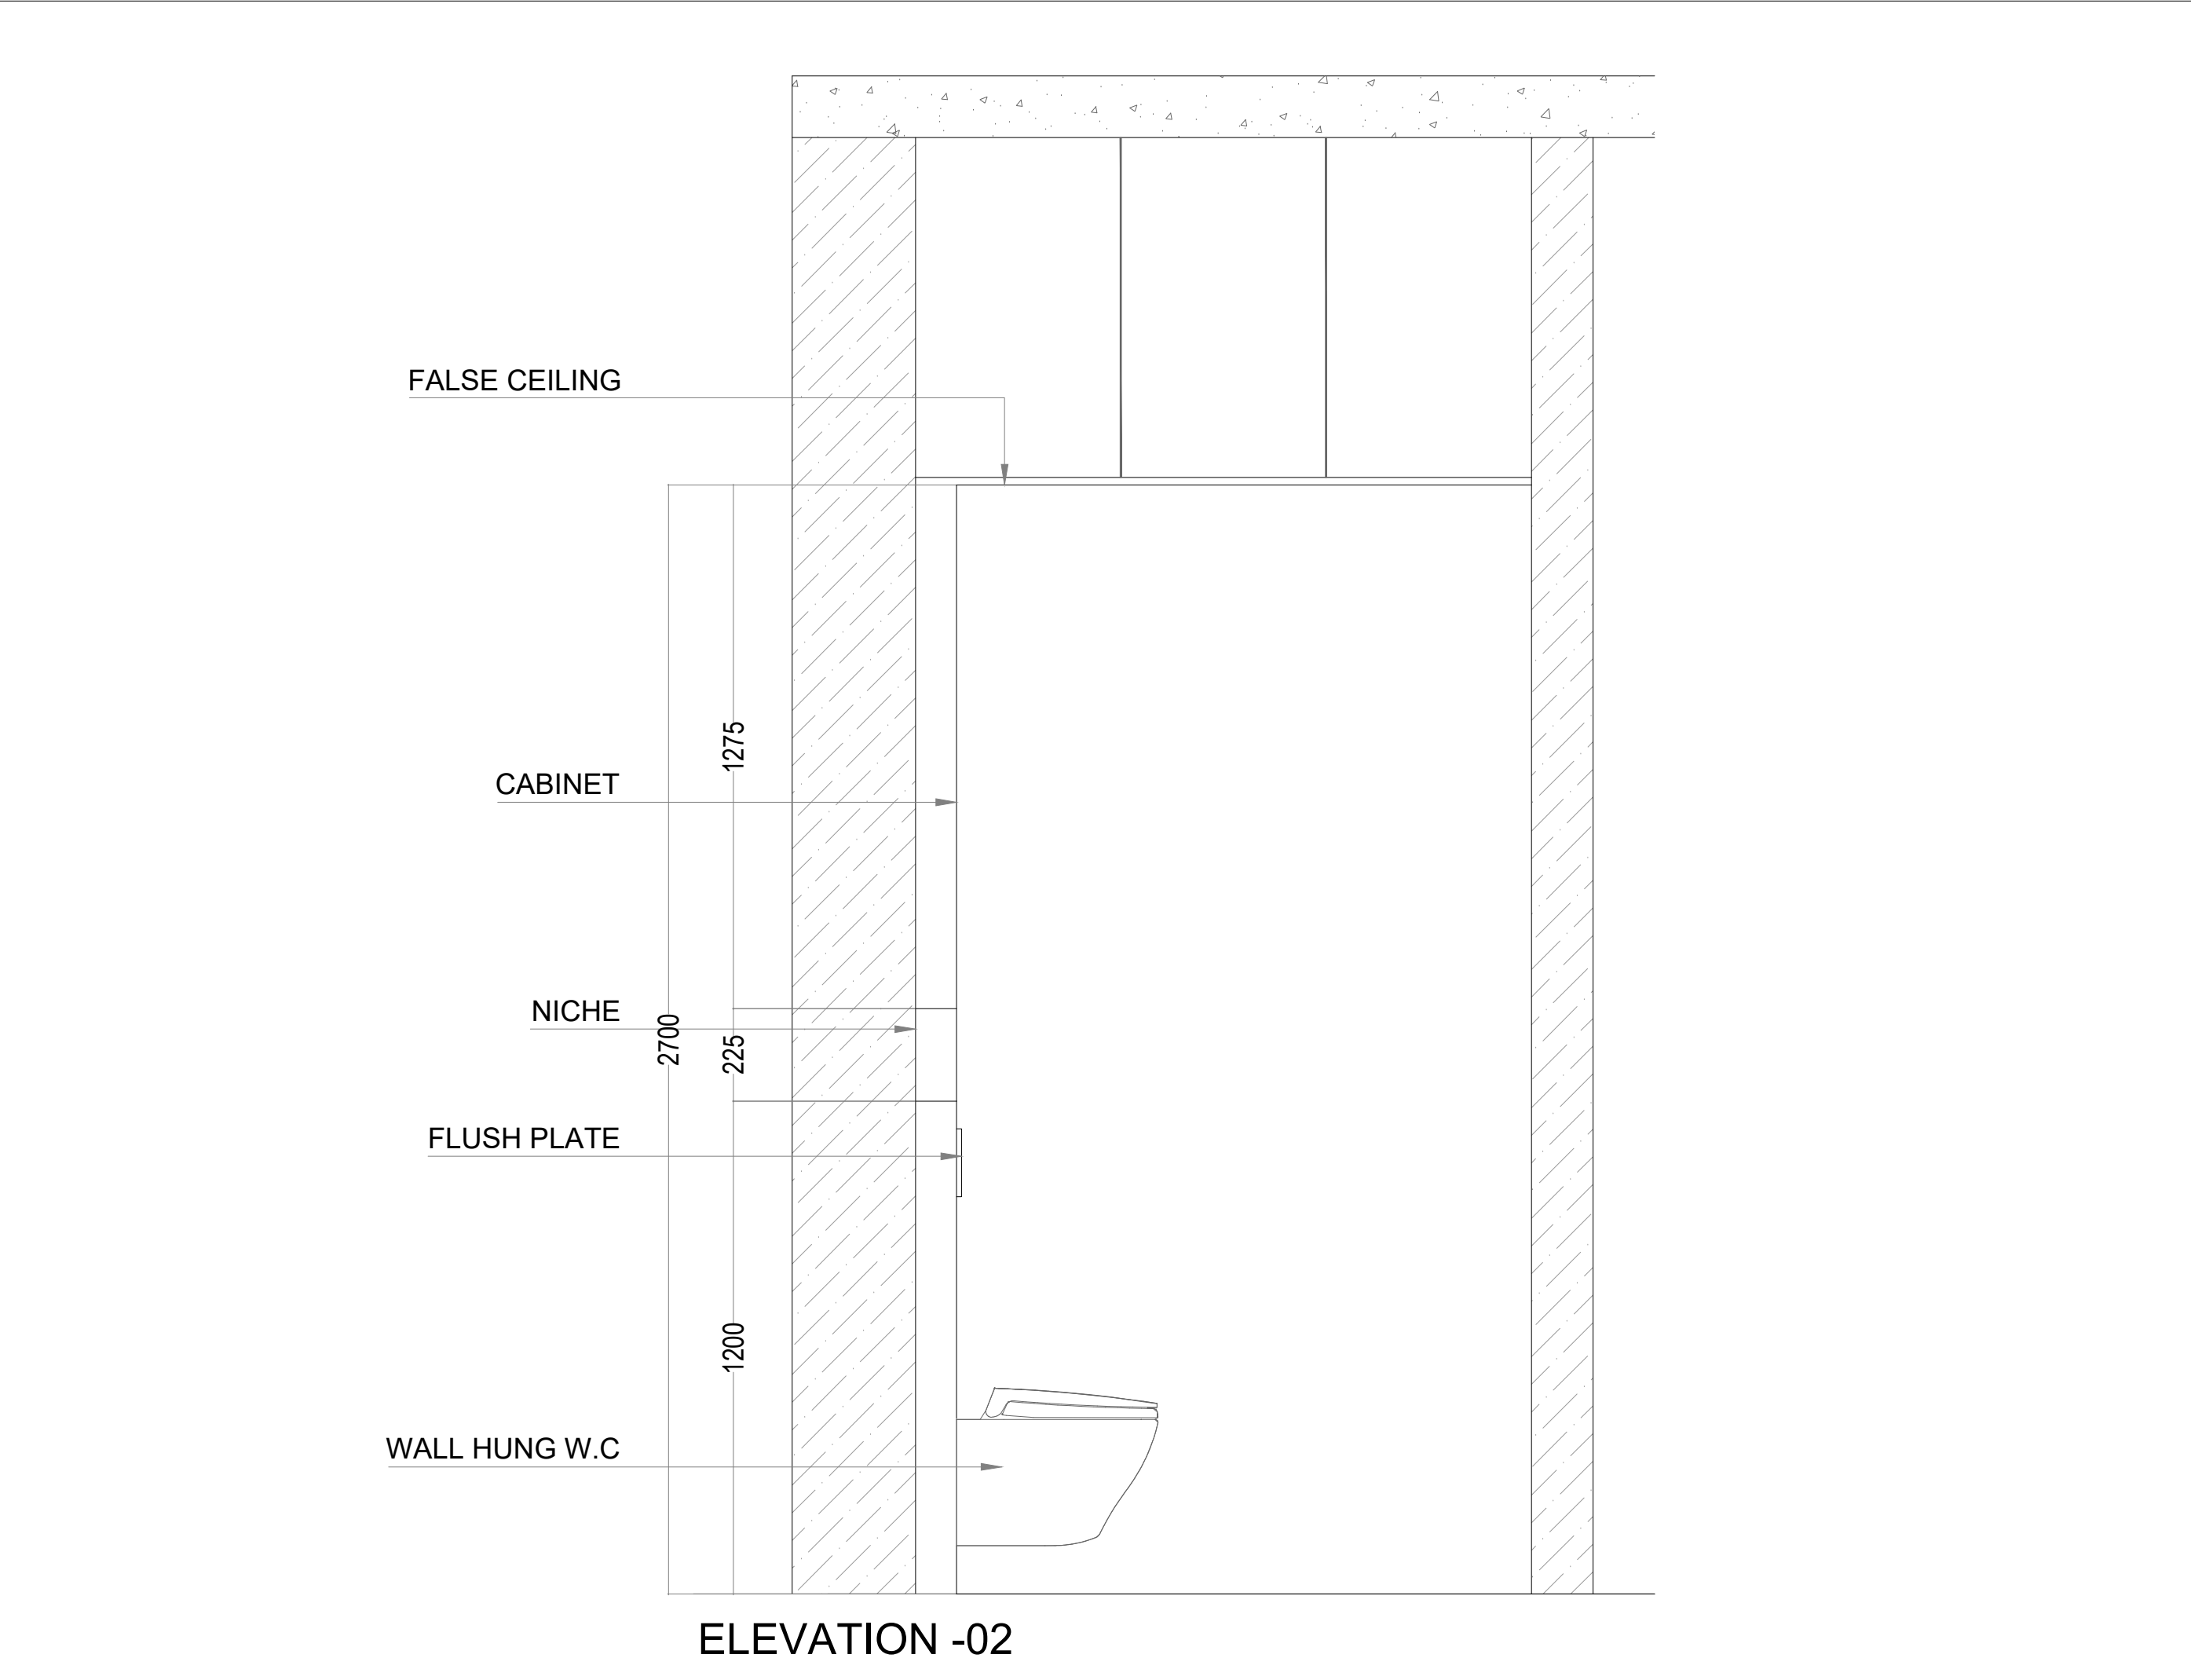

36 ARCLAY CLOSE UB8 3WP
UXBRIDGE LONDON UK
+44 743 8881857

PROJECT NAME:
TASTE OF VILLAGE

OWNER'S NAME:
TASTE OF VILLAGE

PRINCIPAL ARCHITECT;
M.S.

TITLE
TOILET WORKING ELEVATION-02

CHECKED BY :
M.S.
DRAWN BY:
FAIZAN ALI

Revised Dates :
Rev. _____
Rev. _____
Rev. _____
Rev. _____
Rev. _____
Rev. _____


SCALE:
N.T.S

DATE:
22-10-2025

JOB NO.	DRG NO.
25.1030	ID -27

NOTES:

PRESENTATION
DRAWING NOT FOR
CONSTRUCTION

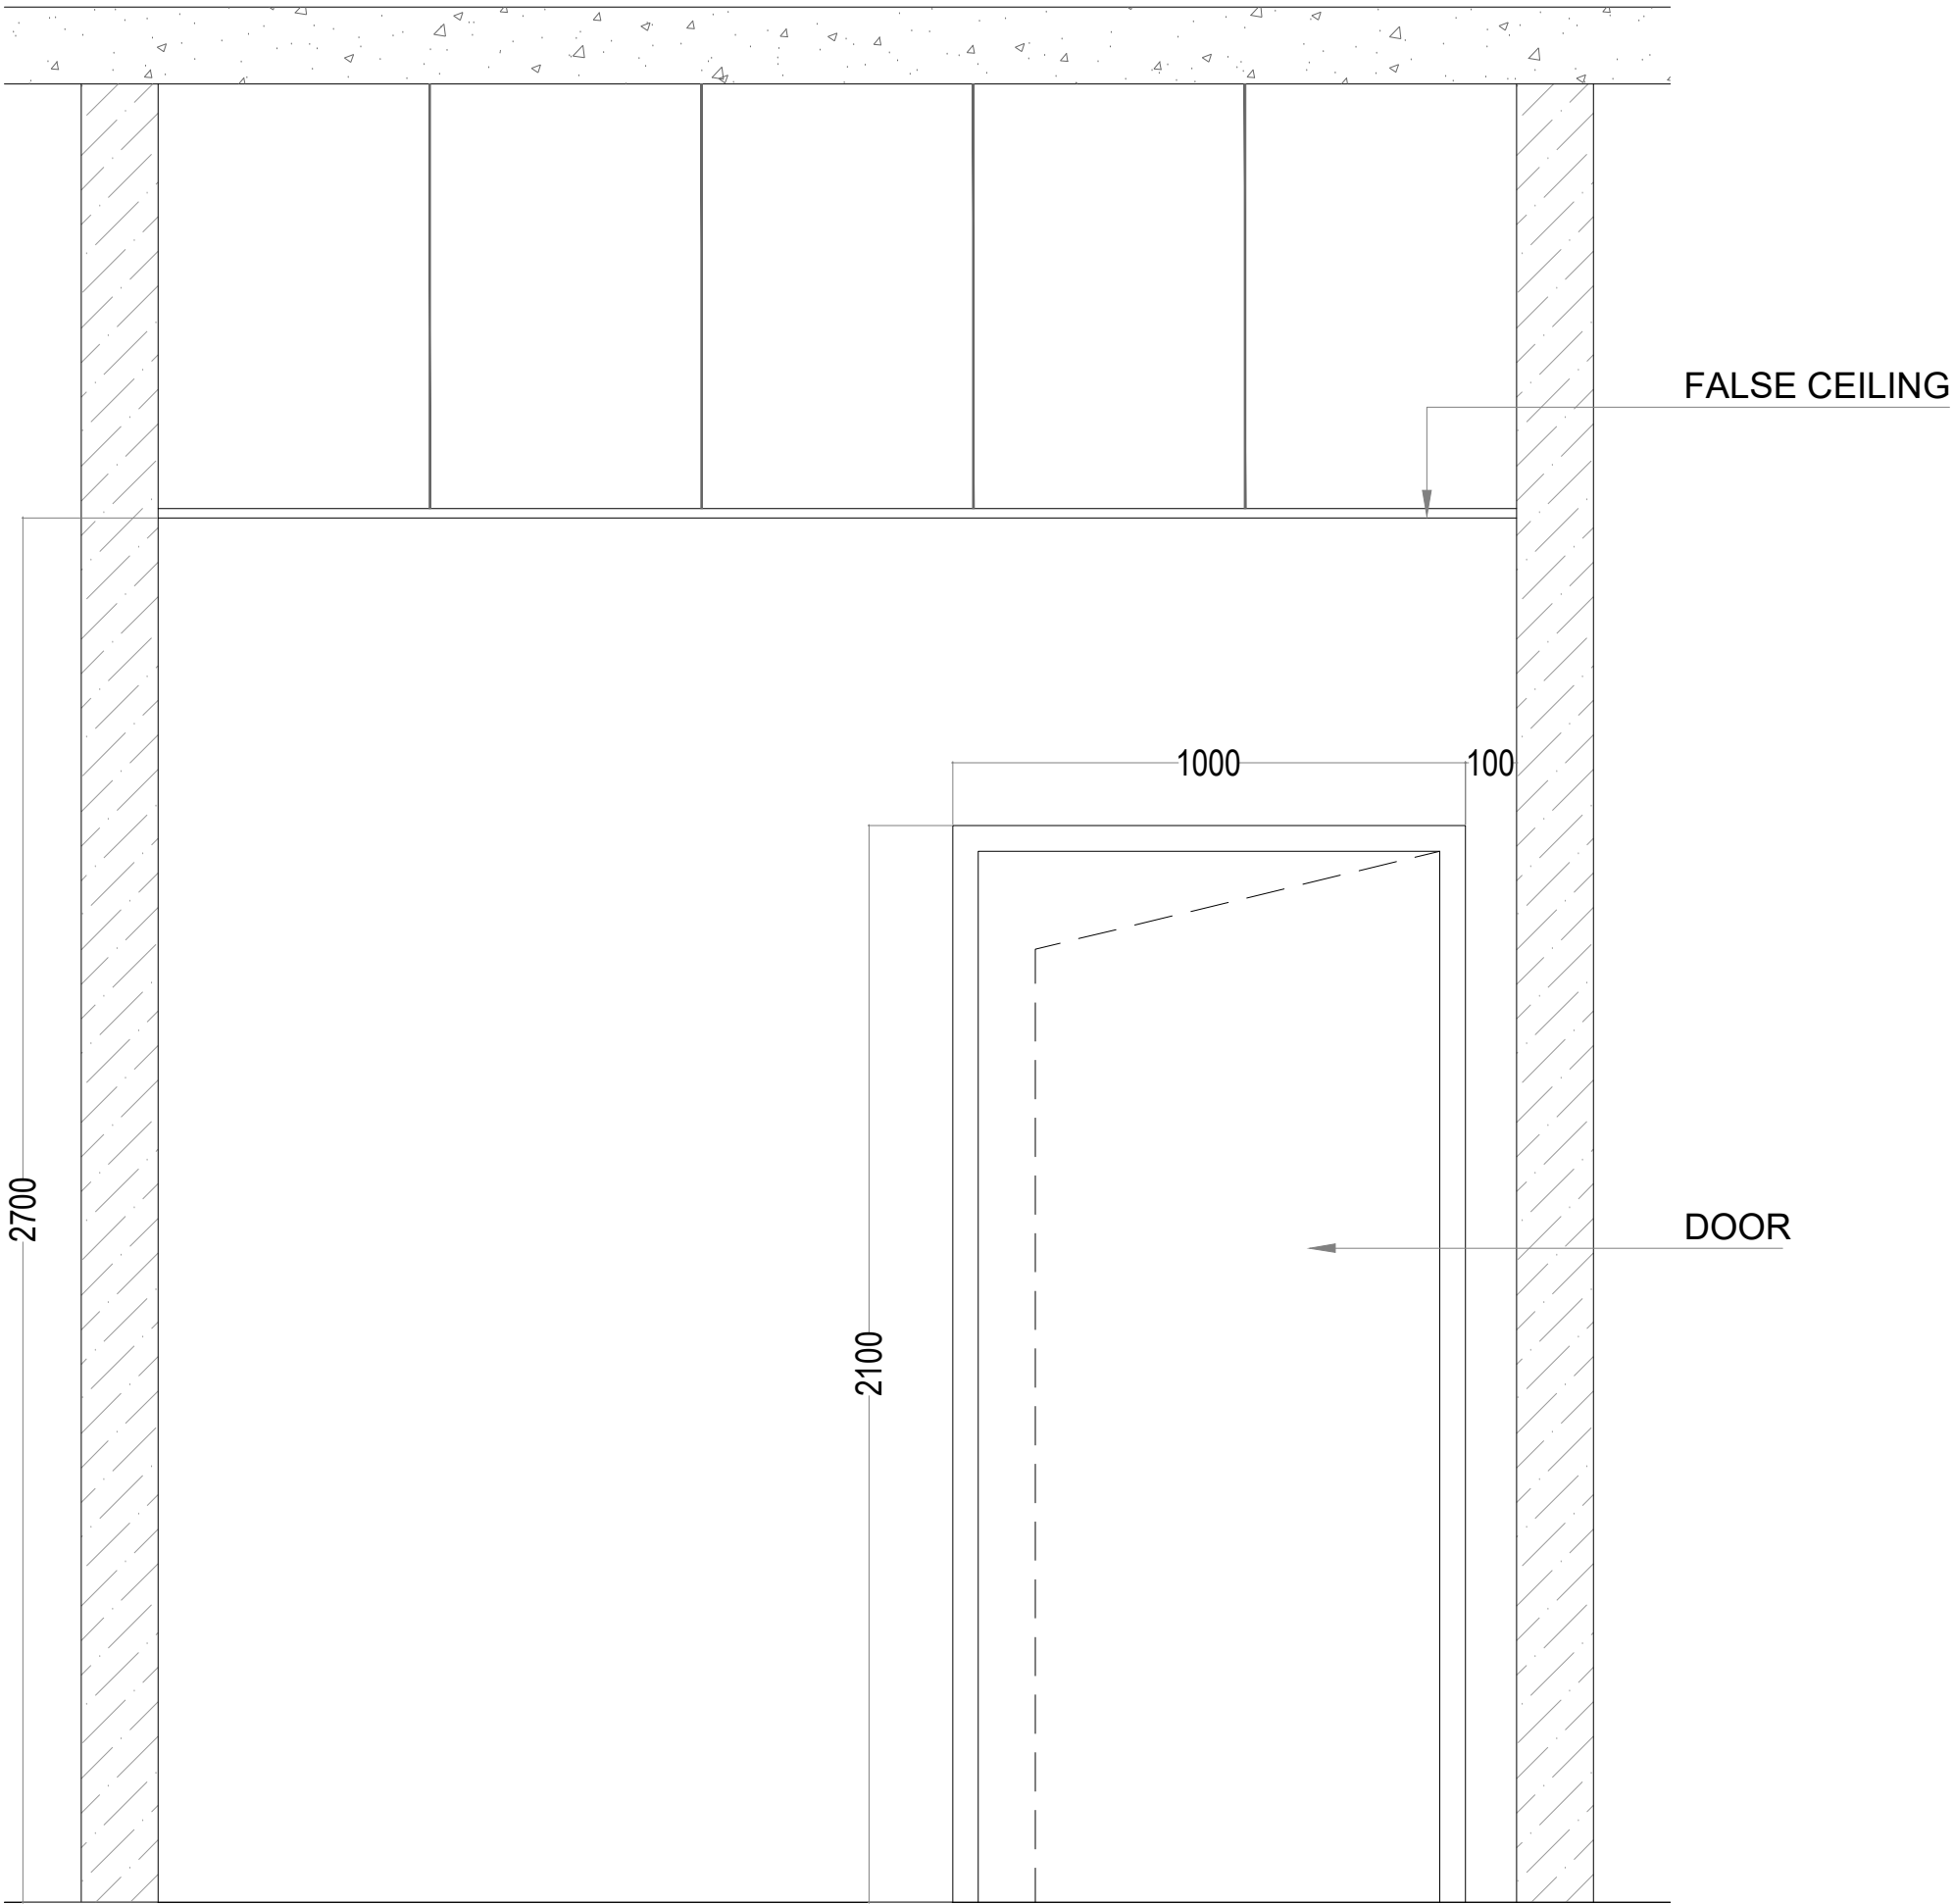

36 ARCLAY CLOSE UB8 3WP
UXBRIDGE LONDON UK
+44 743 8881857

PROJECT NAME:

TASTE OF VILLAGE

OWNER'S NAME:

TASTE OF VILLAGE

PRINCIPAL ARCHITECT;

M.S.

TITLE

TOILET WORKING ELEVATION-03

CHECKED BY :

M.S.

DRAWN BY:

FAIZAN ALI

Revised Dates :

Rev. _____

Rev. _____

Rev. _____

Rev. _____

SCALE:

N.T.S

DATE:

22-10-2025

JOB NO.


25.1030

DRG NO.

ID -28

NOTES:

PRESENTATION
DRAWING NOT FOR
CONSTRUCTION

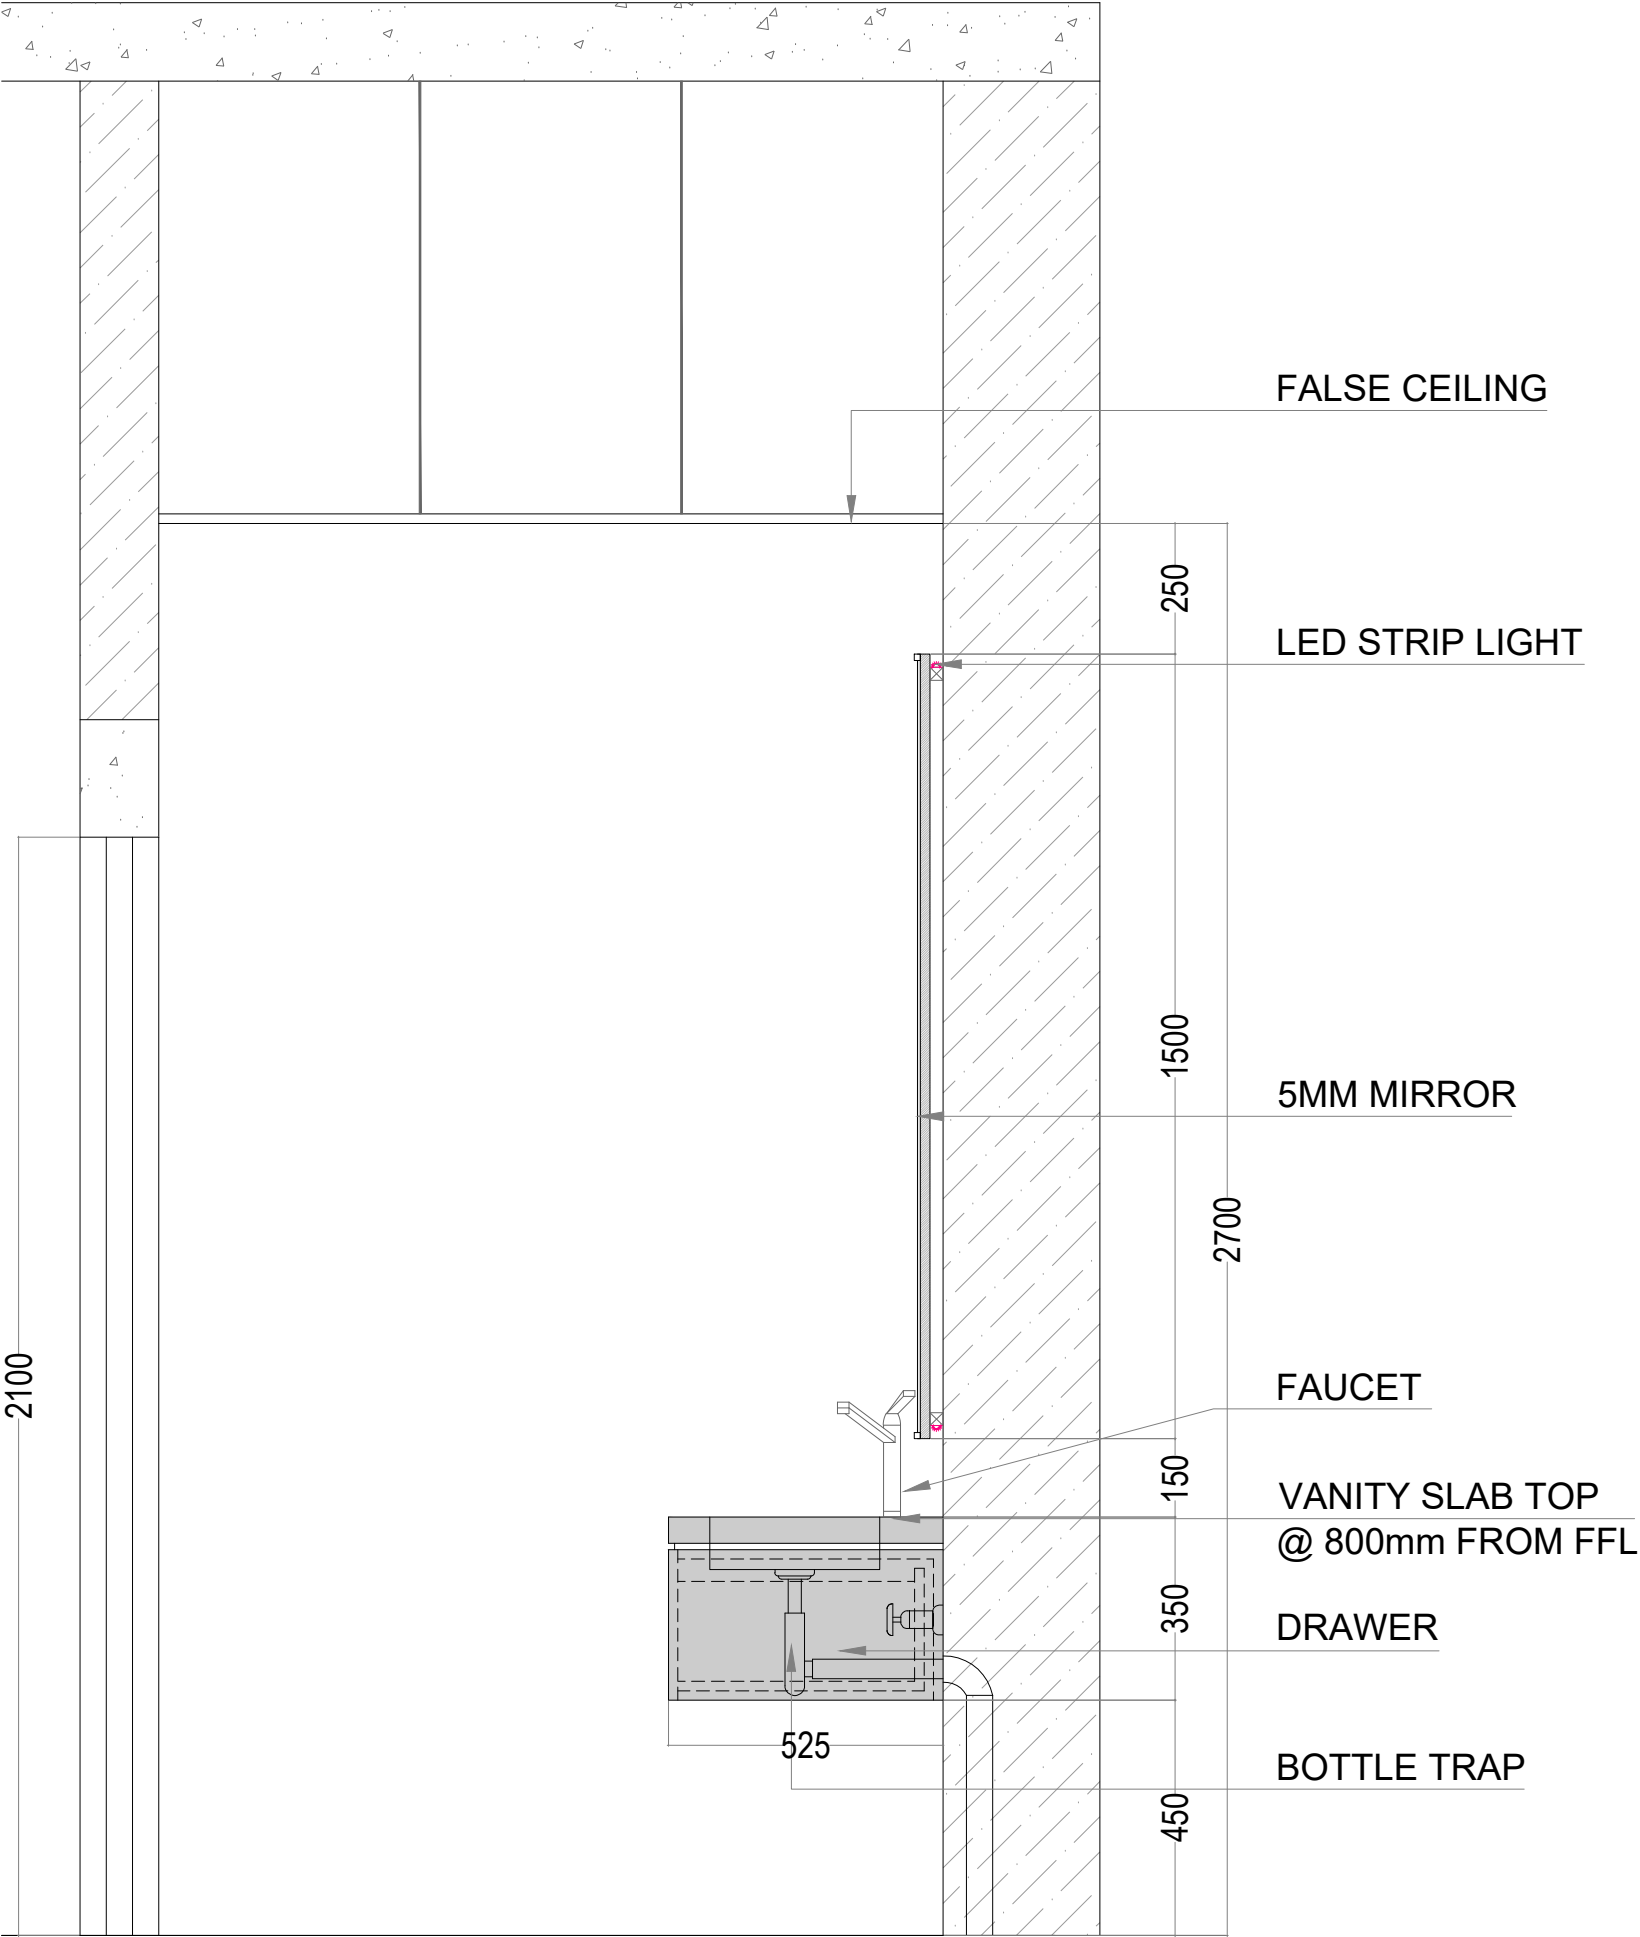

ELEVATION -04



36 ARCLAY CLOSE UB8 3WP
UXBRIDGE LONDON UK
+44 743 8881857

PROJECT NAME:
TASTE OF VILLAGE

OWNER'S NAME:
TASTE OF VILLAGE

PRINCIPAL ARCHITECT;
M.S.
TITLE
TOILET WORKING ELEVATION-04

CHECKED BY :
M.S.
DRAWN BY:
FAIZAN ALI

Revised Dates :
Rev. _____
Rev. _____
Rev. _____
Rev. _____
Rev. _____
Rev. _____

SCALE:
N.T.S

DATE:
22-10-2025

JOB NO.	DRG NO.
25.1030	ID -29

NOTES:
PRESENTATION
DRAWING NOT FOR
CONSTRUCTION



36 ARCLAY CLOSE UB8 3WP
UXBRIDGE LONDON UK
+44 743 8881857

PROJECT NAME:
TASTE OF VILLAGE

OWNER'S NAME:
TASTE OF VILLAGE

PRINCIPAL ARCHITECT;

M.S.
TITLE
TOILET TILE LAYOUT PLAN

CHECKED BY :

M.S.
DRAWN BY:
FAIZAN ALI
Revised Dates :
Rev _____
Rev _____
Rev _____
Rev _____
Rev _____


SCALE:
N.T.S

DATE:
22-10-2025

JOB NO.	DRG NO.
25.1030	ID -30

NOTES:

PRESENTATION
DRAWING NOT FOR
CONSTRUCTION

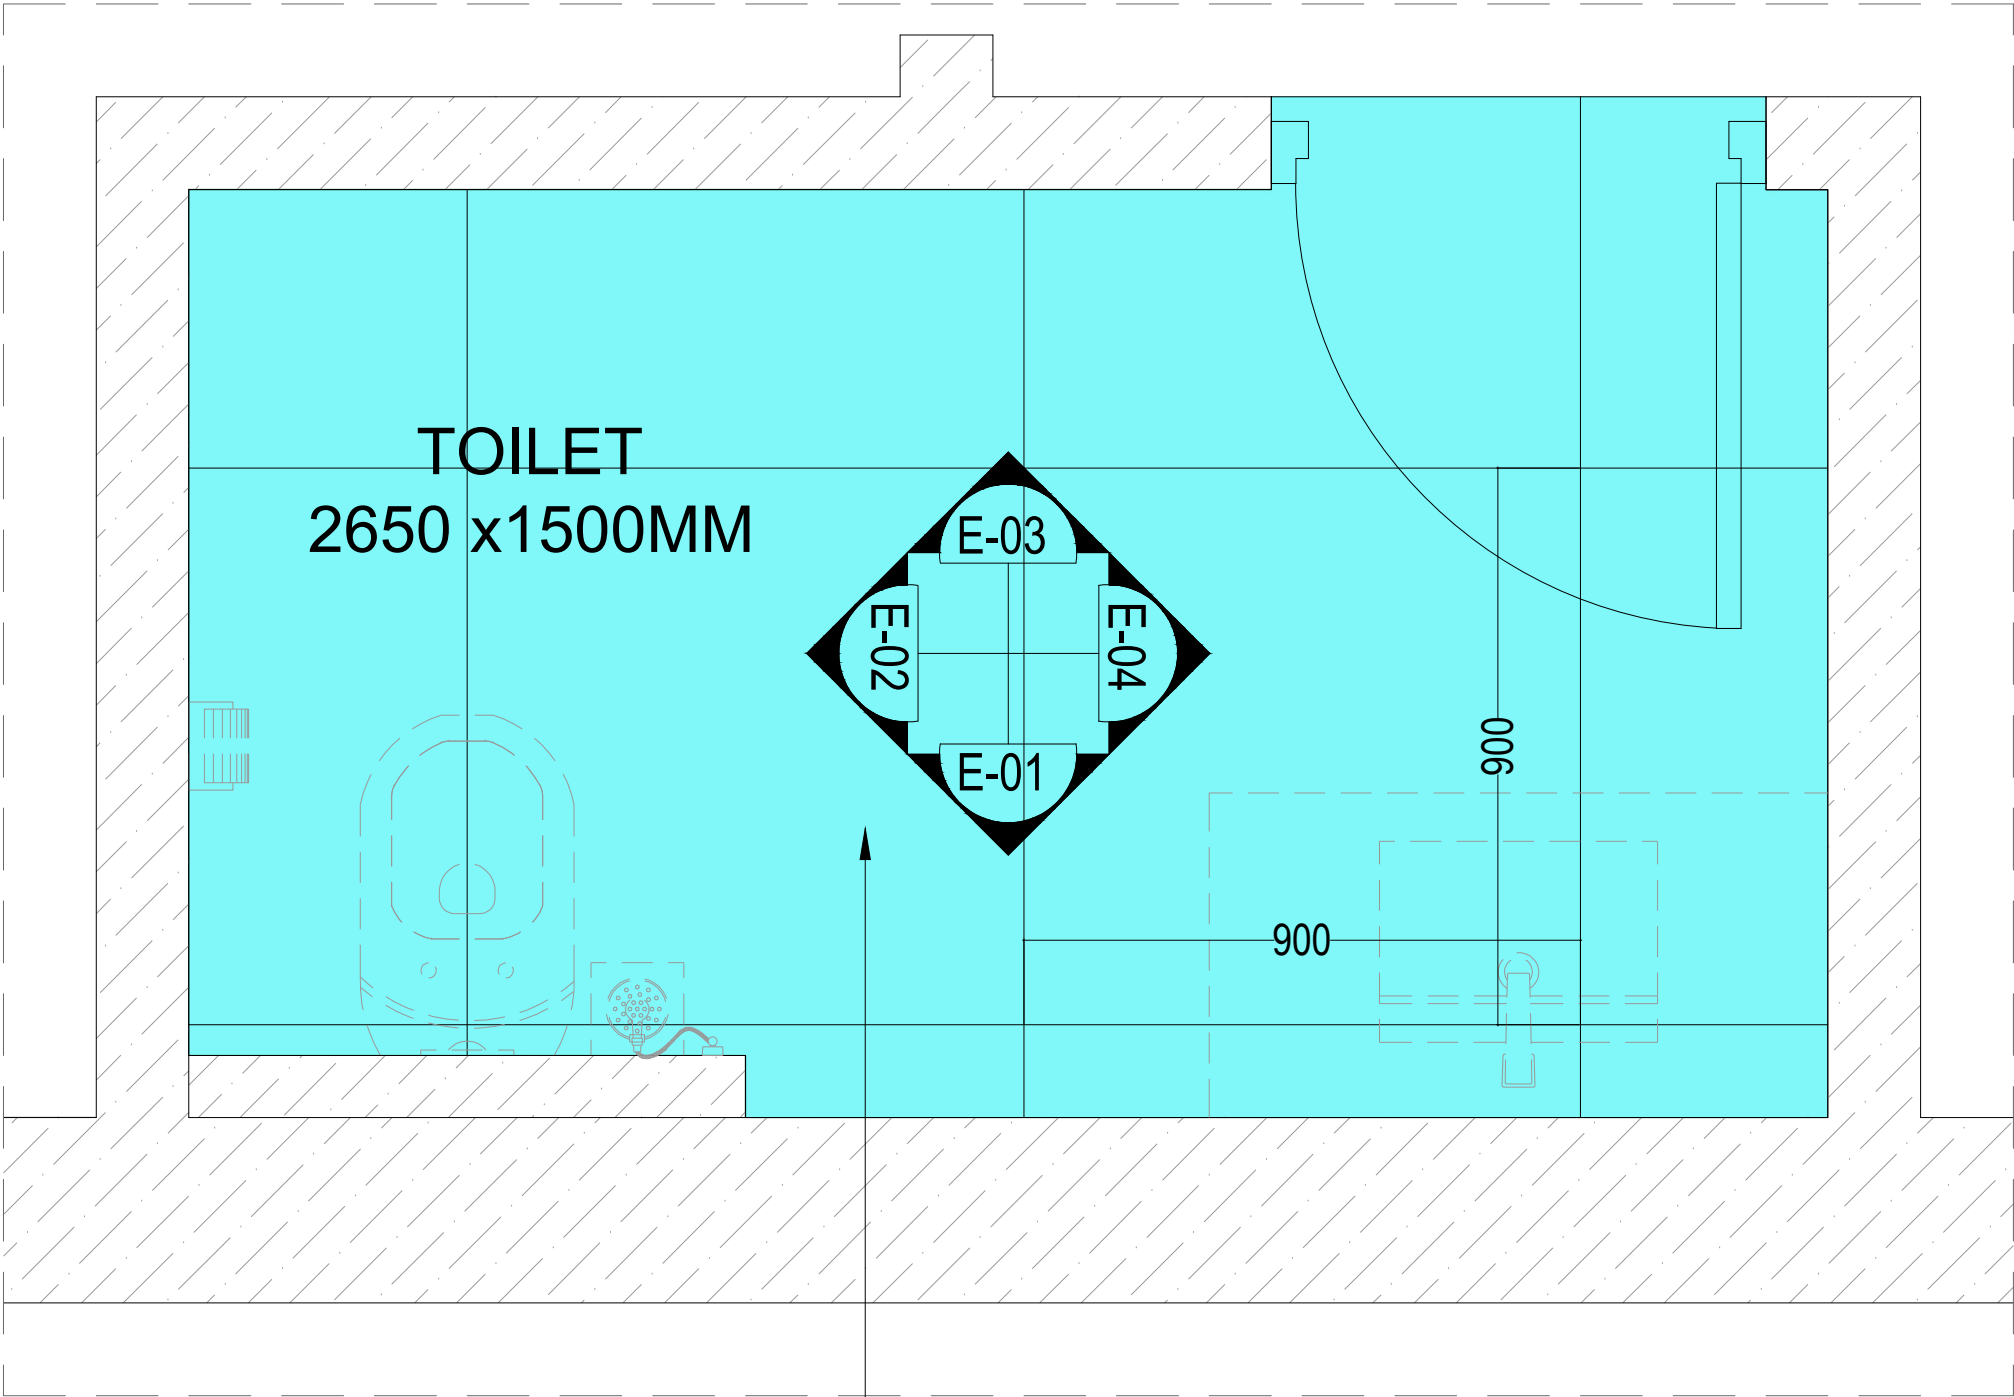

VOLTE BEECH WOVEN WOOD EFFECT
MATT PORCELAIN FLOOR TILE (900 x 900mm)



36 ARCLAY CLOSE UB8 3WP
UXBRIDGE LONDON UK
+44 743 8881857

PROJECT NAME:

TASTE OF VILLAGE

OWNER'S NAME:

TASTE OF VILLAGE

PRINCIPAL ARCHITECT;
M.S.
TITLE
TOILET TILE LAYOUT ELEVATION-01

CHECKED BY :	
M.S.	
DRAWN BY:	
FAIZAN ALI	

Revised Dates :
Rev.....
Rev.....
Rev.....
Rev.....
Rev.....


SCALE:
N.T.S


DATE:
22-10-2025

JOB NO.	DRG NO.
25.1030	ID -31

NOTES:

PRESENTATION
DRAWING NOT FOR
CONSTRUCTION

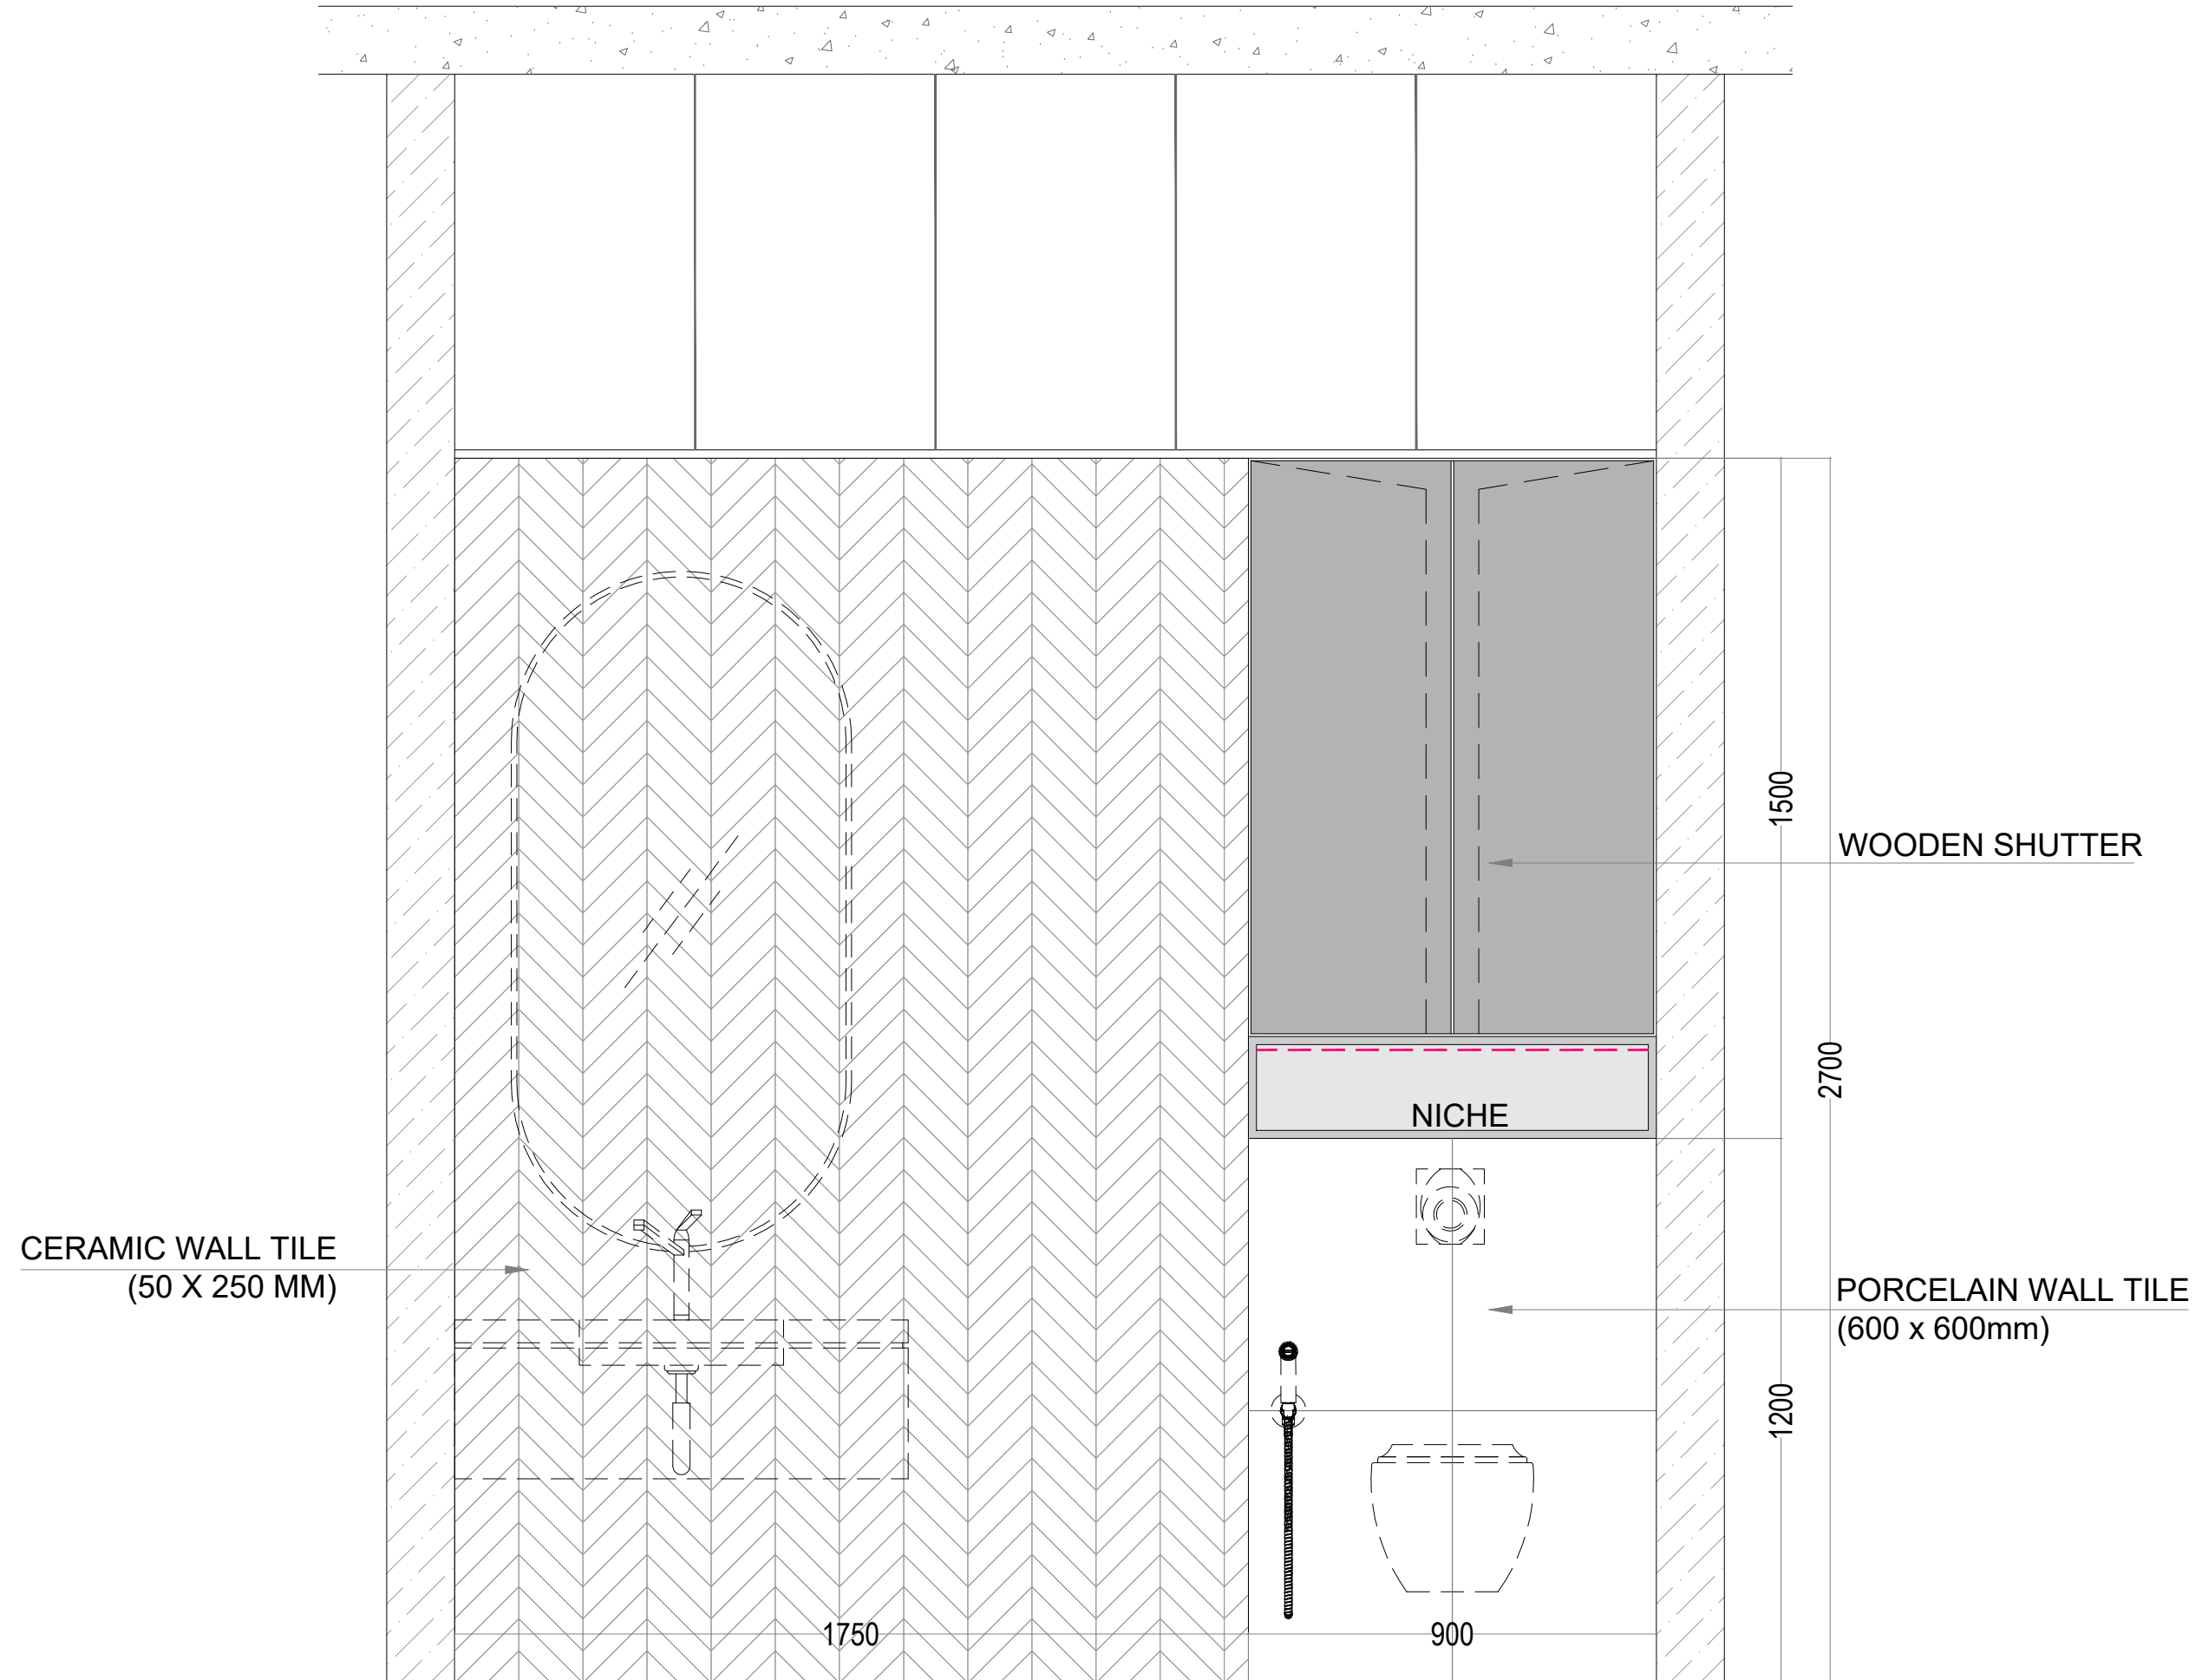

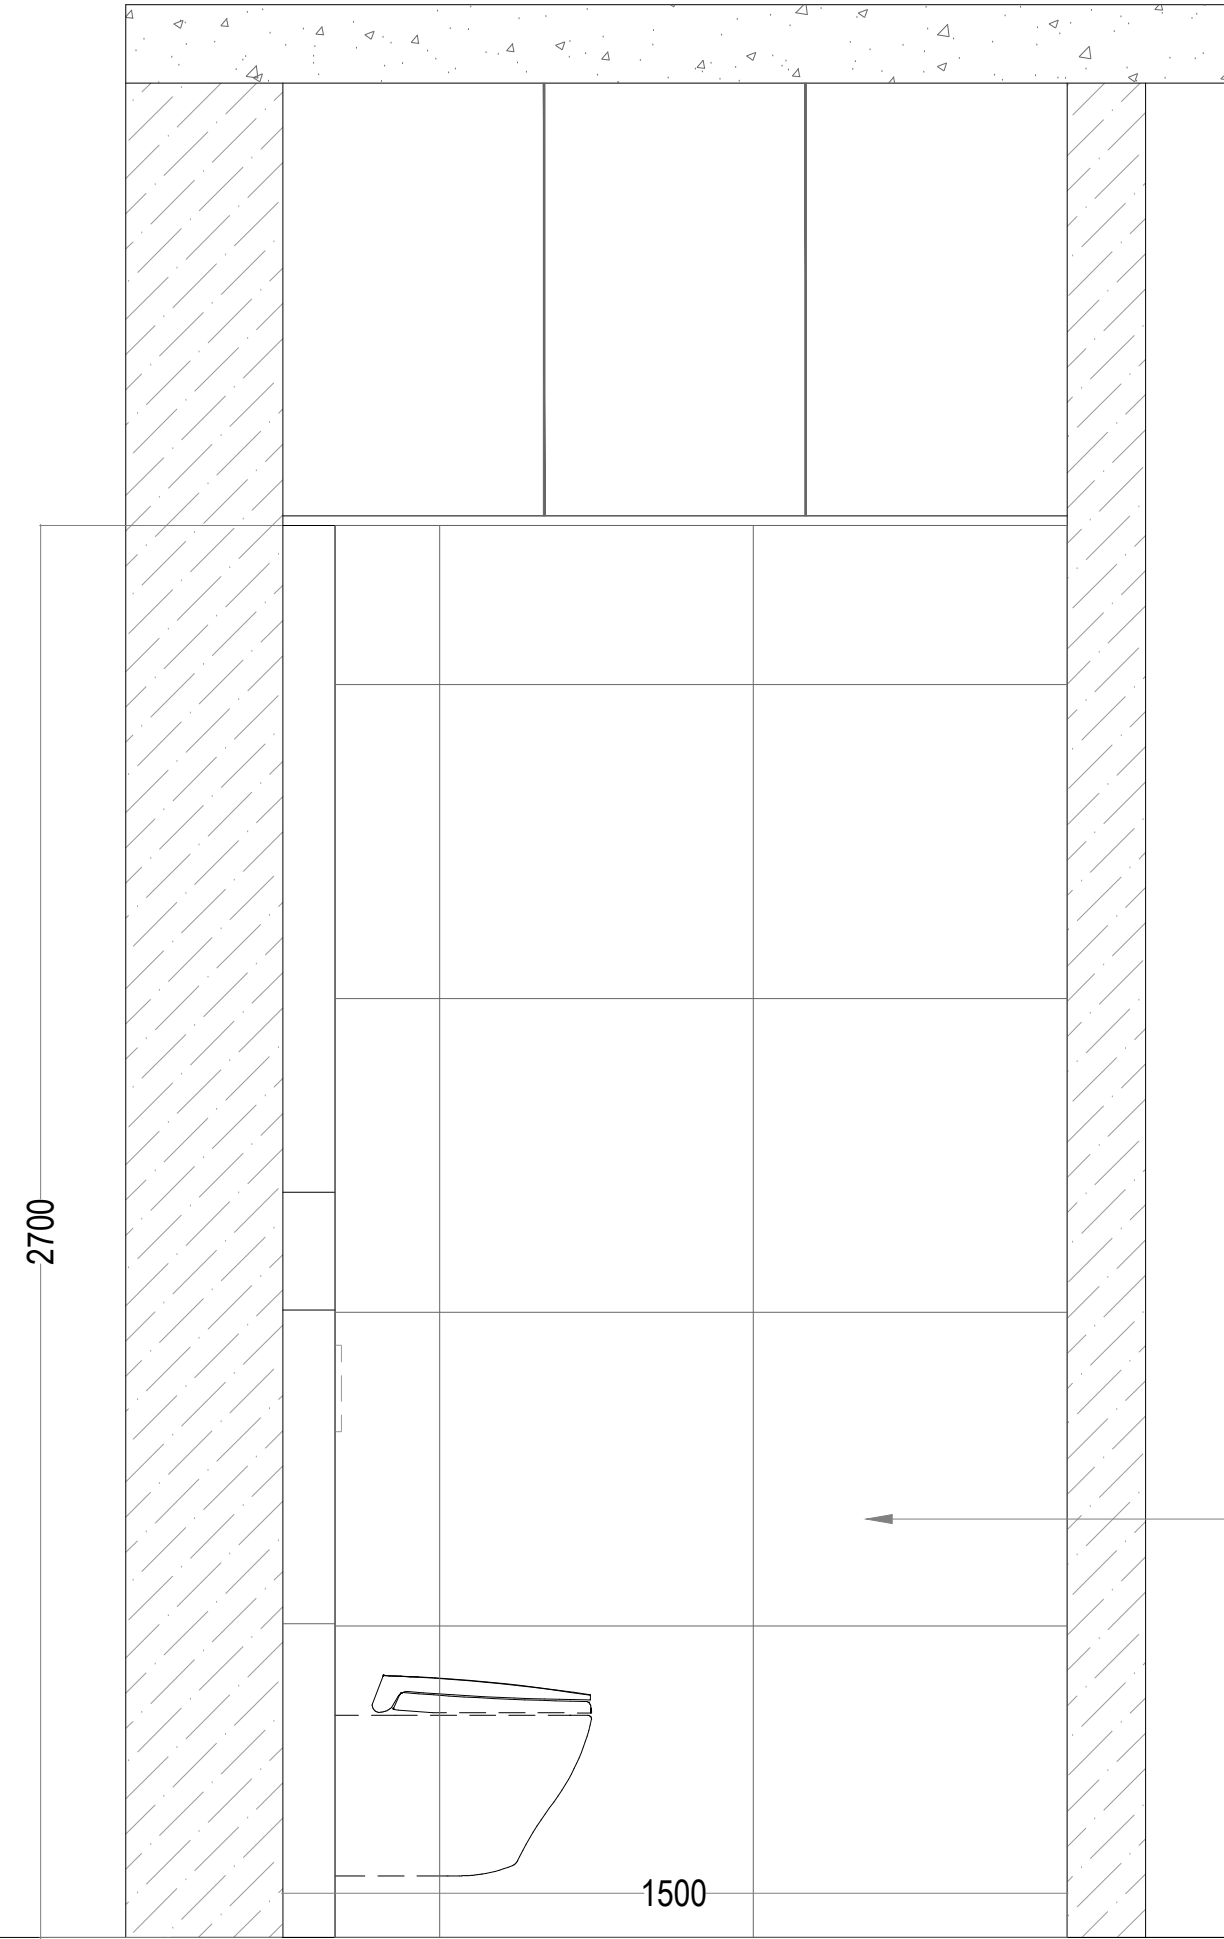

ELEVATION -02



36 ARCLAY CLOSE UB8 3WP
UXBRIDGE LONDON UK
+44 743 8881857

PROJECT NAME:
TASTE OF VILLAGE

OWNER'S NAME:
TASTE OF VILLAGE

PRINCIPAL ARCHITECT;

M.S.
TITLE
TOILET TILE LAYOUT ELEVATION-02

CHECKED BY :

M.S.
DRAWN BY:
FAIZAN ALI

Revised Dates :
Rev. _____
Rev. _____
Rev. _____
Rev. _____
Rev. _____
Rev. _____


SCALE:
N.T.S

DATE:
22-10-2025

JOB NO. 25.1030	DRG NO. ID -32
--------------------	-------------------

NOTES:

PRESENTATION
DRAWING NOT FOR
CONSTRUCTION

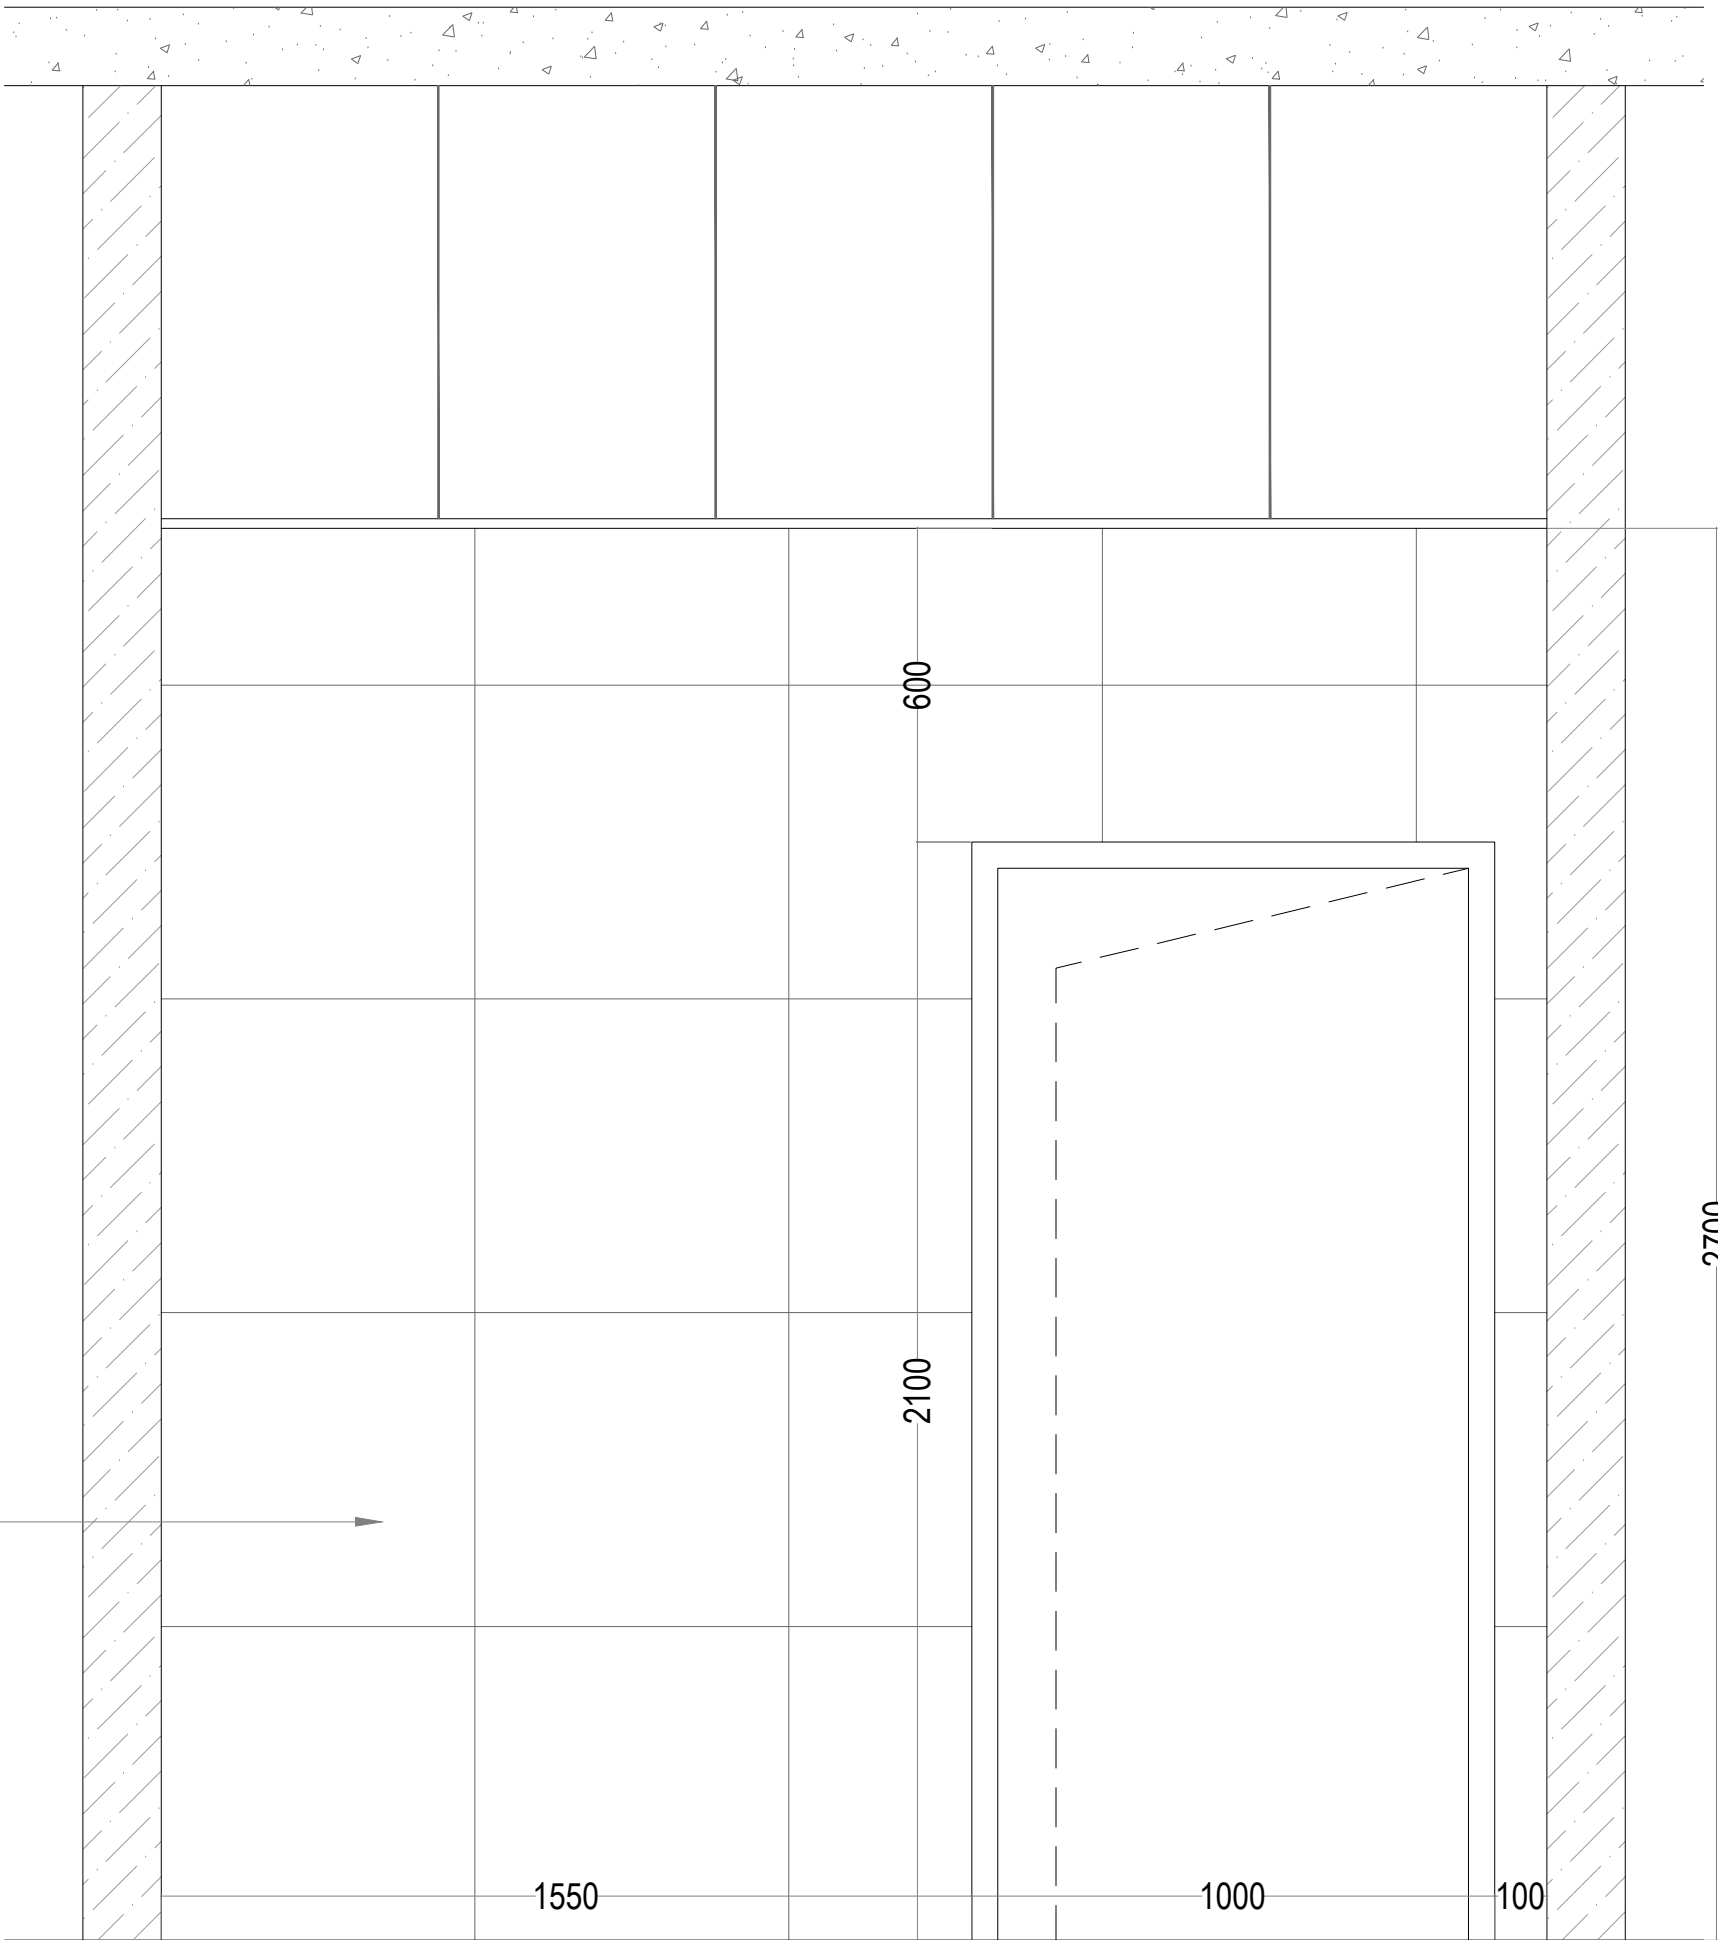

PORCELAIN WALL TILE
(600 x 600mm)

ELEVATION -03



36 ARCLAY CLOSE UB8 3WP
UXBRIDGE LONDON UK
+44 743 8881857

PROJECT NAME:
TASTE OF VILLAGE

OWNER'S NAME:
TASTE OF VILLAGE

PRINCIPAL ARCHITECT;
M.S.
TITLE
TOILET TILE LAYOUT ELEVATION-03

CHECKED BY :
M.S.
DRAWN BY:
FAIZAN ALI

Revised Dates :
Rev. _____
Rev. _____
Rev. _____
Rev. _____
Rev. _____
Rev. _____


SCALE:
N.T.S

DATE:
22-10-2025

JOB NO.	DRG NO.
25.1030	ID -33

NOTES:

PRESENTATION
DRAWING NOT FOR
CONSTRUCTION

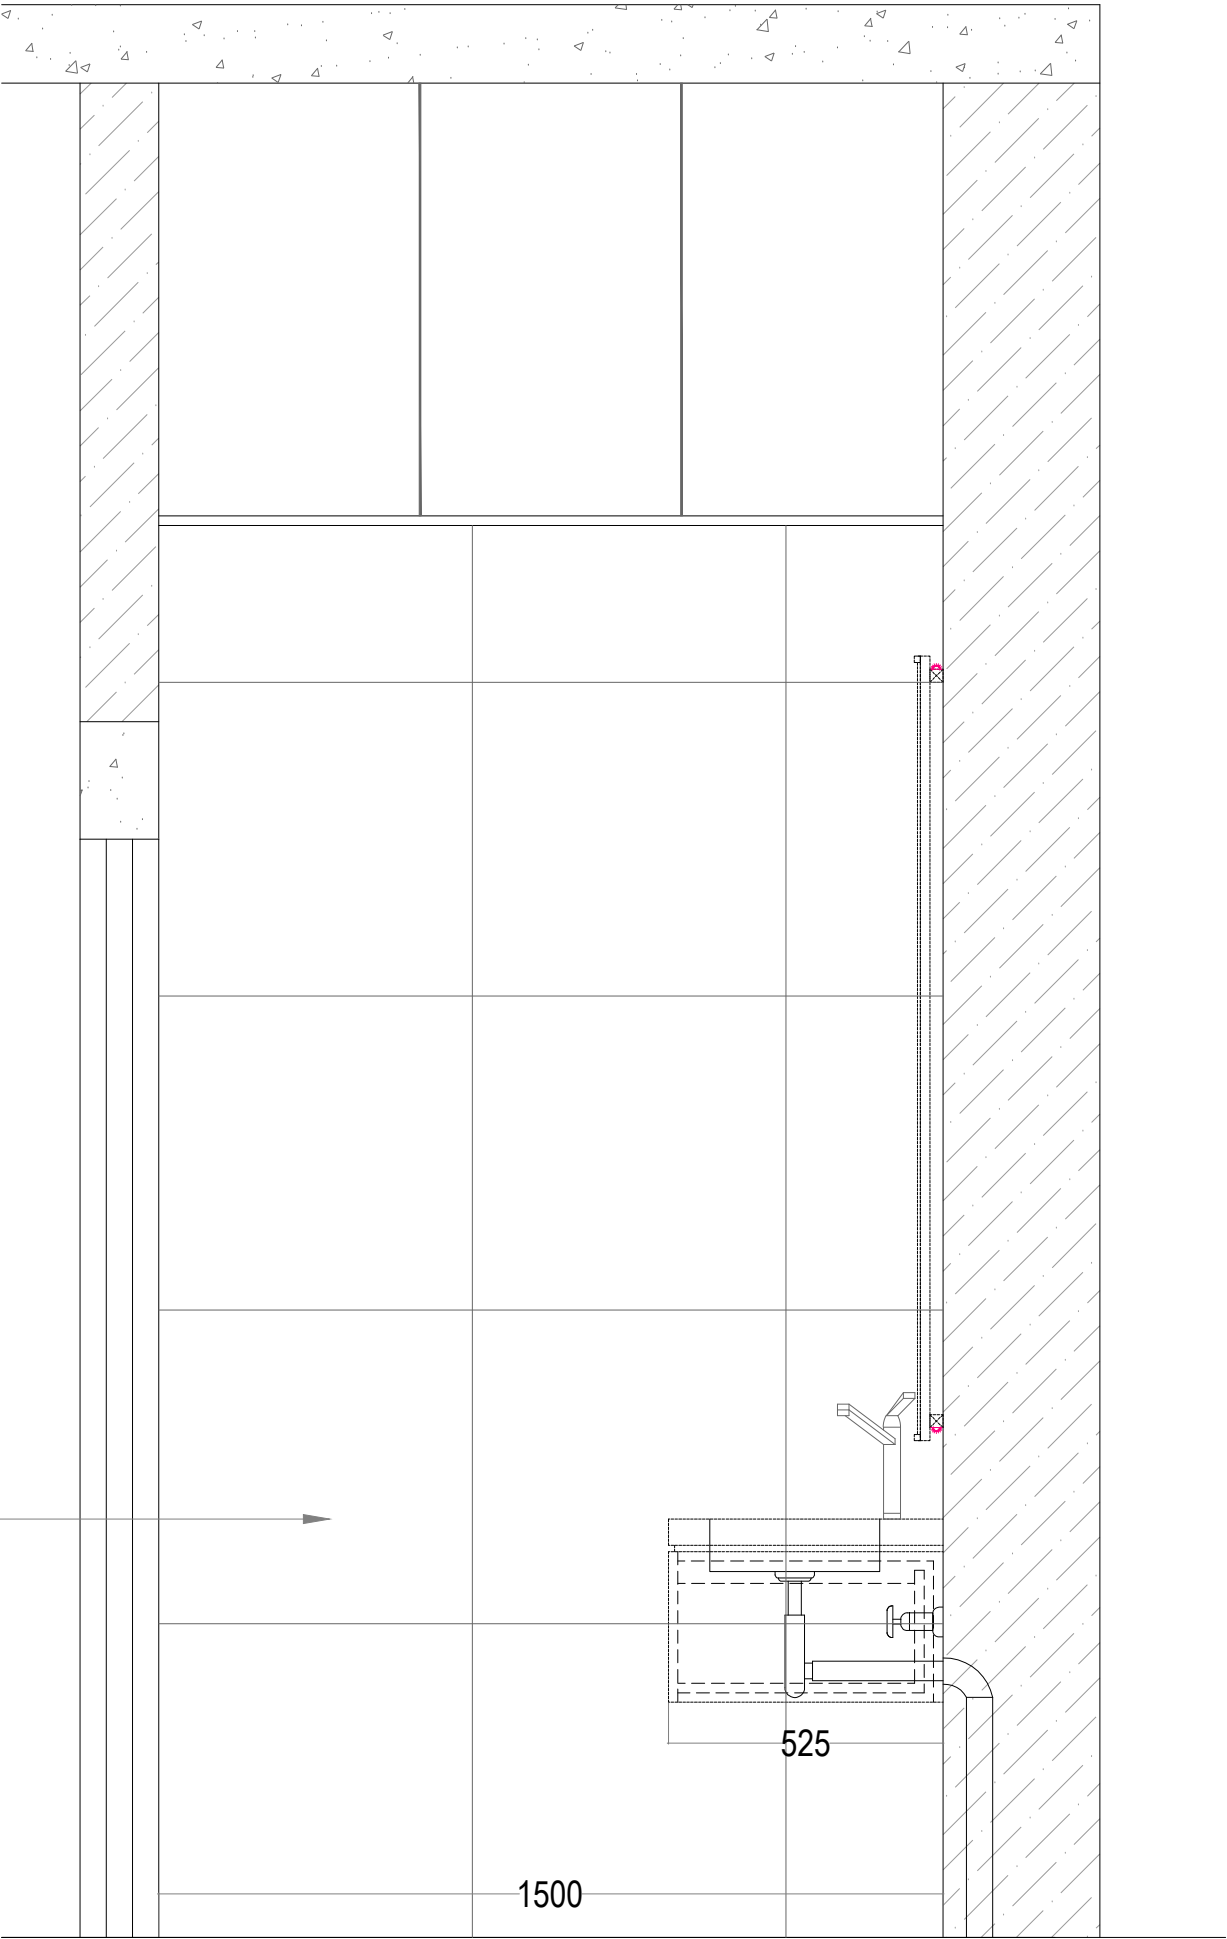

PORCELAIN WALL TILE
(600 x 600mm)

ELEVATION -04



36 ARCLAY CLOSE UB8 3WP
UXBRIDGE LONDON UK
+44 743 8881857

PROJECT NAME:
TASTE OF VILLAGE

OWNER'S NAME:
TASTE OF VILLAGE

PRINCIPAL ARCHITECT;
M.S.
TITLE
TOILET TILE LAYOUT ELEVATION-04

CHECKED BY :
M.S.
DRAWN BY:
FAIZAN ALI

Revised Dates :
Rev. _____
Rev. _____
Rev. _____
Rev. _____
Rev. _____
Rev. _____

SCALE:
N.T.S

DATE:
22-10-2025

JOB NO.	DRG NO.
25.1030	ID -34

NOTES:
PRESENTATION
DRAWING NOT FOR
CONSTRUCTION

SECURITY MONITORING		QUANTITY
	CAMERA TYPE-1 (DOME)	09
	CAMERA TYPE-2	00
	RECORDER	01
	CONTROL MONITOR	01



36 ARCLAY CLOSE UB8 3WP
UXBRIDGE LONDON UK
+44 743 8881857

PROJECT NAME:

TASTE OF VILLAGE

OWNER'S NAME:

TASTE OF VILLAGE

PRINCIPAL ARCHITECT;

M.S.

TITLE
GROUND FLOOR
CAMERA SURVEILLANCE PLAN

CHECKED BY :

M.S.

DRAWN BY:

FAIZAN ALI

Revised Dates :

Rev. _____

Rev. _____

Rev. _____

Rev. _____

Rev. _____

SCALE:

N.T.S

DATE:

22-10-2025

JOB NO.


25.1030

DRG NO.


ID -35

NOTES:

PRESENTATION
DRAWING NOT FOR
CONSTRUCTION

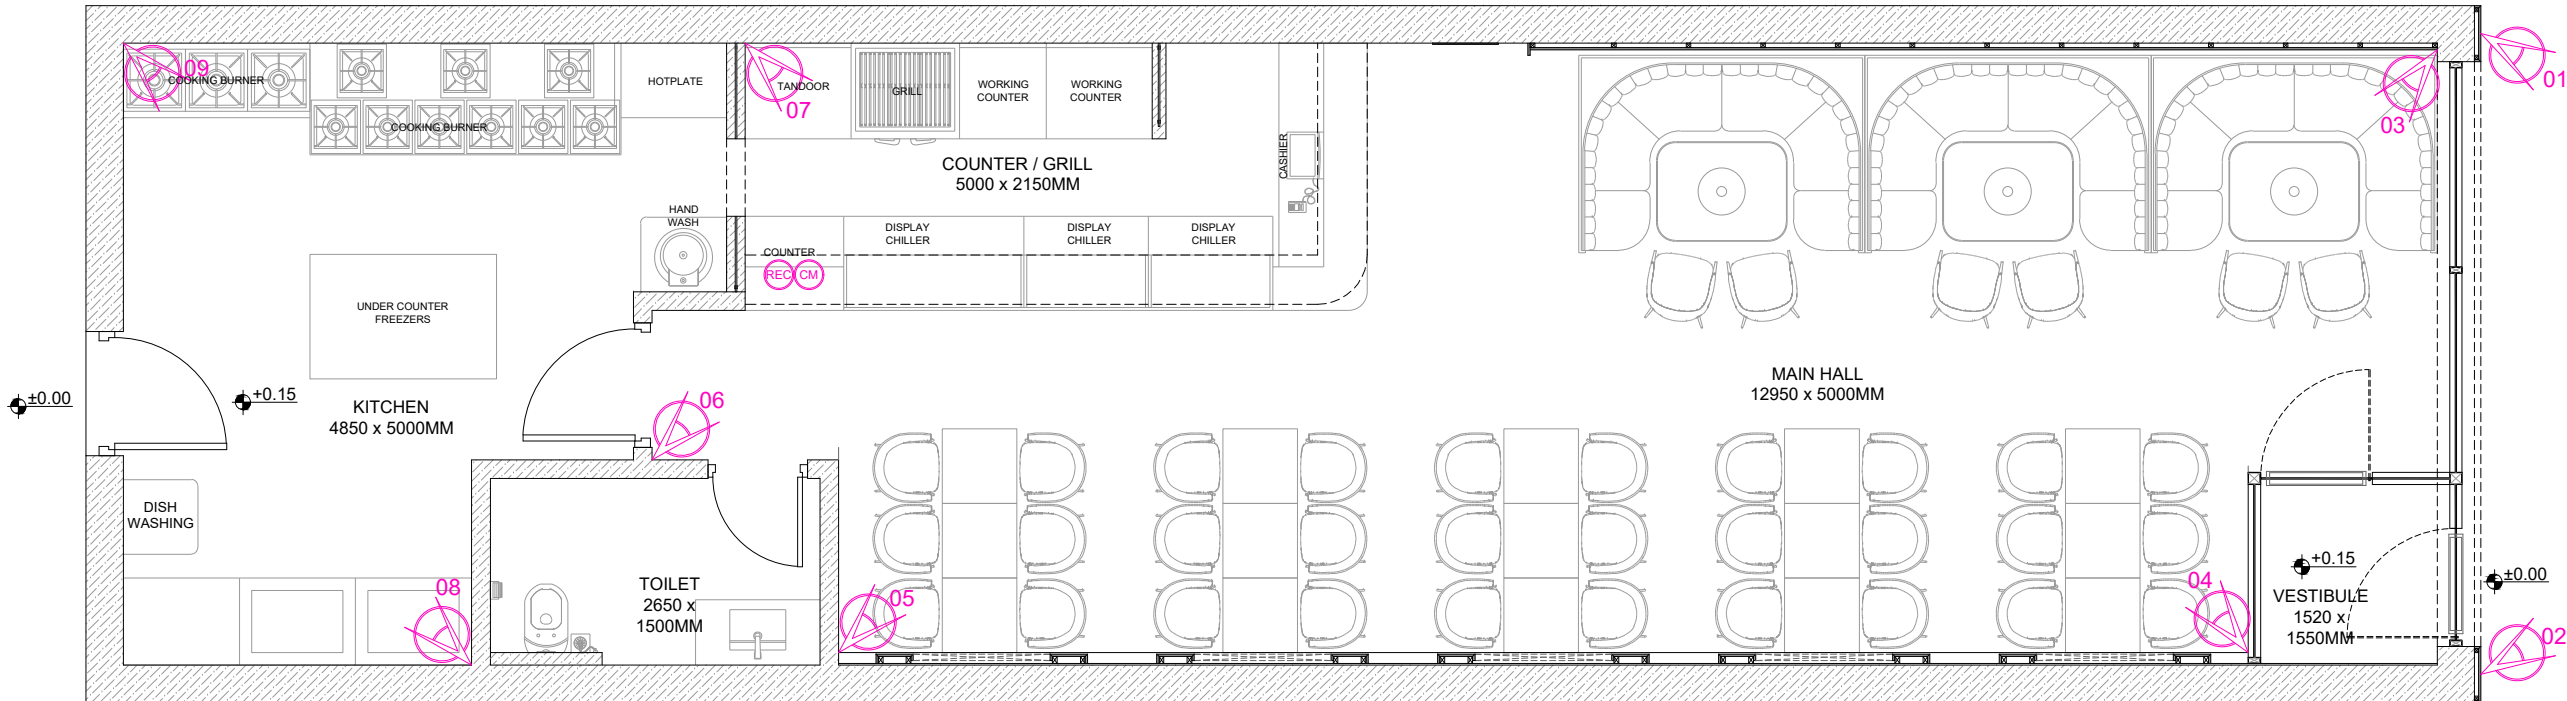

HVAC	
	MANUAL CALL POINT
	SOUNDER BEACON AUDIBLE INDICATOR
	SOUNDER BEACON VISUAL INDICATOR
	FIRE ACTION NOTICE SIGN
	FIRE EVACUATION PLAN
	FIRE EXTINGUISHER
	CO2 FIRE EXTINGUISHER
	FIRE DETECTION & SUPPRESSION SYSTEM
	TELEPHONE
	INTERNALLY ILLUMINATED FIRE EXIT SIGN BS 5266
	SMOKE DETECTOR
	HEAT DETECTOR
	FIRE BLANKET
	BREAK GLASS
	SAFETY LIGHTING

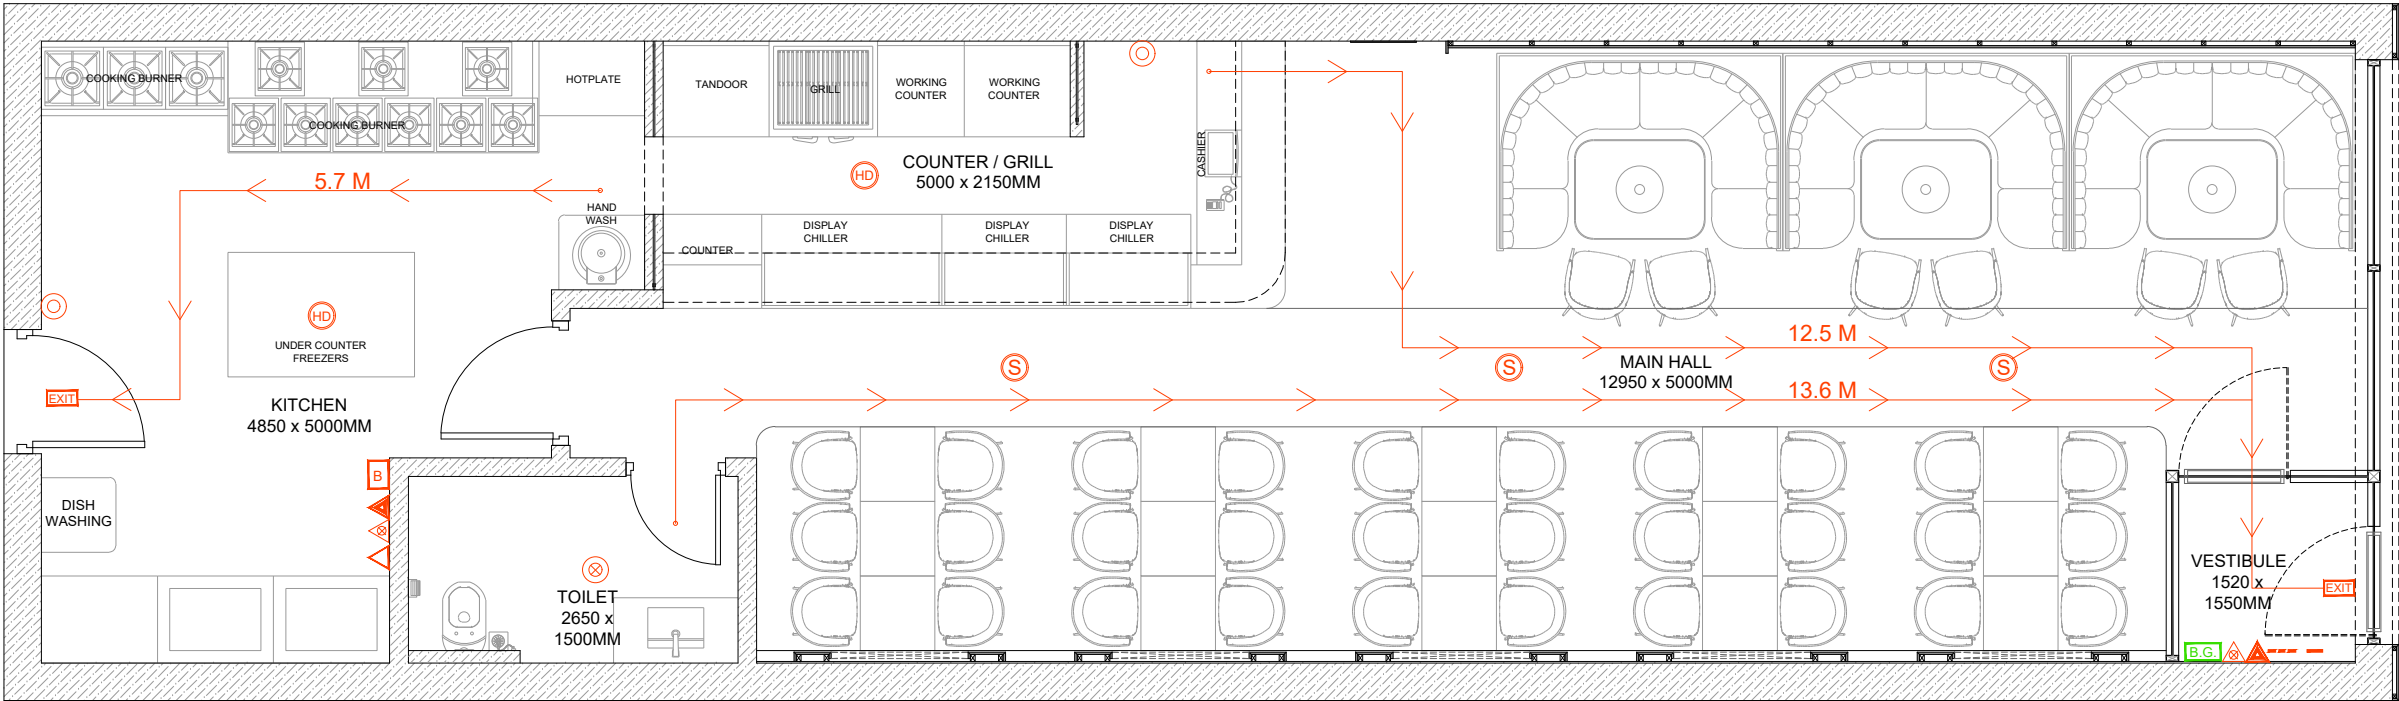

36 ARCLAY CLOSE UB8 3WP
UXBRIDGE LONDON UK
+44 743 8881857

PROJECT NAME:

TASTE OF VILLAGE

OWNER'S NAME:

TASTE OF VILLAGE

PRINCIPAL ARCHITECT;

M.S.

TITLE

GROUND FLOOR
FIRE STRATEGY PLAN

CHECKED BY :

M.S.

DRAWN BY:

FAIZAN ALI

Revised Dates :

Rev. _____

Rev. _____

Rev. _____

Rev. _____

Rev. _____

SCALE:

N.T.S

DATE:

22-10-2025

JOB NO.

25.1030


DRG NO.

ID -36

NOTES:

PRESENTATION
DRAWING NOT FOR
CONSTRUCTION

EQUIPMENT - TECH		QUANTITY
PT	PAYMENT TERMINAL	01
TT	TOUCH SCREEN TERMINAL	00
RP	RECEIPT PRINTER	01
DR	DRAWER	01
SP	SPEAKER	04
PP	PREPARATION PRINTER	01
PS	PREPARATION KITCHEN SCREEN	01

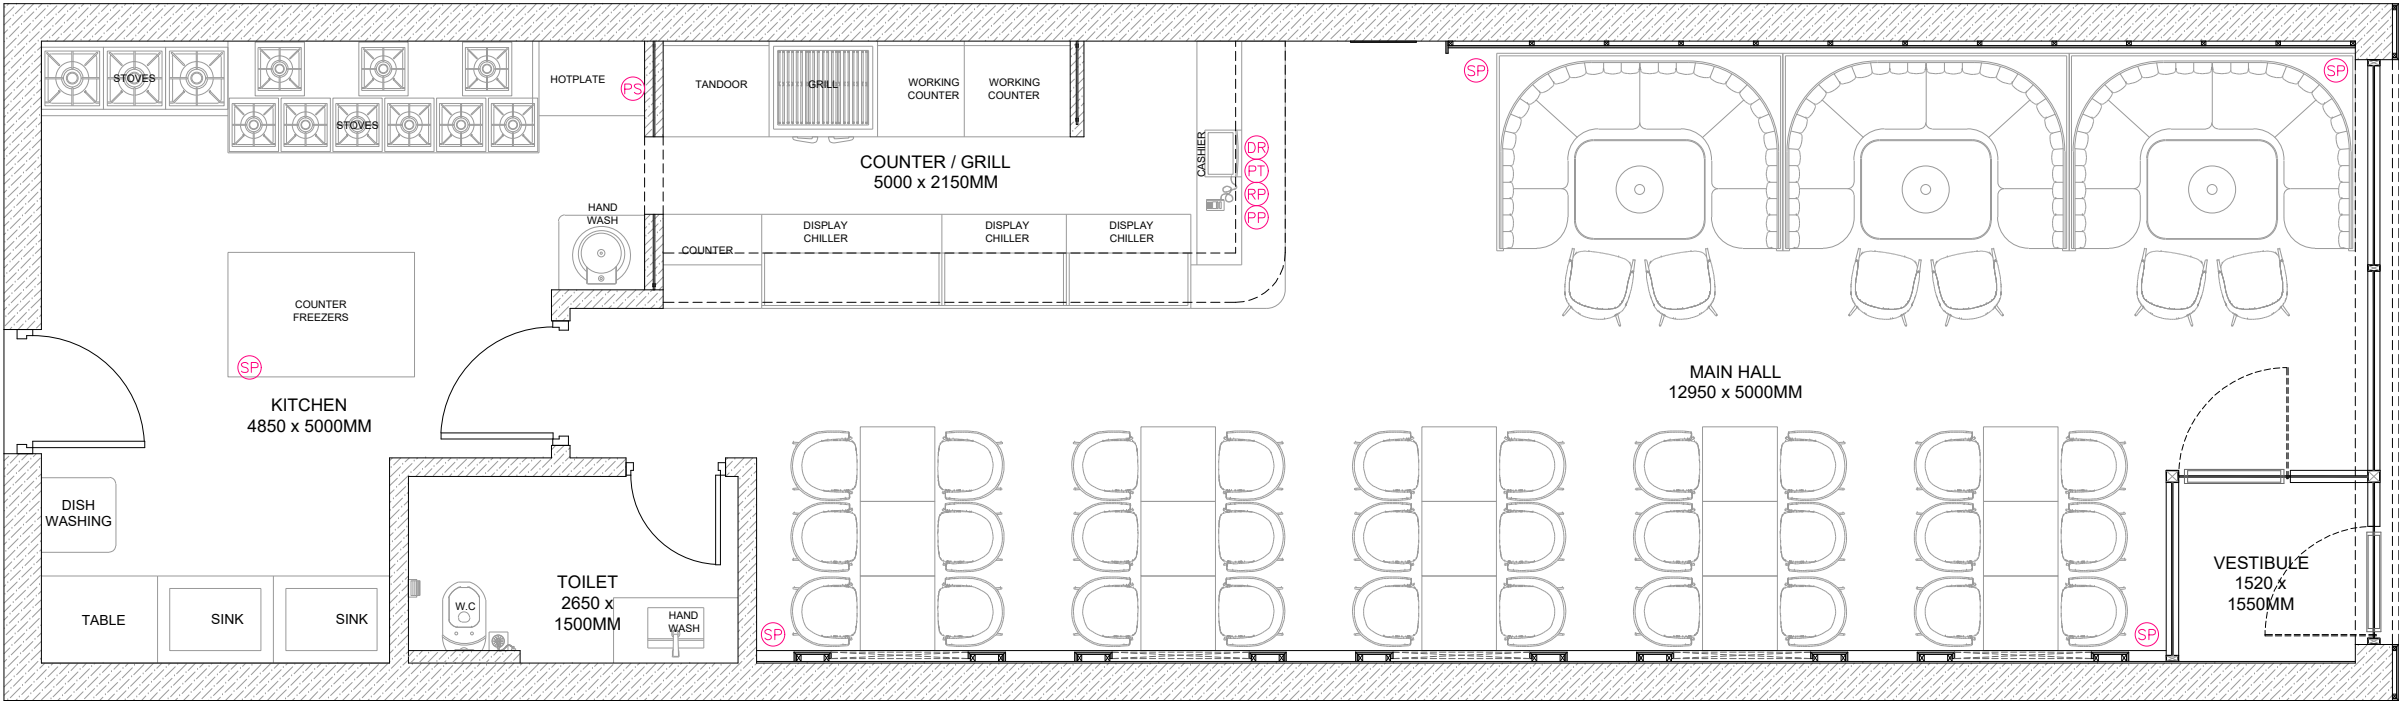

36 ARCLAY CLOSE UB8 3WP
UXBRIDGE LONDON UK
+44 743 8881857

PROJECT NAME:

TASTE OF VILLAGE

OWNER'S NAME:

TASTE OF VILLAGE

PRINCIPAL ARCHITECT;

M.S.

TITLE

GROUND FLOOR
PLACEMENT PLAN
TECH EQUIPMENTS

CHECKED BY :

M.S.

DRAWN BY:

FAIZAN ALI

Revised Dates :

Rev. _____

Rev. _____

Rev. _____

Rev. _____

Rev. _____

SCALE:

N.T.S

DATE:

22-10-2025

JOB NO.

25.1030


DRG NO.

ID -37

NOTES:

PRESENTATION
DRAWING NOT FOR
CONSTRUCTION

EQUIPMENTS - KITCHEN PREPARATION		QUANTITY
REFRIGERATOR		
ⓈⓈ	DISPLAY CHILLER	03
ⓈⓈ	FREEZERS	01
COOKING		
ⓈⓈ	GRILL	01
ⓈⓈ	TANDOOR	01
ⓈⓈ	HOT PLATE	01
ⓈⓈ	STOVES	12
PREPARATION		
ⓈⓈ	WORKING COUNTER	02
ⓈⓈ	COUNTER	01
ⓈⓈ	HAND WASH	01
ⓈⓈ	DISHWASHING	01
ⓈⓈ	STAINLESS STEEL SINK	02
ⓈⓈ	TABLE	01
GARBAGE		
ⓈⓈ	CHROME WIRE SHELVING	01

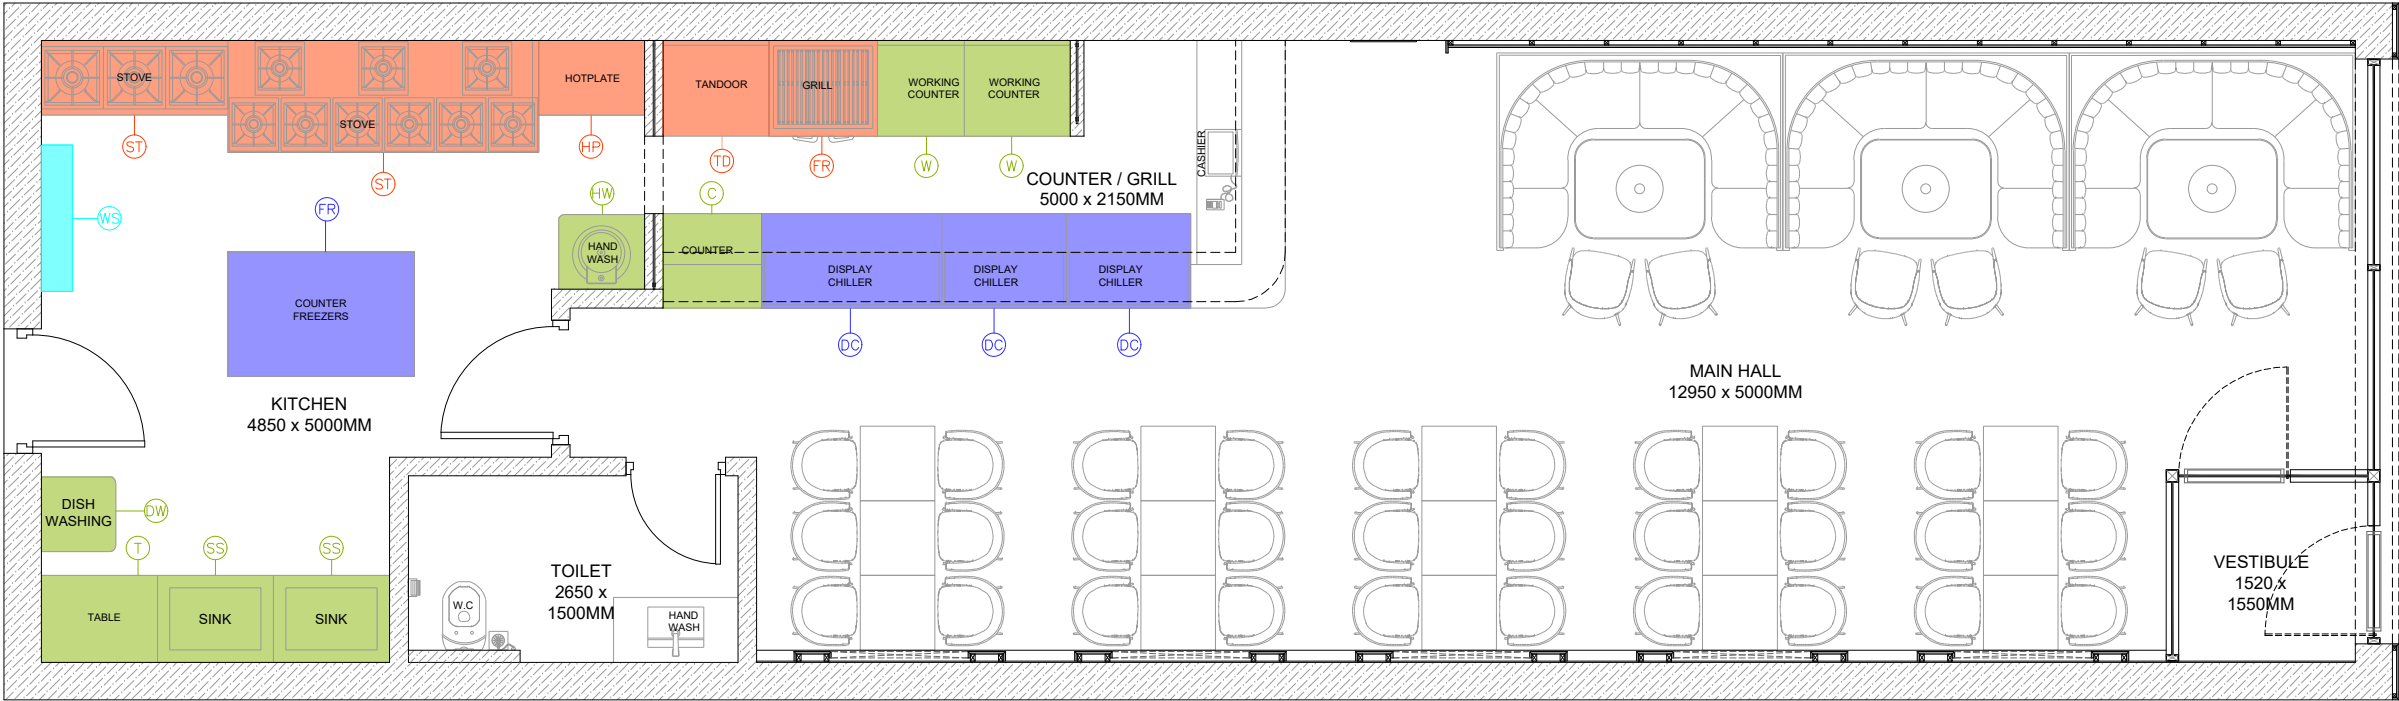

36 ARCLAY CLOSE UB8 3WP
UXBRIDGE LONDON UK

+44 743 8881857

PROJECT NAME:

TASTE OF VILLAGE

OWNER'S NAME:

TASTE OF VILLAGE

PRINCIPAL ARCHITECT;

M.S.

TITLE

GROUND FLOOR
PLACEMENT PLAN
KITCHEN EQUIPMENTS

CHECKED BY :

M.S.

DRAWN BY:

FAIZAN ALI

Revised Dates :

Rev. _____

Rev. _____

Rev. _____

Rev. _____

Rev. _____

SCALE:

N.T.S

DATE:

22-10-2025

JOB NO.






25.1030


DRG NO.

ID -38

NOTES:

PRESENTATION
DRAWING NOT FOR
CONSTRUCTION

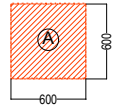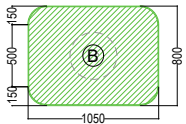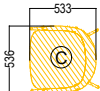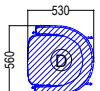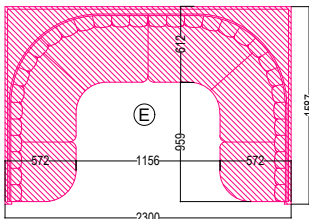LEGEND	QUANTITY	NAME
	15	COFFEE TABLE
	03	CENTER TABLE
	06	CHAIR
	30	CHAIR
	03	SOFA

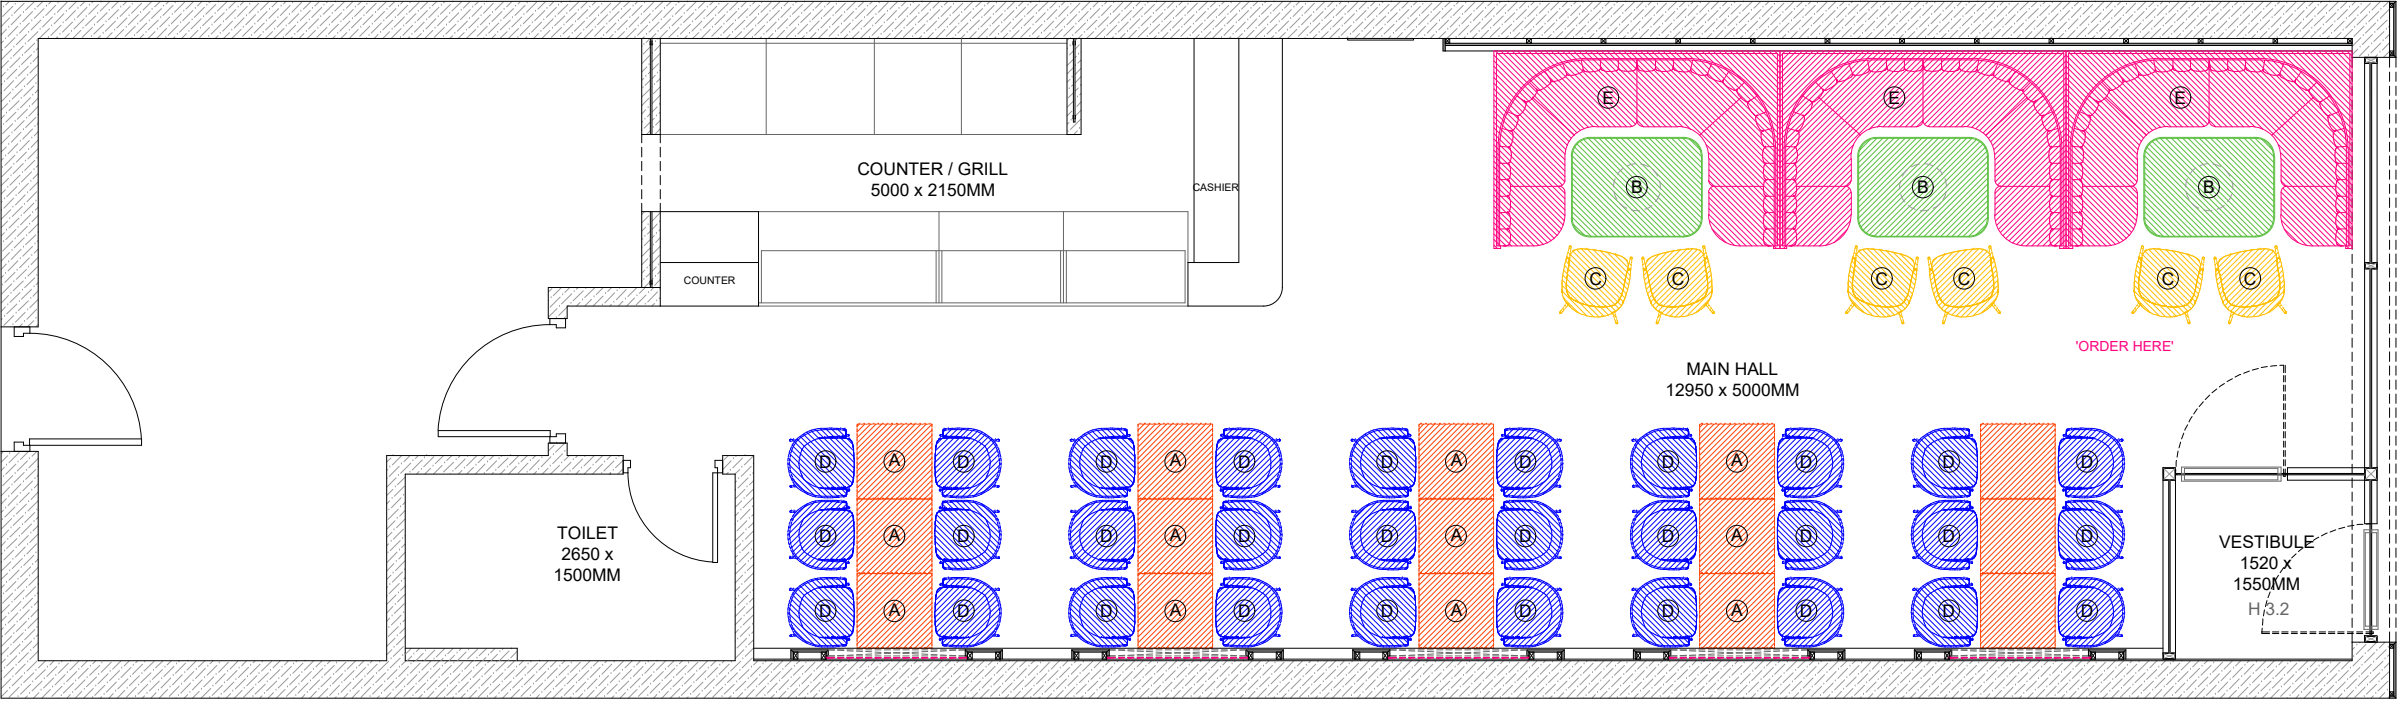

36 ARCLAY CLOSE UB8 3WP
UXBRIDGE LONDON UK
+44 743 8881857

PROJECT NAME:
TASTE OF VILLAGE

OWNER'S NAME:
TASTE OF VILLAGE

PRINCIPAL ARCHITECT;
M.S.

TITLE
GROUND FLOOR
FURNITURE LAYOUT PLAN

CHECKED BY :

M.S.

DRAWN BY:

FAIZAN ALI

Revised Dates :

Rev. _____

Rev. _____

Rev. _____

Rev. _____

Rev. _____

SCALE:

N.T.S

DATE:

22-10-2025

JOB NO.

25.1030


DRG NO.

ID -39

NOTES:

PRESENTATION
DRAWING NOT FOR
CONSTRUCTION

EQUIPMENT - SANITARY		QUANTITY
(W.C)	GEBERIT ONE DISABLE W.C	01
(FR)	GEBERIT DUOFIX REINFORCED W.C FRAME FOR DISABLE W.C	00
(FP)	GEBERIT SIGMA 01 BLACK DUAL FLASH PLATE	01
(CC)	GEBERIT SELNOVA FLOOR - STANDING CLOSE COUPLE TOILET	01
(SR)	TWYFORD DISABILITY HINGED SUPPORT RAIL	02
(B)	AREZZO STONE WALL HUNG GRAY BASIN	01
(TR)	AREZZO MATT BLACK TRAP & ISOLATING SET	01
(MX)	PABLO MATT BLACK BASIN MIXER TAP	05
(D)	DYSON AIR BLADE V HAND DRYER	01
(SD)	TORK LIQUID SOAP DISPENSER	02
(TRD)	TOR MINI JUMBO TOILET ROLL DISPENSER	01
(HTD)	TORK MATIC AUTOMATIC HAND TOWEL ROLL DISPENSER	01
(CD)	TORK REFLEX SINGLE SHEET MINI CENTREFEED DISPENSER	03

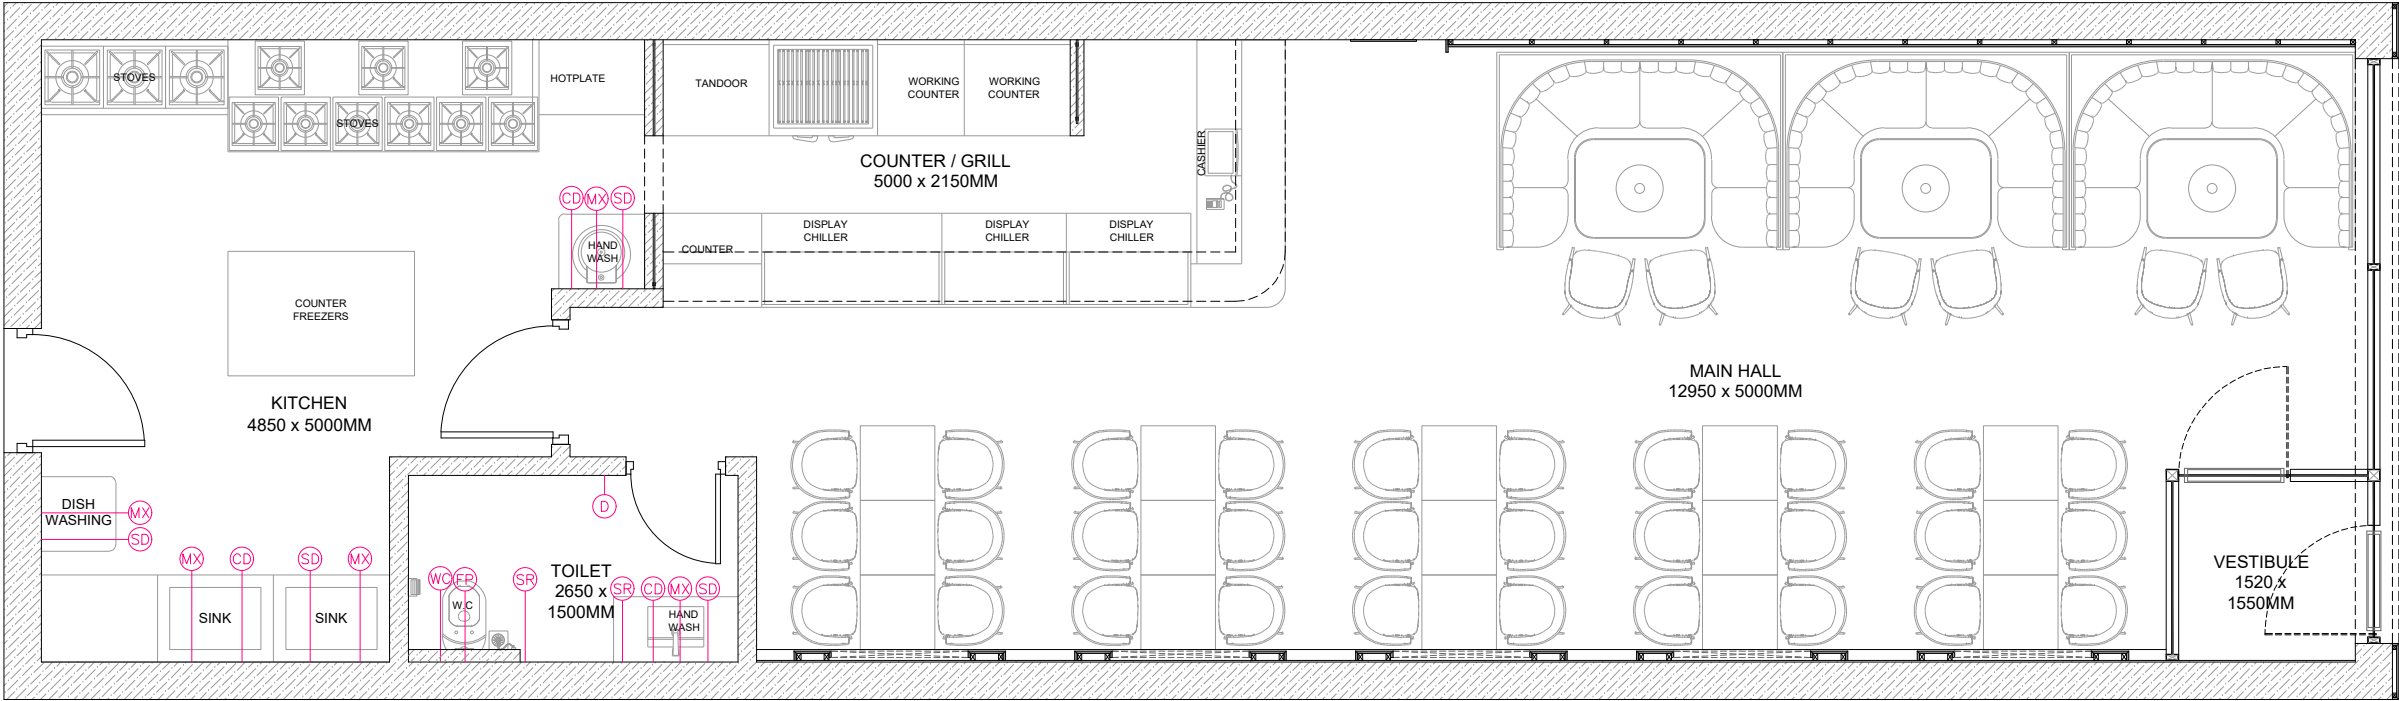

36 ARCLAY CLOSE UB8 3WP
UXBRIDGE LONDON UK
+44 743 8881857

PROJECT NAME:

TASTE OF VILLAGE

OWNER'S NAME:

TASTE OF VILLAGE

PRINCIPAL ARCHITECT;

M.S.

TITLE

GROUND FLOOR
PLACEMENT PLAN
SANITARY EQUIPMENTS

CHECKED BY :

M.S.

DRAWN BY:

FAIZAN ALI

Revised Dates :

Rev. _____

Rev. _____

Rev. _____

Rev. _____

SCALE:

N.T.S

DATE:

22-10-2025

JOB NO.

25.1030

DRG NO.

ID -40

NOTES:

PRESENTATION
DRAWING NOT FOR
CONSTRUCTION